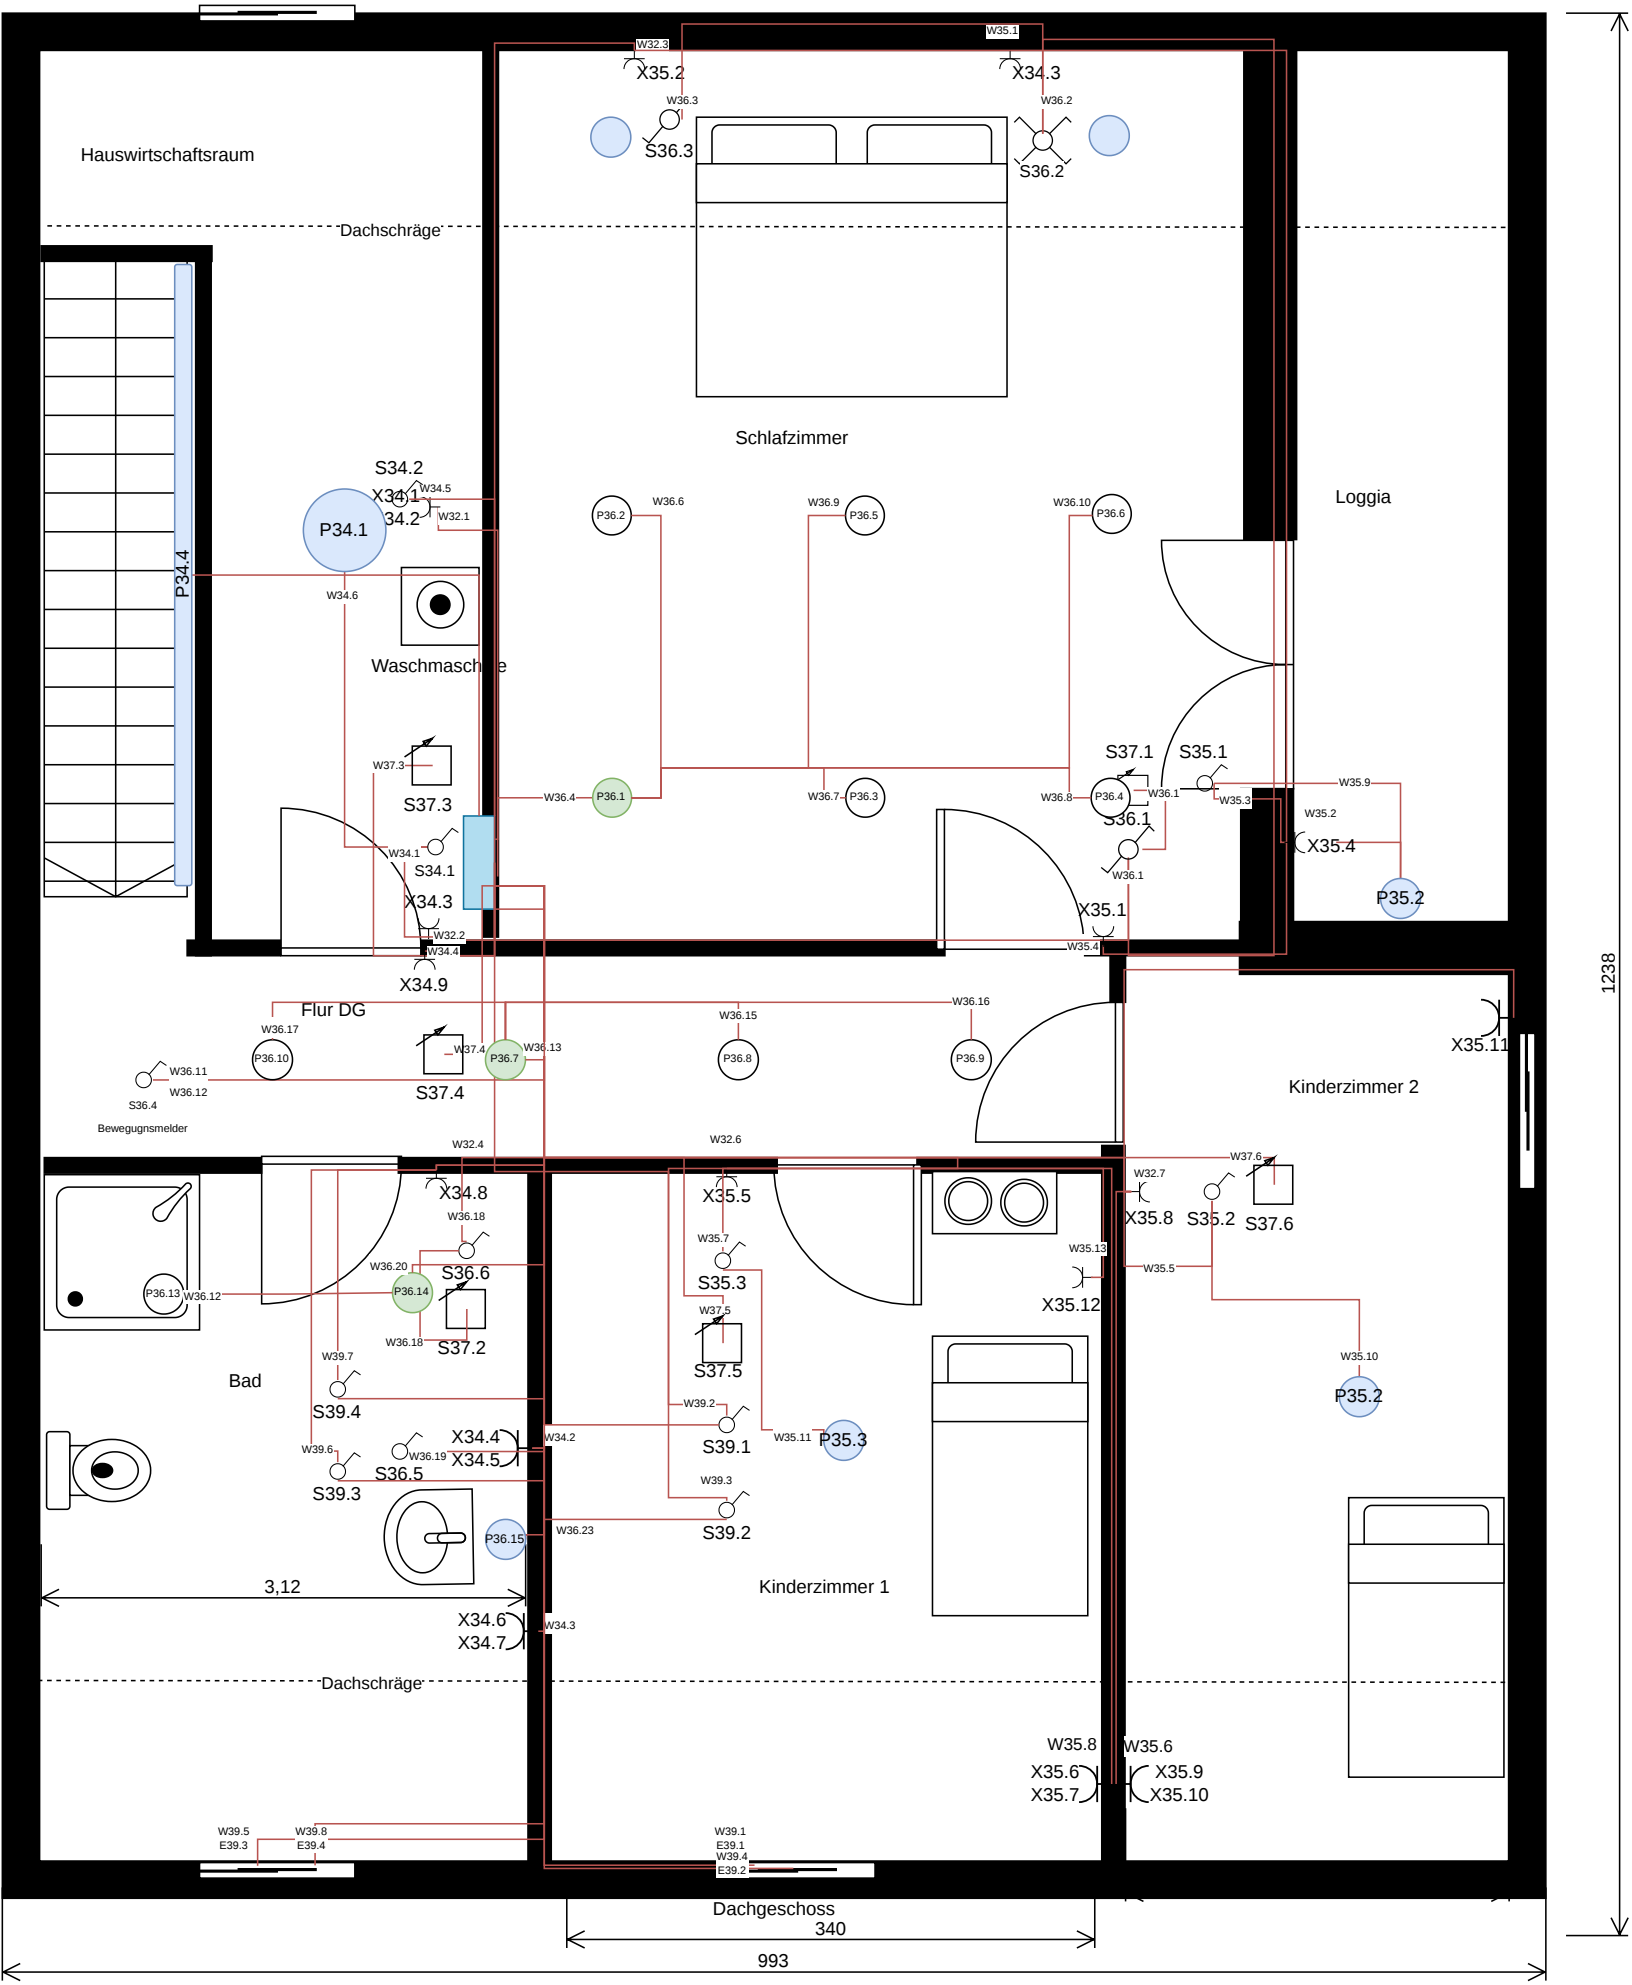

Hauswirtschaftsraum
Dachschräge
Schlafzimmer
Loggia
Waschmaschine
Flur DG
Bad
Kinderzimmer 1
Kinderzimmer 2
Bewegungsmelder
P34.4
P34.1
S34.2
X34.1
X34.2
W34.5
W32.1
W34.6
W32.3
X35.2
W35.1
X34.3
W36.3
S36.3
W36.2
S36.2
P36.2
W36.6
P36.5
W36.9
P36.6
W36.10
W37.3
S37.3
W36.4
P36.1
W36.7
P36.3
W36.8
P36.4
W36.1
S37.1
S35.1
W35.3
W35.9
W35.2
X35.4
S36.1
W36.1
P35.2
S34.1
X34.3
W34.1
W32.2
W34.4
X34.9
X35.1
W35.4
W36.16
W36.15
W36.17
P36.10
W37.4
P36.7
W36.13
P36.8
P36.9
W36.11
W36.12
S36.4
S37.4
X35.11
W32.4
W32.6
W37.6
W32.7
X34.8
X35.5
X35.8
S35.2
S37.6
W36.18
W35.7
W36.20
S36.6
S35.3
W35.13
X35.12
W35.5
P36.13
W36.12
P36.14
W36.18
S37.2
W37.5
S37.5
W39.7
W35.10
P35.2
S39.4
W39.2
X34.4
X34.5
W34.2
S39.1
W35.11
P35.3
W39.6
W36.19
S36.5
S39.3
W39.3
S39.2
P36.15
W36.23
3,12
X34.6
X34.7
W34.3
W35.8
W35.6
X35.6
X35.7
X35.9
X35.10
W39.5
E39.3
W39.8
E39.4
W39.1
E39.1
W39.4
E39.2
Dachgeschoss
340
993
1238