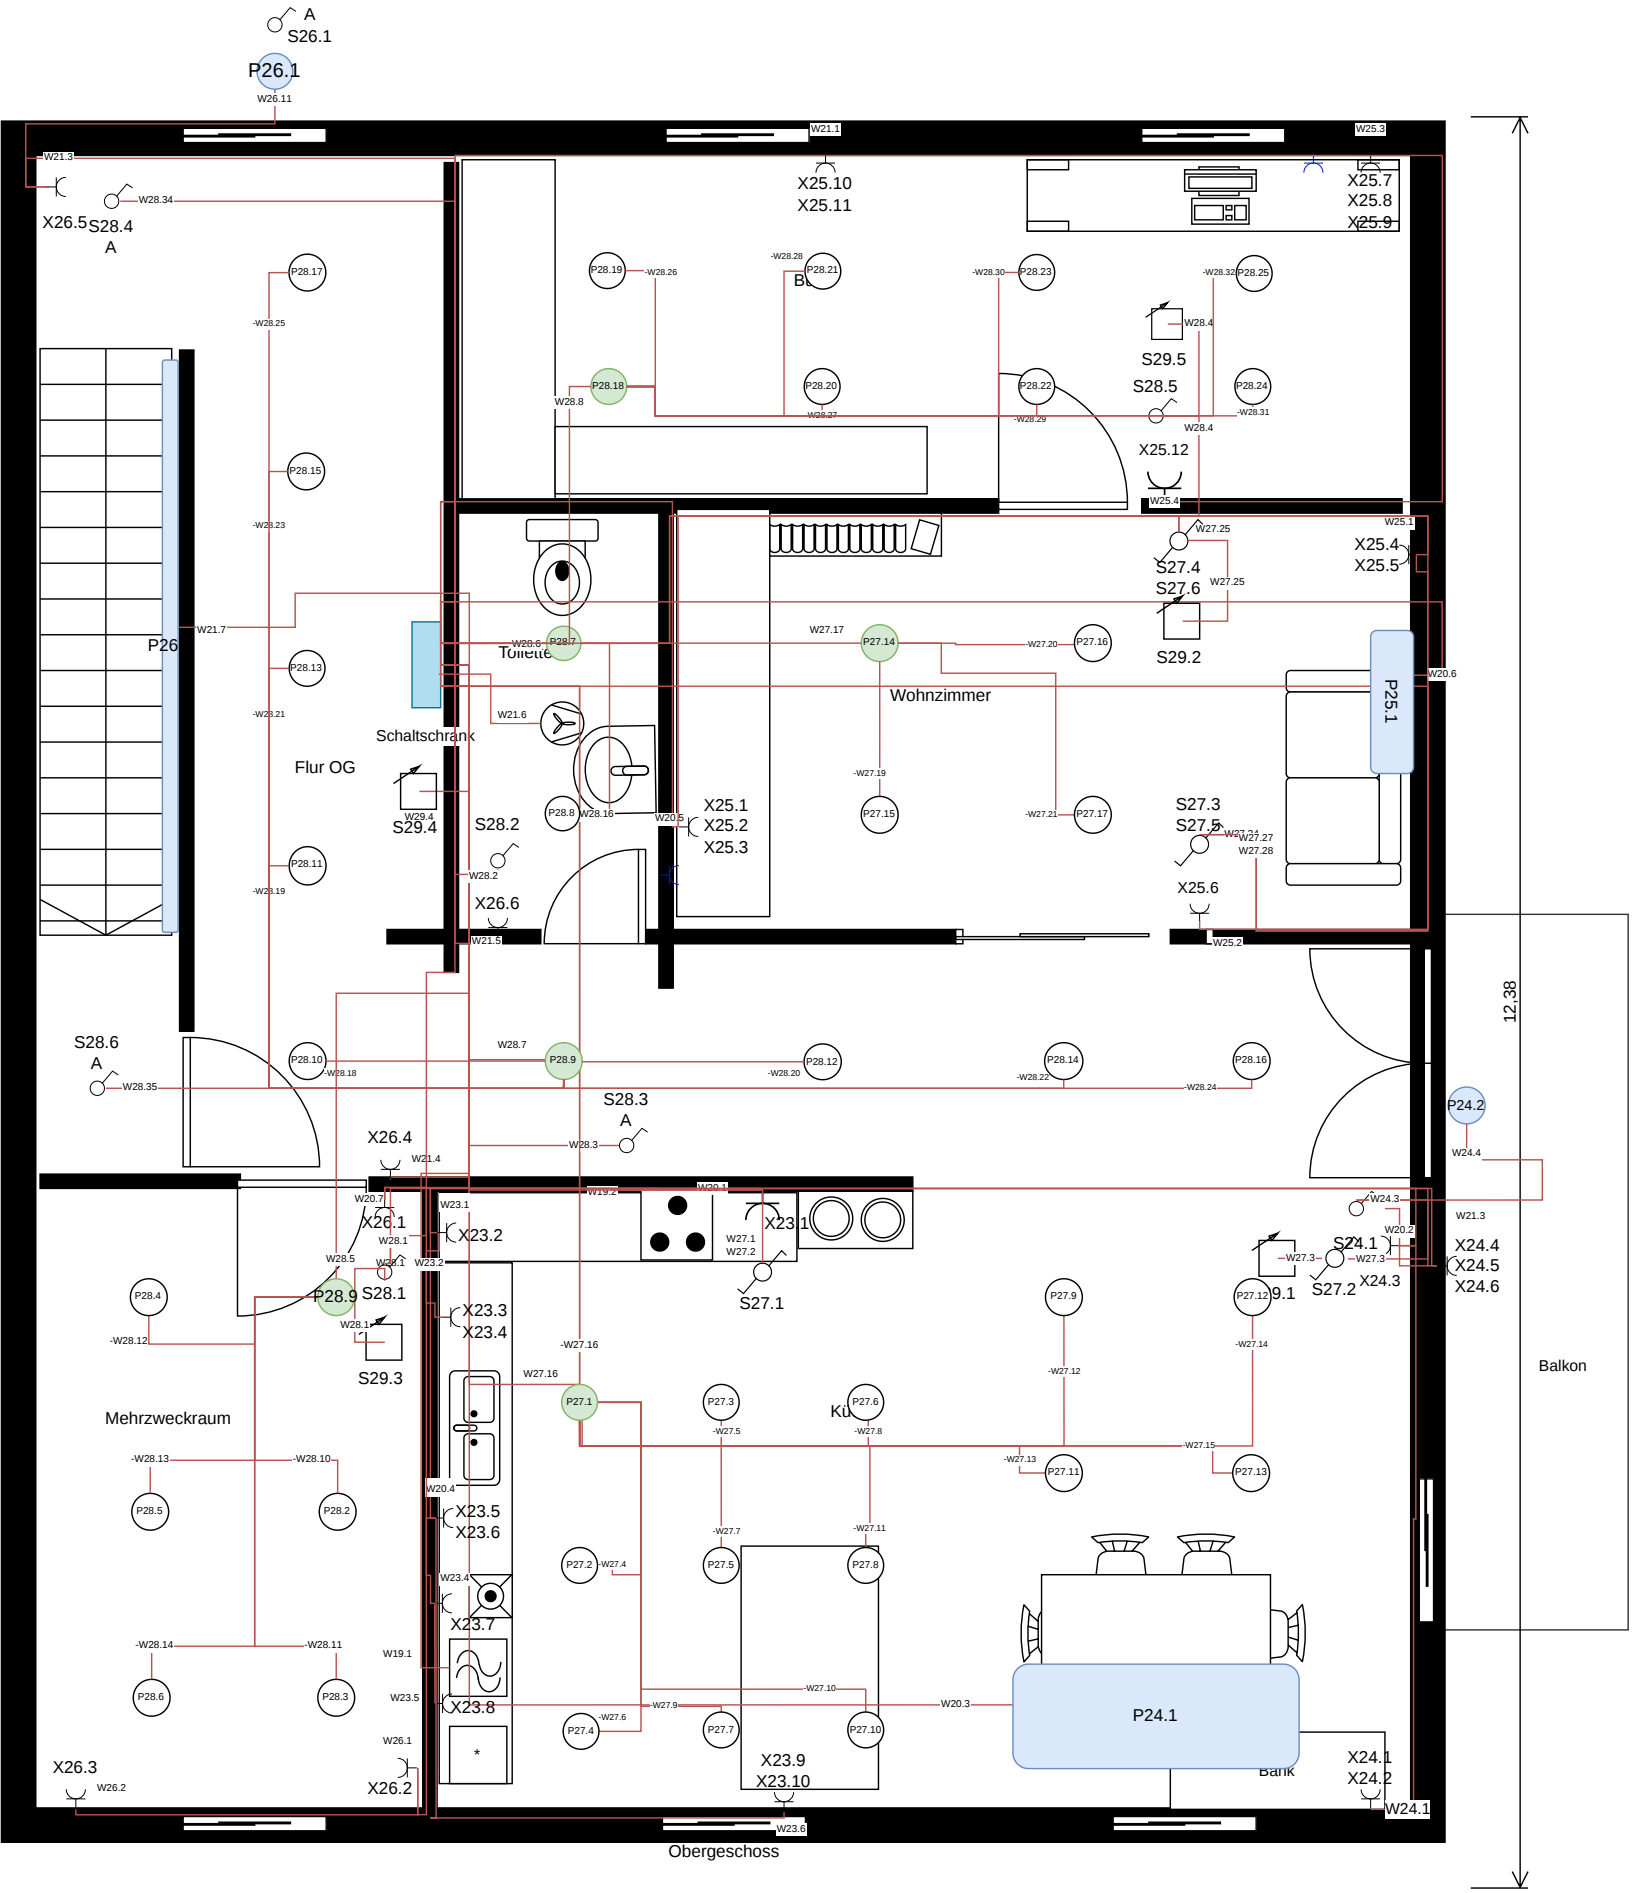

A
S26.1
P26.1
W26.11
W21.3
X26.5
W28.34
S28.4
A
W21.1
X25.10
X25.11
W25.3
X25.7
X25.8
X25.9
P28.17
P28.19
W28.26
W28.28
P28.21
W28.30
P28.23
W28.32
P28.25
W28.4
S29.5
S28.5
P28.18
W28.8
P28.20
W28.27
P28.22
W28.29
P28.24
W28.31
W28.4
X25.12
W25.4
P28.15
W28.23
W27.25
W25.1
X25.4
X25.5
S27.4
S27.6
W27.25
P26
W21.7
P28.13
W28.6
P28.7
Toilette
W27.17
P27.14
W27.20
P27.16
S29.2
W20.6
W28.21
Wohnzimmer
P25.1
W21.6
Schaltschrank
Flur OG
W29.4
S29.4
S28.2
P28.8
W28.16
W20.5
X25.1
X25.2
X25.3
W27.19
P27.15
W27.21
P27.17
S27.3
S27.5
W27.27
W27.28
X25.6
P28.11
W28.19
W28.2
X26.6
W21.5
W25.2
S28.6
A
W28.35
P28.10
W28.18
W28.7
P28.9
W28.20
P28.12
W28.22
P28.14
W28.24
P28.16
S28.3
A
P24.2
W24.4
X26.4
W21.4
W28.3
W20.7
W19.2
W20.1
W24.3
W21.3
X26.1
W23.1
X23.2
X23.1
W27.1
W27.2
W28.1
W20.2
W28.5
W23.2
W27.3
S24.1
X24.4
X24.5
X24.6
P28.4
W28.12
P28.9
S28.1
W28.1
S27.1
S27.2
X24.3
X23.3
X23.4
P27.9
P27.12
9.1
W27.16
W27.12
W27.14
S29.3
Mehrzweckraum
P27.1
P27.3
W27.5
Kü
P27.6
W27.8
W27.15
W27.13
P27.11
P27.13
W28.13
W28.10
W20.4
X23.5
X23.6
P28.5
P28.2
W27.7
W27.11
P27.2
W27.4
P27.5
P27.8
W23.4
X23.7
W28.14
W28.11
W19.1
W23.5
X23.8
P28.6
P28.3
W27.9
W27.10
W20.3
P24.1
W27.6
P27.4
P27.7
P27.10
W26.1
*
X23.9
X23.10
Bank
X24.1
X24.2
X26.3
W26.2
X26.2
W24.1
W23.6
Obergeschoss
12,38
Balkon