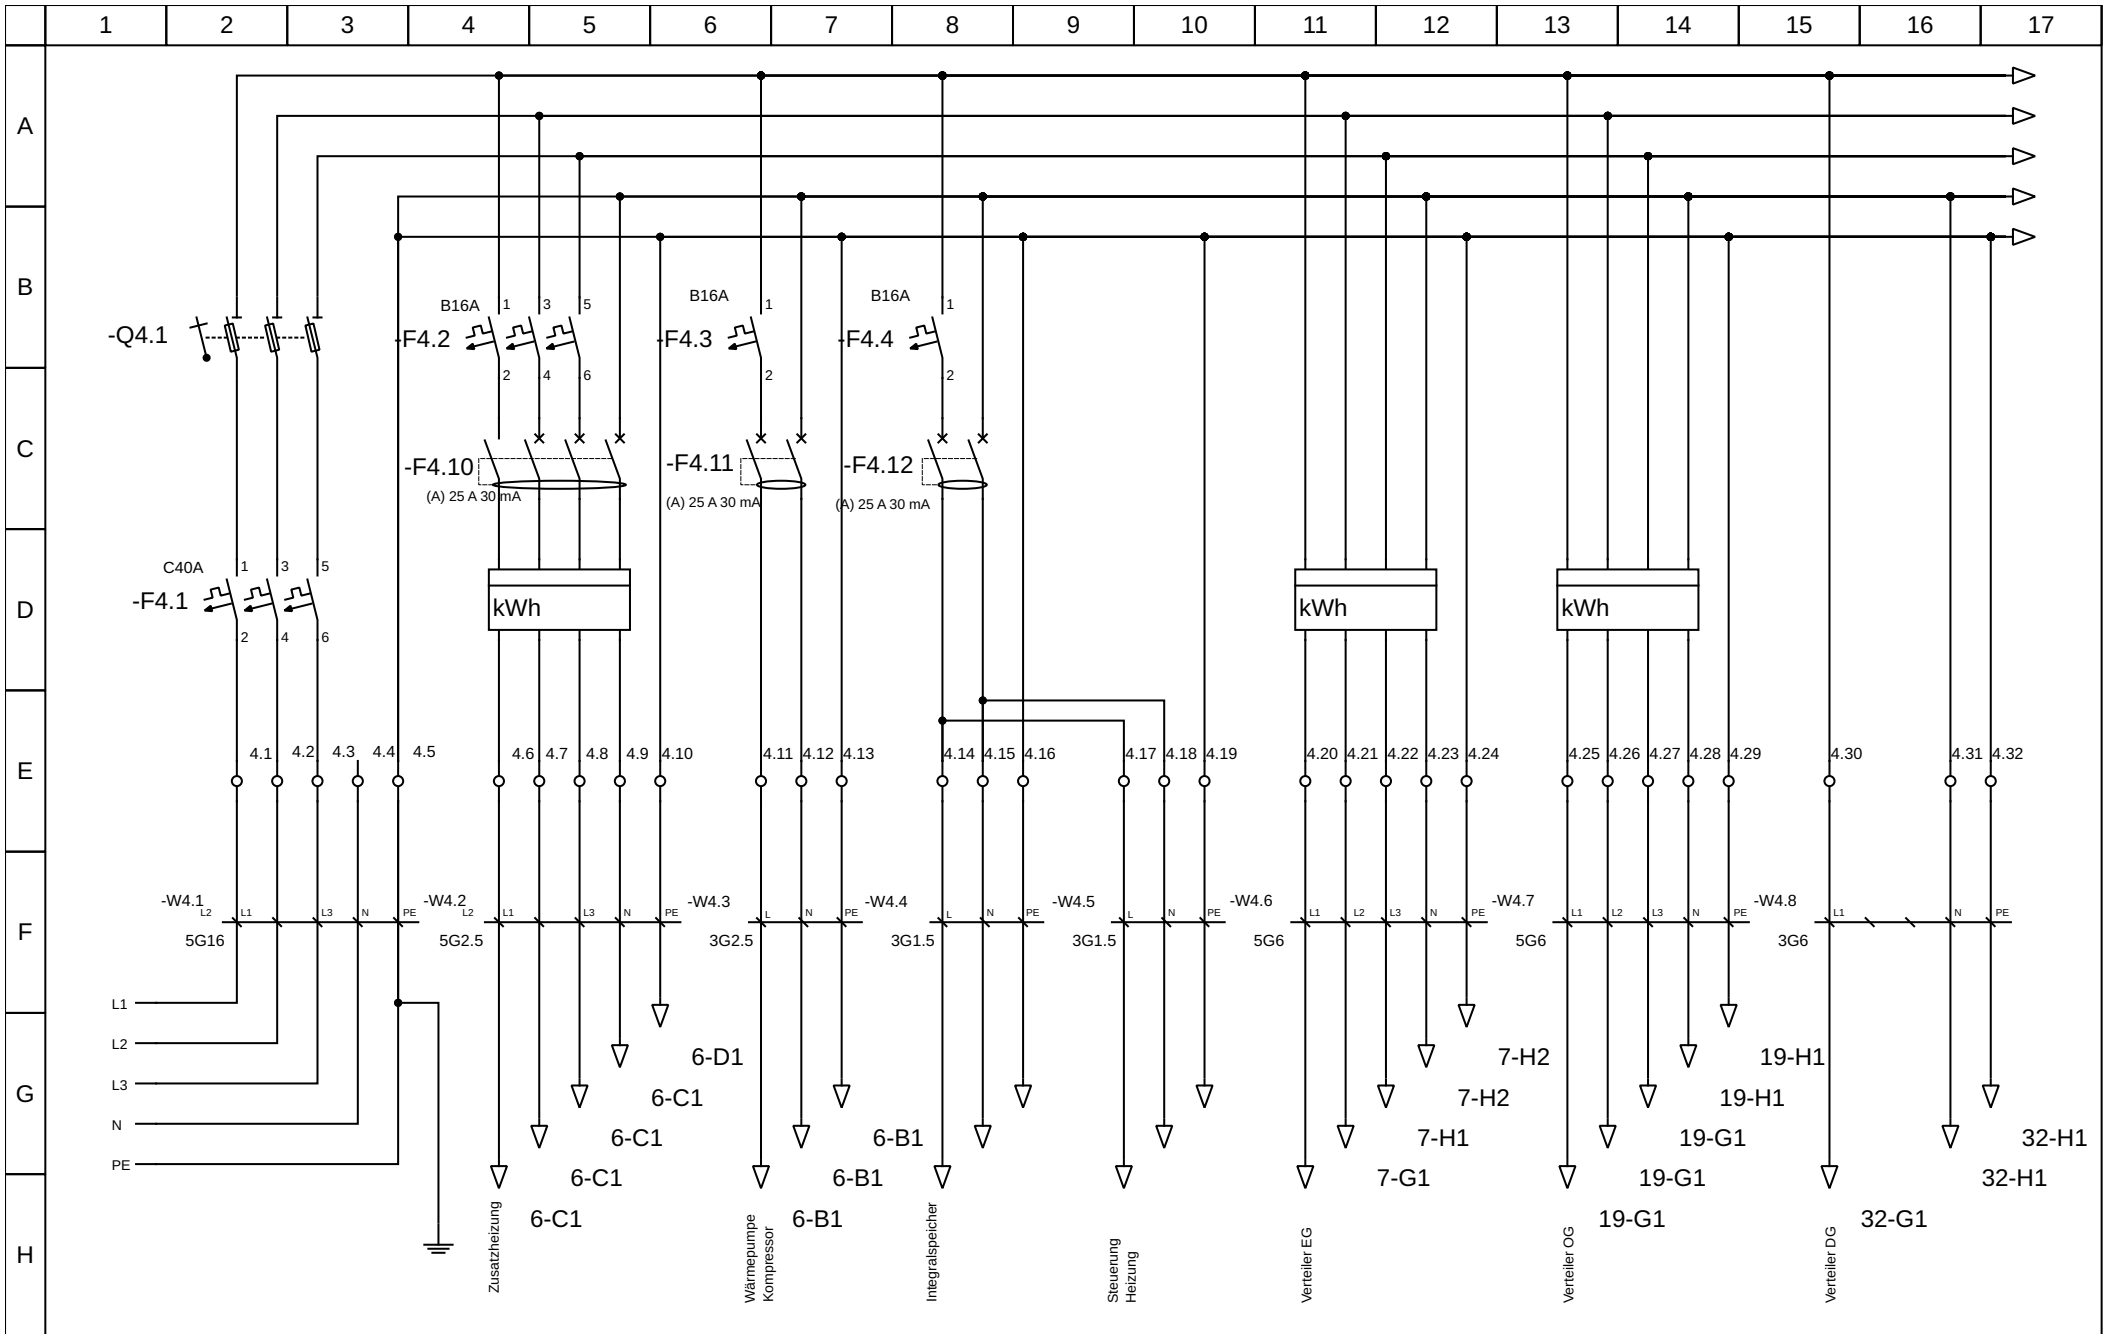
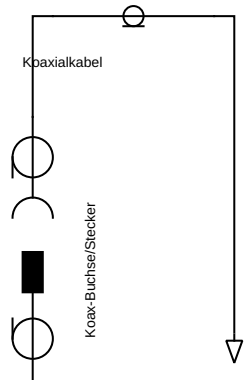
| Seite | Titel | Anlage (=) | Ort (+) | Foliennummer | Revisionsindex |
|---|---|---|---|---|---|
| 1 | Inhaltsverzeichniss | EG | | 1/39 | |
| 4 | Hauptversorgung | EG | Technikraum | 4/39 | 01 |
| 5 | Daten | EG | Technikraum | 5/39 | 01 |
| 6 | Heizung | EG | Wärmepump | 6/39 | 01 |
| 7 | Sicherung | EG | Verteiler | 7/39 | 01 |
| 8 | Sicherung | EG | Verteiler | 8/39 | 01 |
| 9 | Kleinspannungversorgung | EG | Verteiler | 9/39 | 01 |
| 10 | Hauptstrom Küche | EG | Küche | 10/39 | 01 |
| 11 | Hauptstrom Bad | EG | Bad | 11/39 | 01 |
| 12 | Hauptstrom | EG | Wohnzimmer Schlafzimmer Terasse | 12/39 | 01 |
| 13 | Hauptstrom | EG | WC Eingang Flur Bad | 13/39 | 01 |
| 14 | Kleinspannung | EG | Küche Wohnzimmer Schlafzimmer Bad | 14/39 | 01 |
| 15 | Kleinspannung | EG | Flur WC Eingang | 15/39 | 01 |
| 16 | Thermostate | EG | Küche Wohnzimmer Bad Schlafzimmer Flur | 16/39 | 01 |
| 17 | Daten | EG | Verteiler Wohnzimmer | 17/39 | 01 |
| 18 | Klemmenplan | EG | Verteiler | 18/39 | 01 |

| Seite | Titel | Anlage (=) | Ort (+) | Foliennummer | Revisionsindex |
|---|---|---|---|---|---|
| 2 | Inhaltsverzeichniss | OG | | 2/39 | 01 |
| 19 | Sicherung | OG | Verteiler | 19/39 | 01 |
| 20 | Sicherung | OG | Verteiler | 20/39 | 01 |
| 21 | Sicherung | OG | Küche | 21/39 | 01 |
| 22 | Kleinspannungsversorgung | OG | Verteiler | 22/39 | 01 |
| 23 | Hauptstrom Küche | OG | Küche | 23/39 | 01 |
| 24 | Hauptstrom | OG | Küche Esstisch Balkon | 24/39 | 01 |
| 25 | Hauptstrom | OG | Wohnzimmer Büro | 25/39 | 01 |
| 26 | Hauptstrom | OG | Mehrzweckraum Flur WC Balkon | 26/39 | 01 |
| 27 | Kleinspannung | OG | Küche Wohnzimmer | 27/39 | 01 |
| 28 | Kleinspannung | OG | WC Flur Mehrzweckraum Büro | 28/39 | 01 |
| 29 | Thermostate | OG | Verteiler | 29/39 | 01 |
| 30 | Daten | OG | Verteiler | 30/39 | 01 |
| 31 | Klemmenplan | OG | Verteiler | 31/39 | 01 |


| Seite | Titel | Anlage (=) | Ort (+) | Foliennummer | Revisionsindex |
|---|---|---|---|---|---|
| 3 | Inhaltsverzeichniss | DG | | 3/39 | 01 |
| 32 | Sicherung | DG | Verteiler | 32/39 | 01 |
| 33 | Kleinspannungsversorgung | DG | Verteiler | 33/39 | 01 |
| 34 | Hauptstrom | DG | HW Bad | 34/39 | 01 |
| 35 | Hauptstrom | DG | Schlafzimmer Flur Kind1 Kind2 | 35/39 | |
| 36 | Kleinspannung | DG | Schlafzimmer Flur Bad | 36/39 | |
| 37 | Thermostate | DG | Verteiler | 37/39 | 01 |
| 38 | Dachfenster | DG | Bad-Kind1 | 38/39 | |
| 39 | Klemmenplan | DG | Verteiler | 39/39 | 01 |




| | | |
|---|---|---|
| Autor: Entrich | Hauptversorgung | Datei: |
| Datum: 10/16/26 | | Seite: 4/39 |




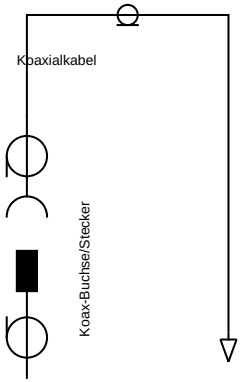
17-C1




17-B1

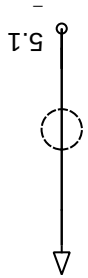
Bus - Heizung?





6-A1

| | | | | | | | | | | | | | | | | |
|---|---|---|---|---|---|---|---|---|---|---|---|---|---|---|---|---|
| | 1 | 2 | 3 | 4 | 5 | 6 | 7 | 8 | 9 | 10 | 11 | 12 | 13 | 14 | 15 | 16 | 17 |
| A | | | | | | | | | | | | | | | | | |
| B | | | | | | | | | | | | | | | | | |
| C | | | | | | | | | | | | | | | | | |
| D | | | | | | | | | | | | | | | | | |
| E | | | | | | | | | | | | | | | | | |
| F | | | | | | | | | | | | | | | | | |
| G | | | | | | | | | | | | | | | | | |
| H | | | | | | | | | | | | | | | | | |


| | | |
|---|---|---|
| Autor: Entrich | Daten | Datei: |
| Datum: 10/16/26 | | Seite: 5/39 |

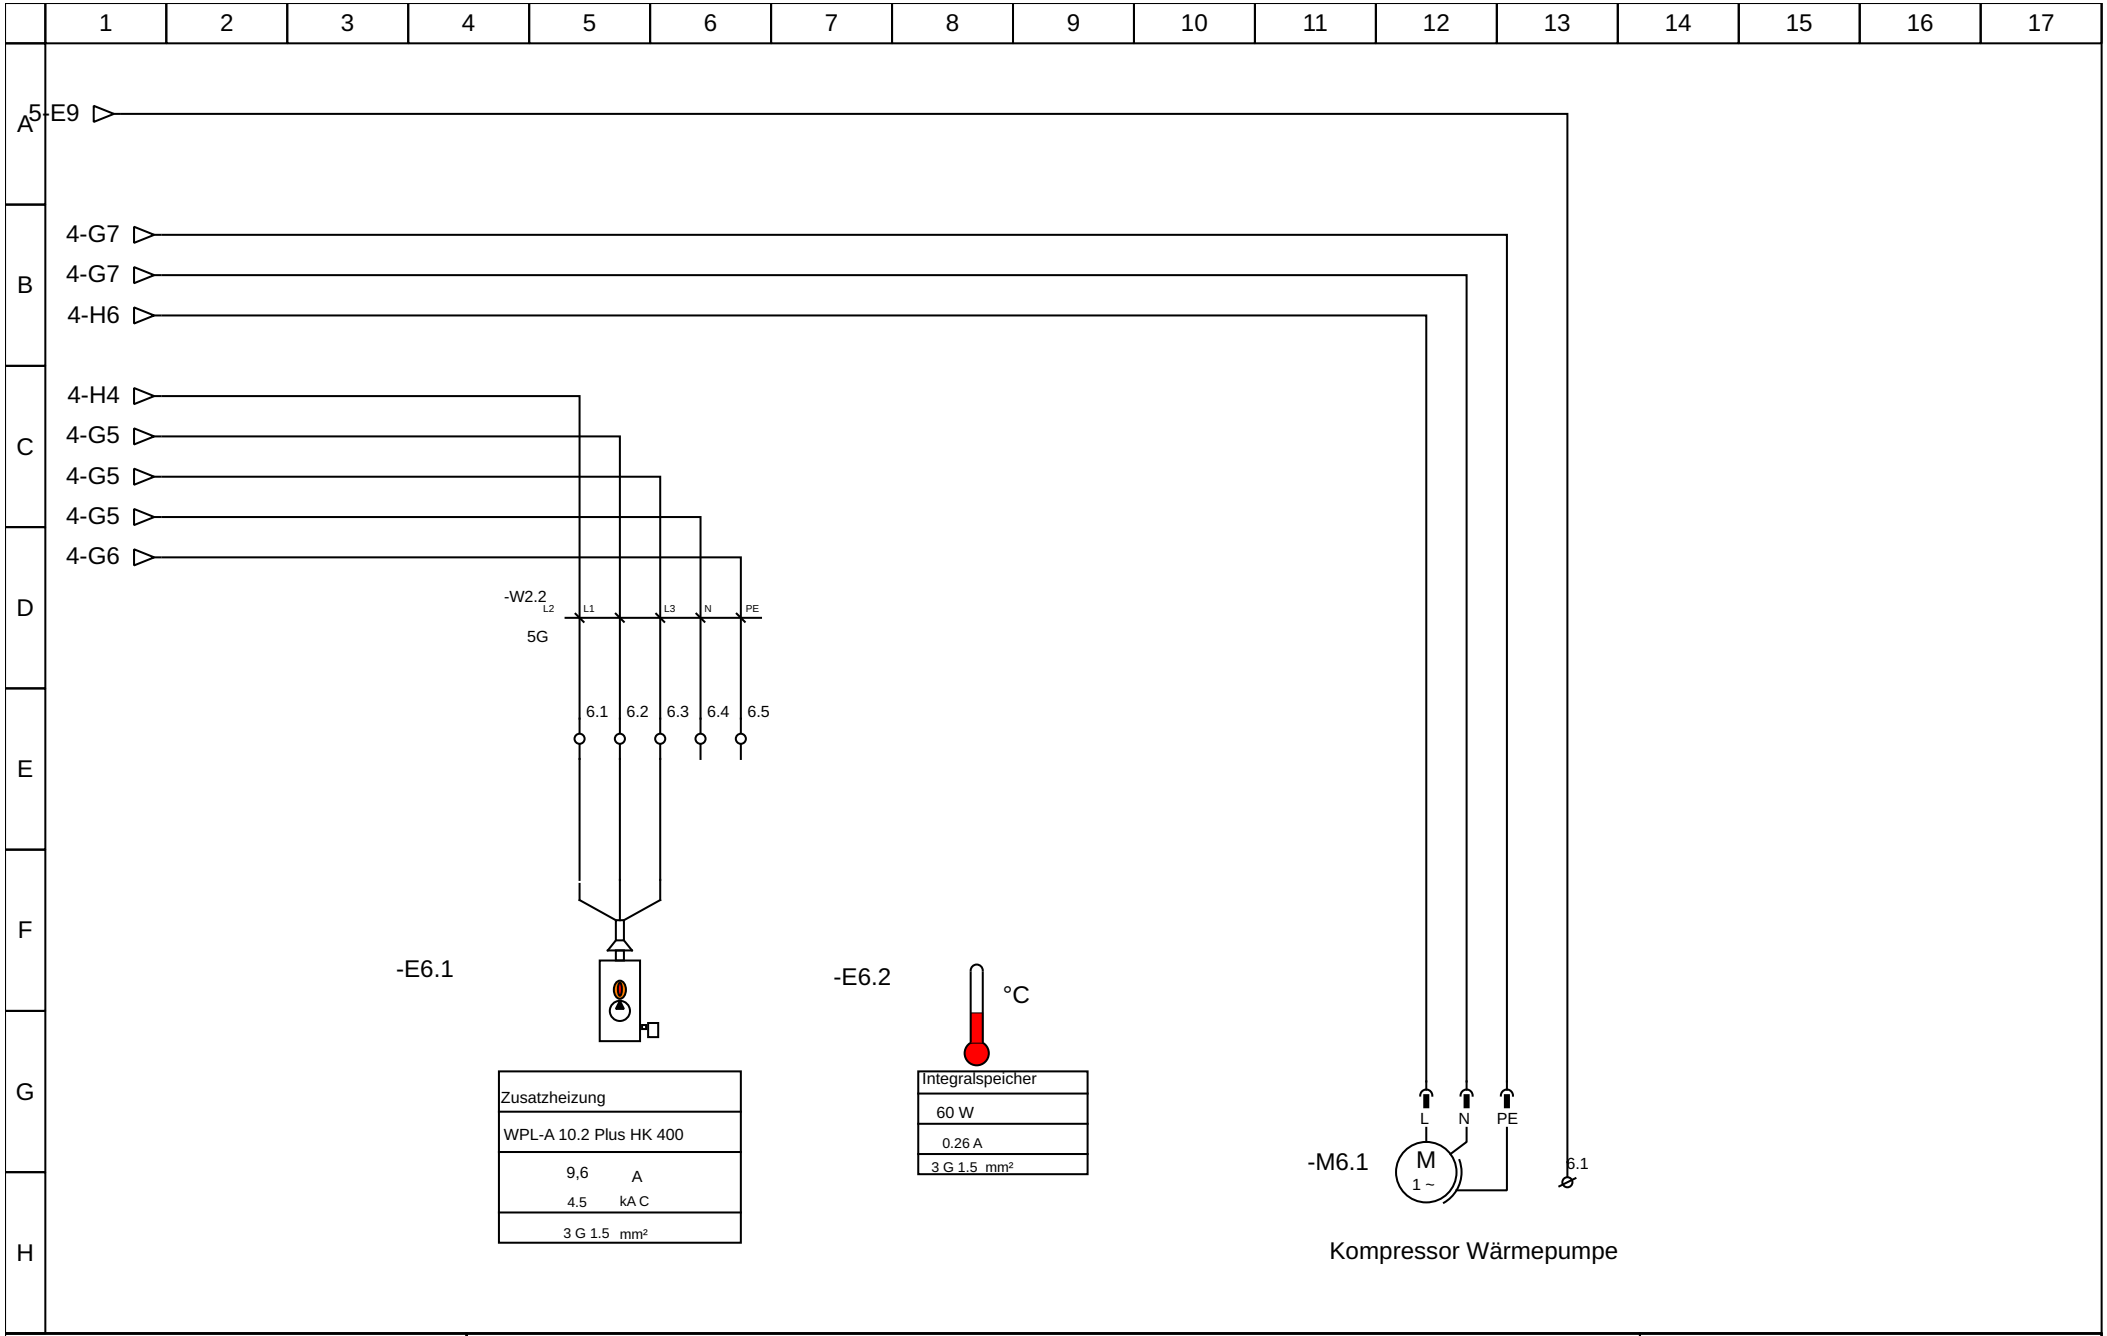



| | | |
|---|---|---|
| Autor: Entrich | Heizung | Datei: |
| Datum: 10/16/26 | | Seite: 6/39 |

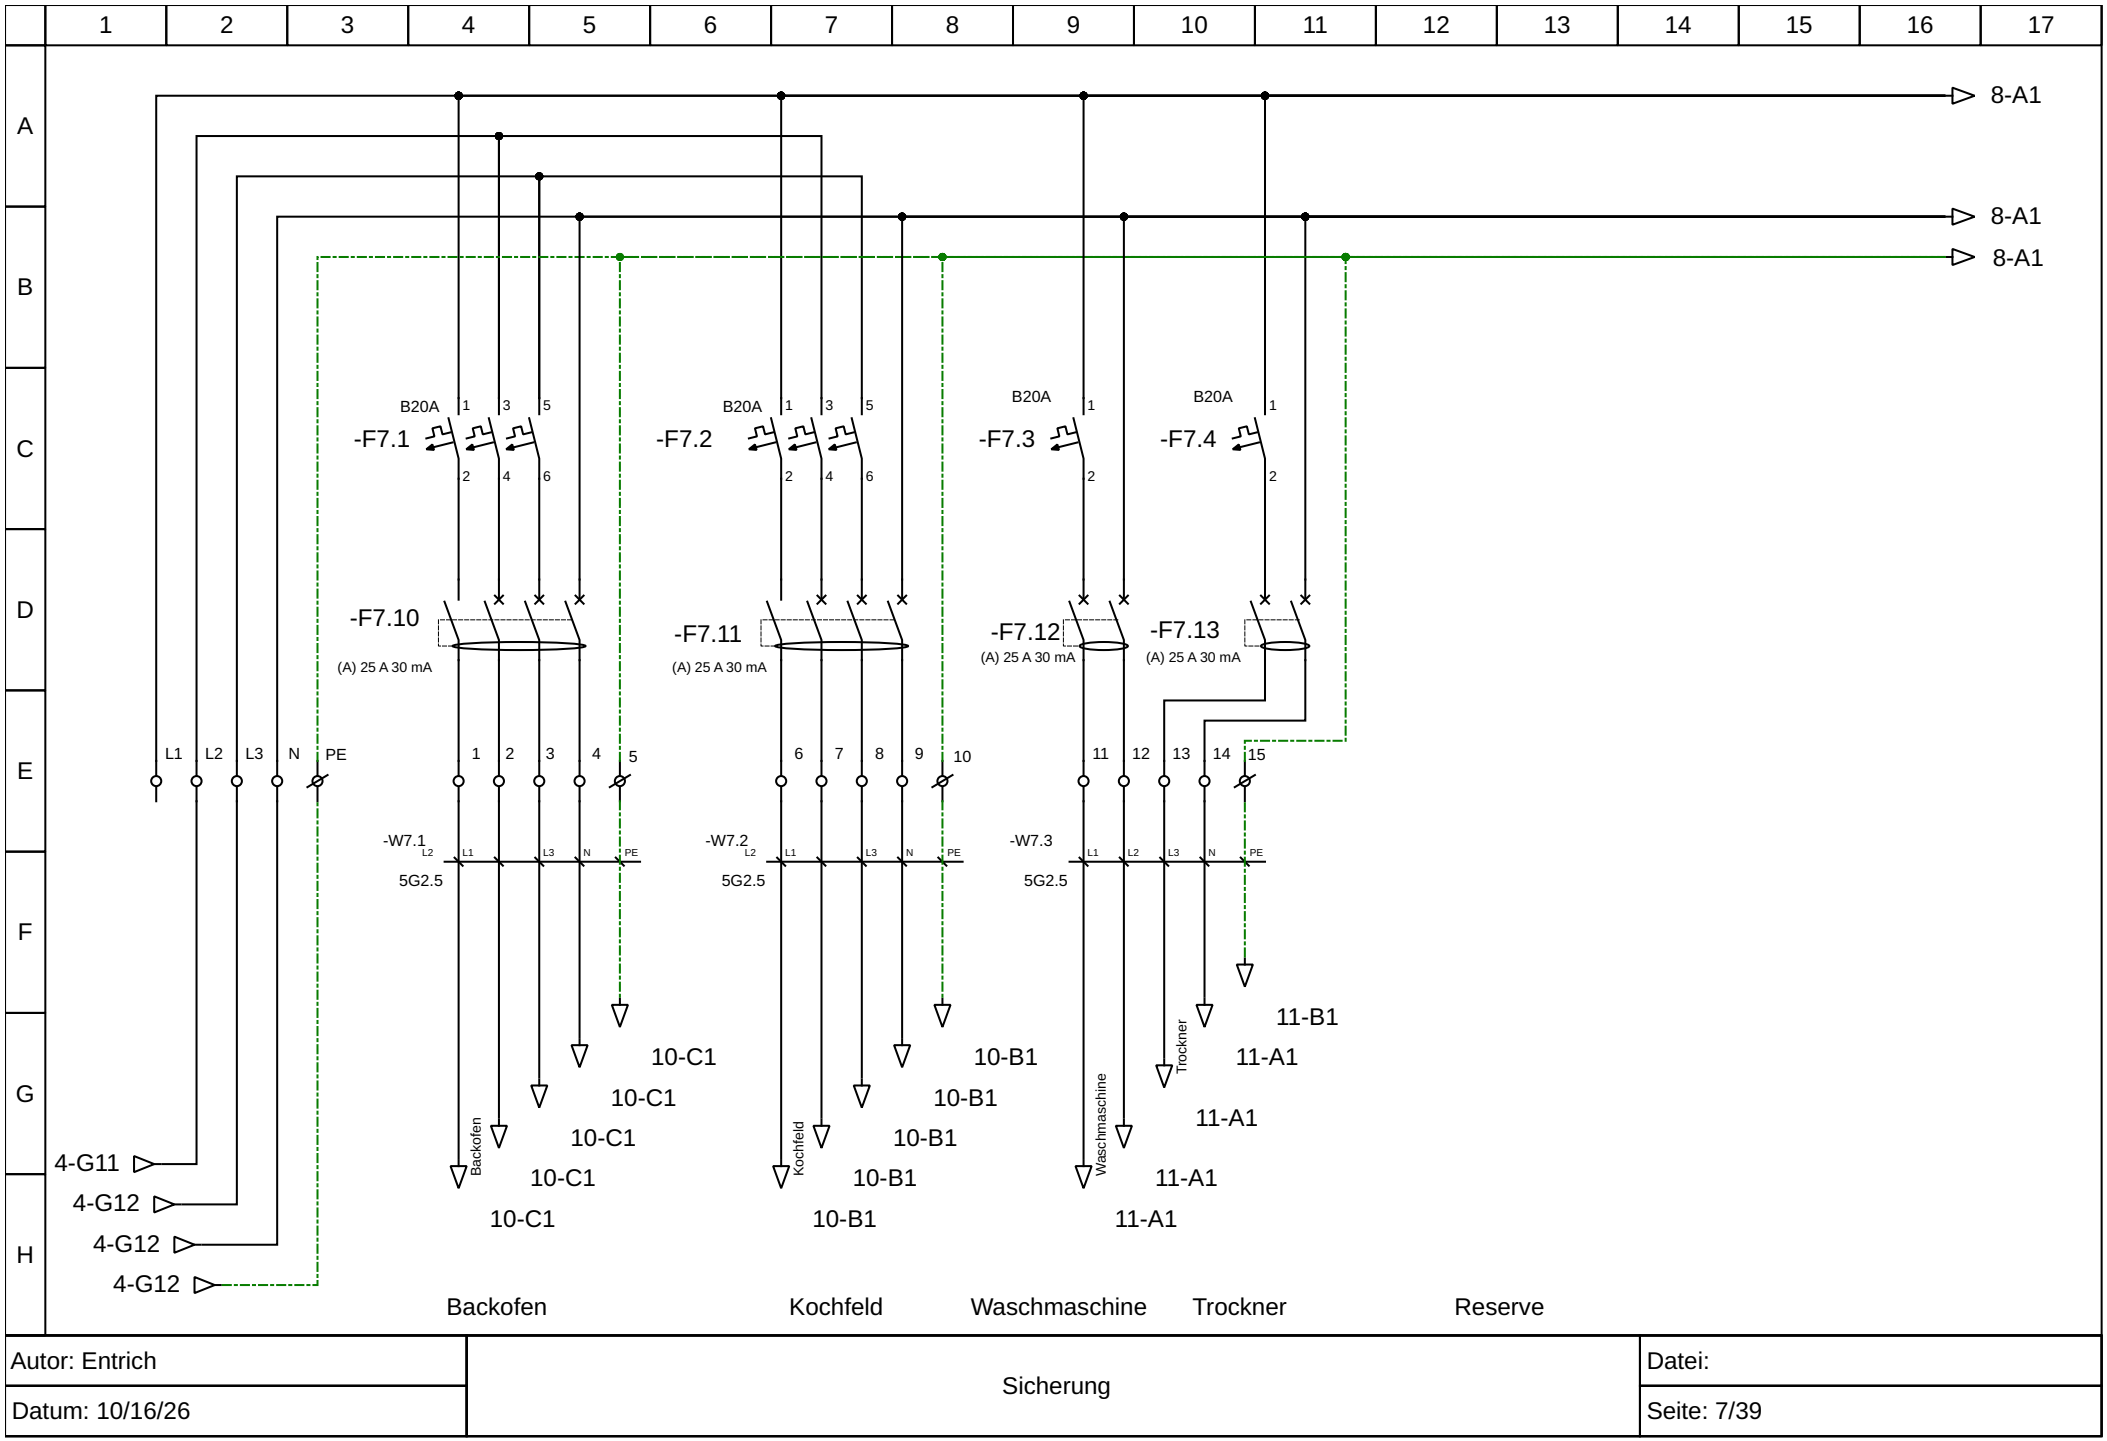



| | | |
|---|---|---|
| Autor: Entrich | Sicherung | Datei: |
| Datum: 10/16/26 | | Seite: 7/39 |

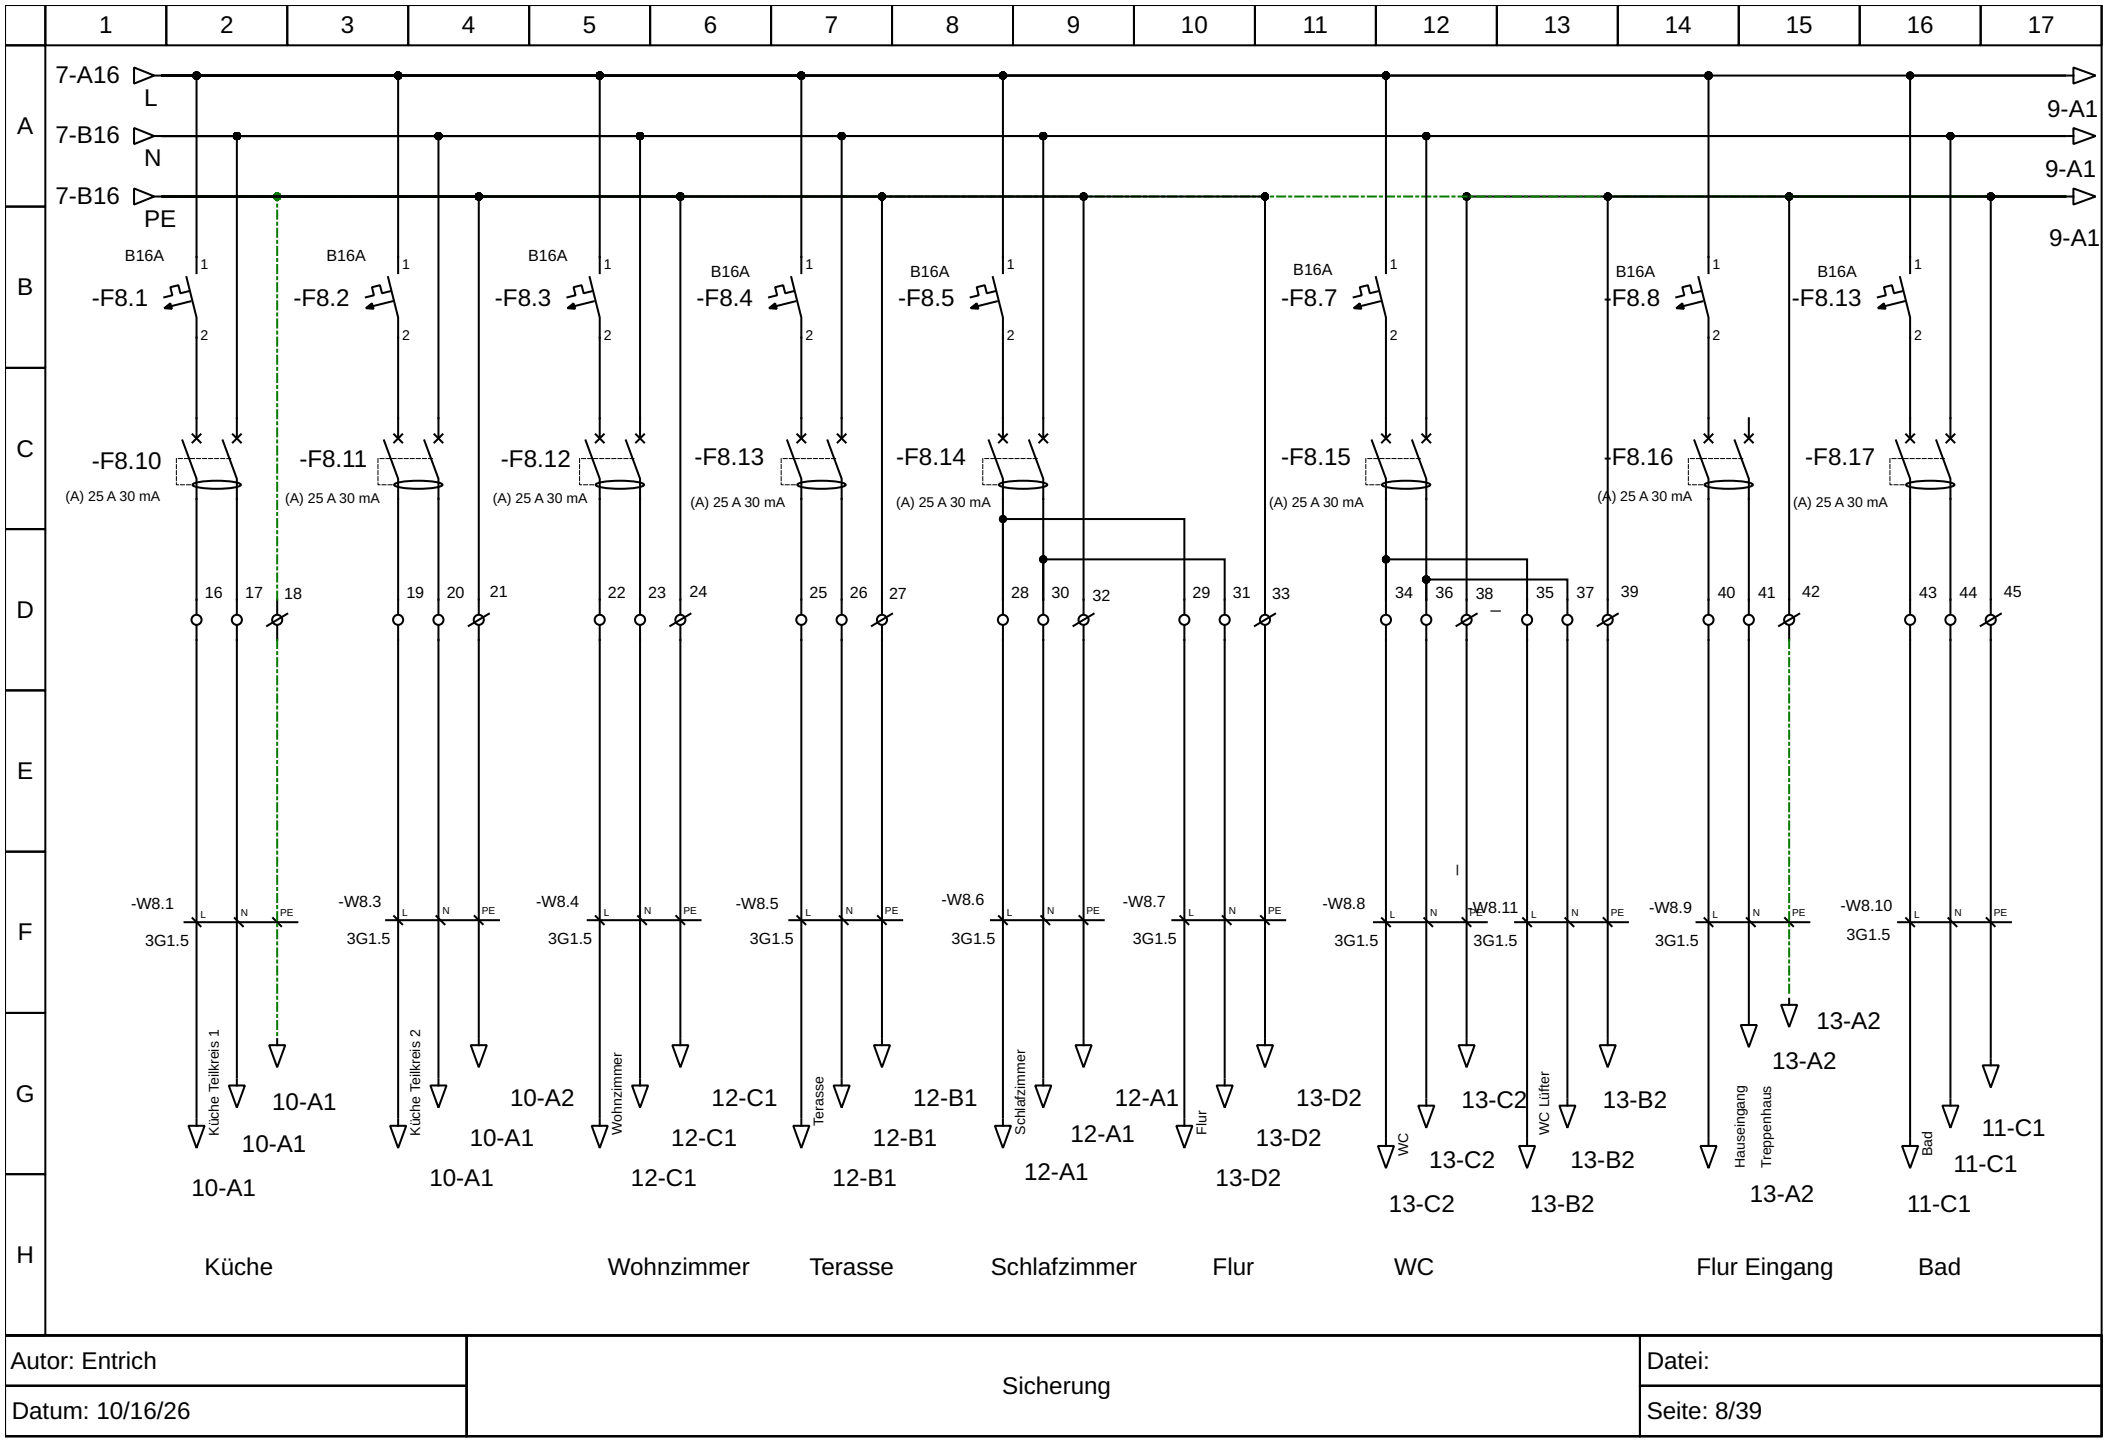



| | | |
|---|---|---|
| Autor: Entrich | Sicherung | Datei: |
| Datum: 10/16/26 | | Seite: 8/39 |

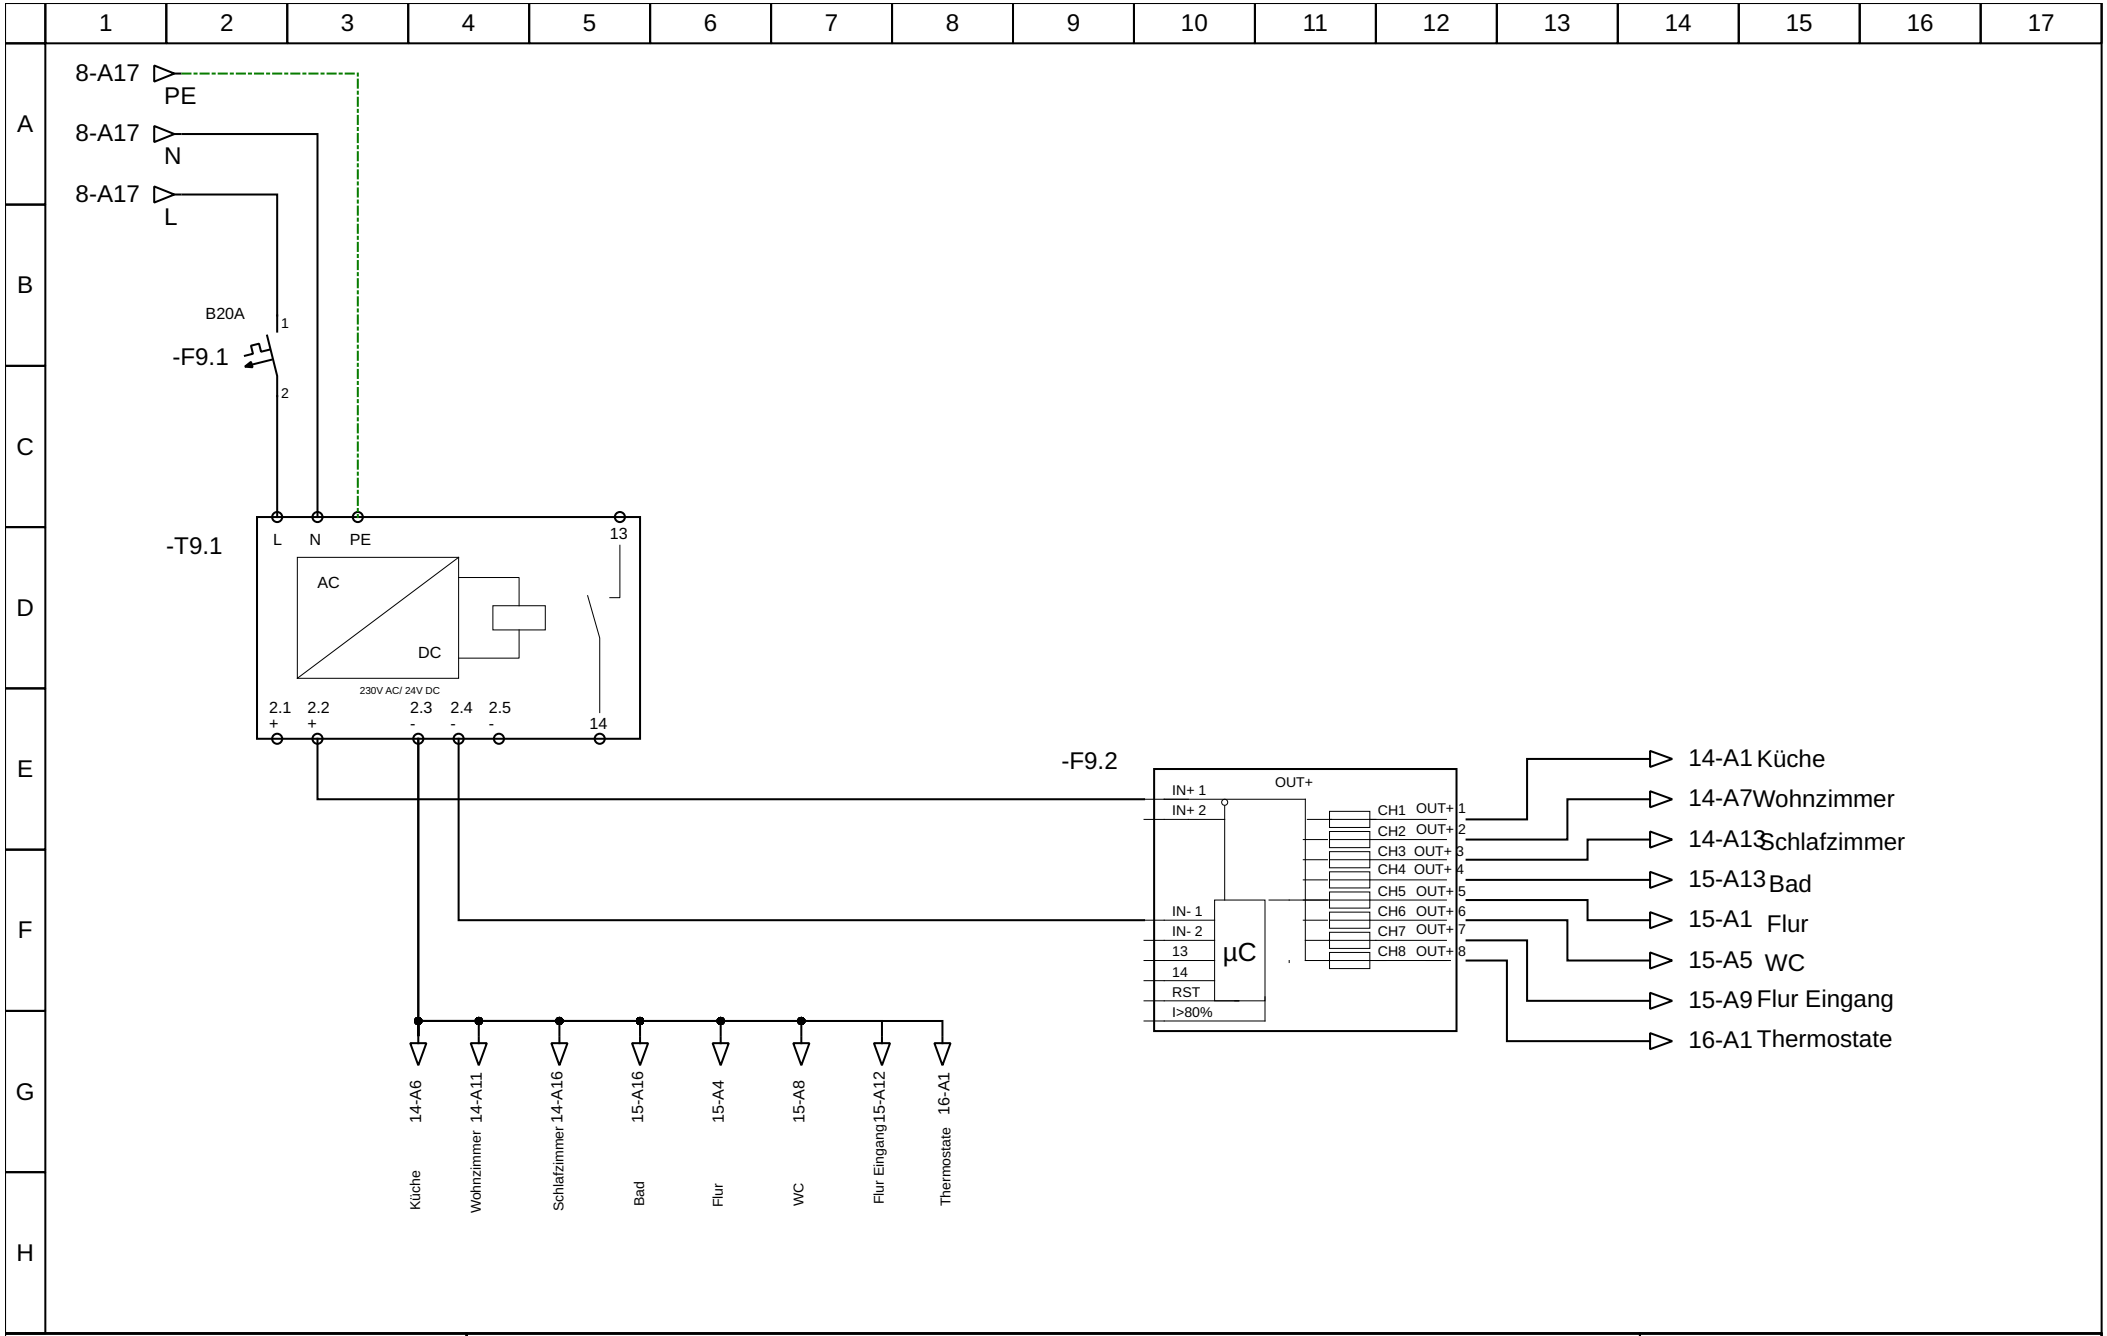



| | | |
|---|---|---|
| Autor: Entrich | Kleinspannungversorgung | Datei: |
| Datum: 10/16/26 | | Seite: 9/39 |

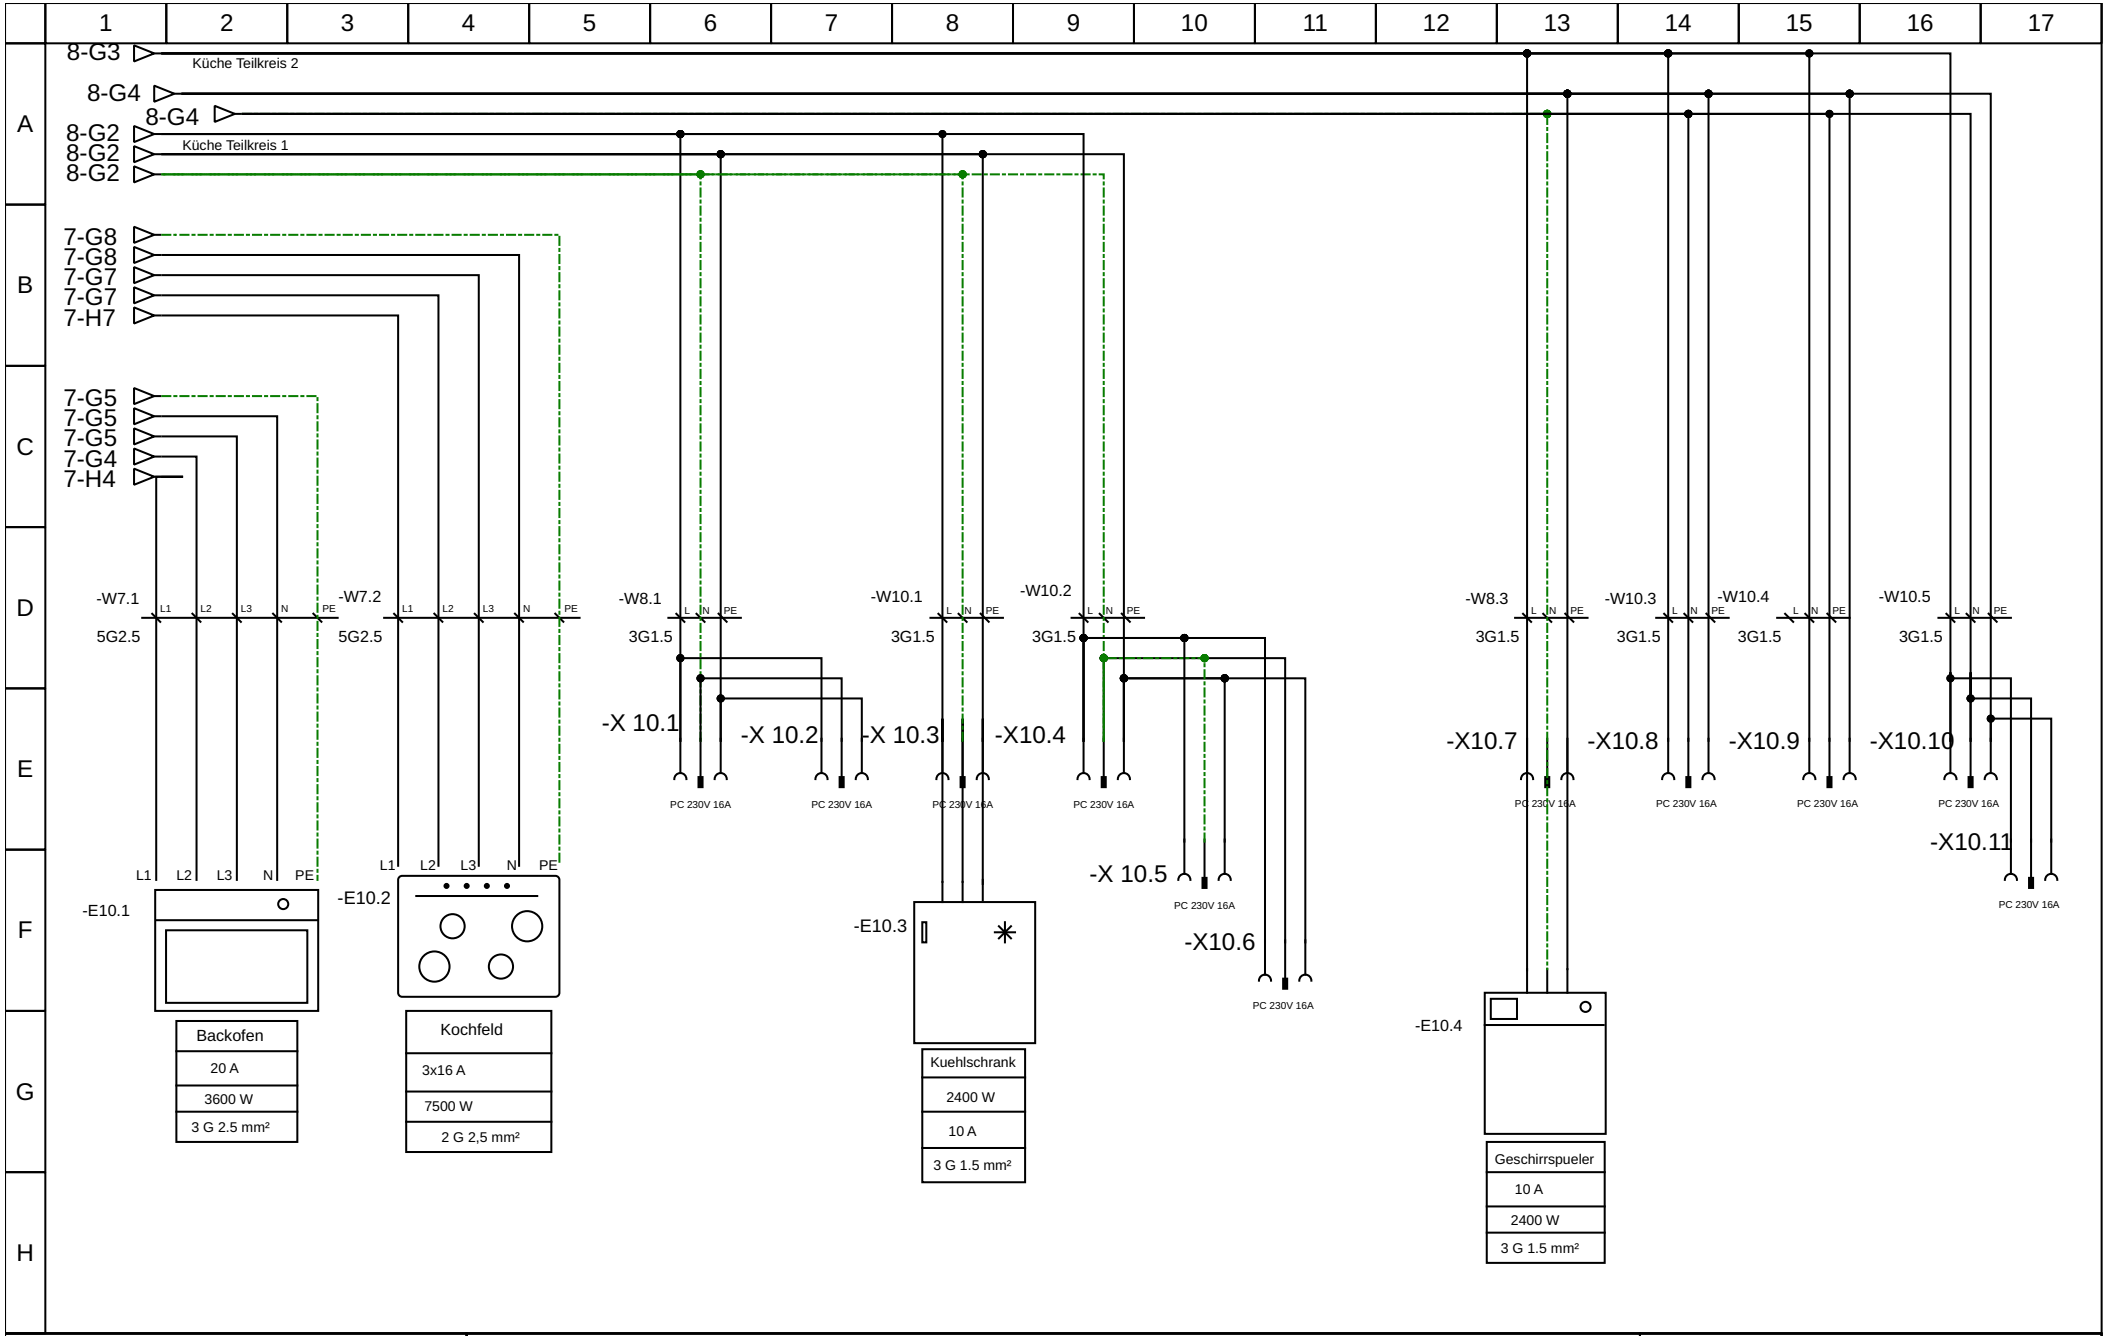



| | | |
|---|---|---|
| Autor: Entrich | Hauptstrom Küche | Datei: |
| Datum: 10/16/26 | | Seite: 10/39 |

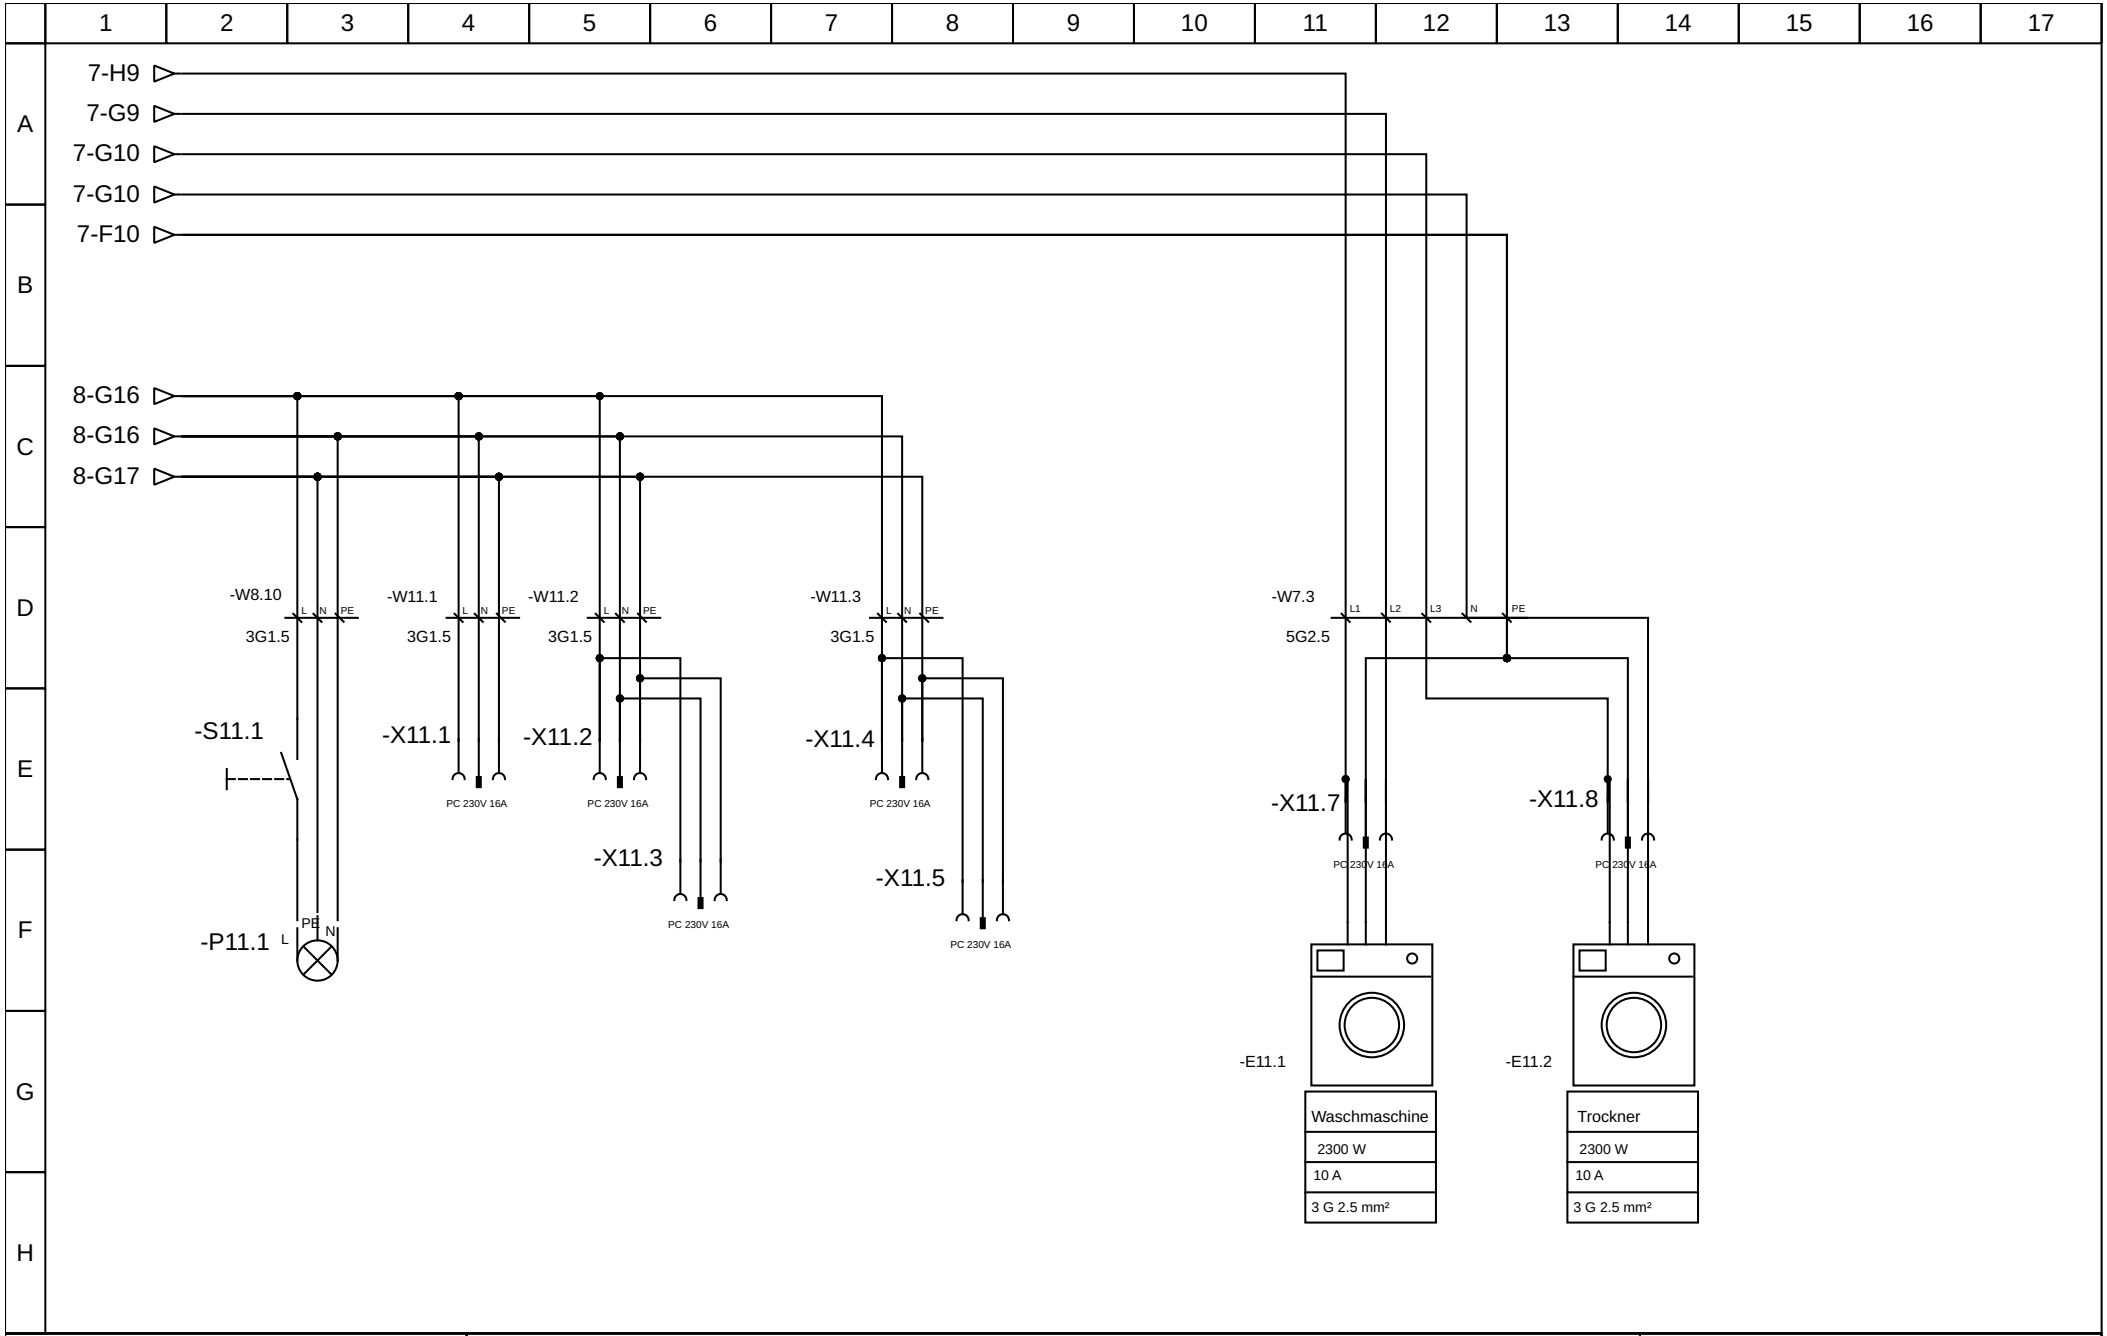



| | | |
|---|---|---|
| Autor: Entrich | Hauptstrom Bad | Datei: |
| Datum: 10/16/26 | | Seite: 11/39 |

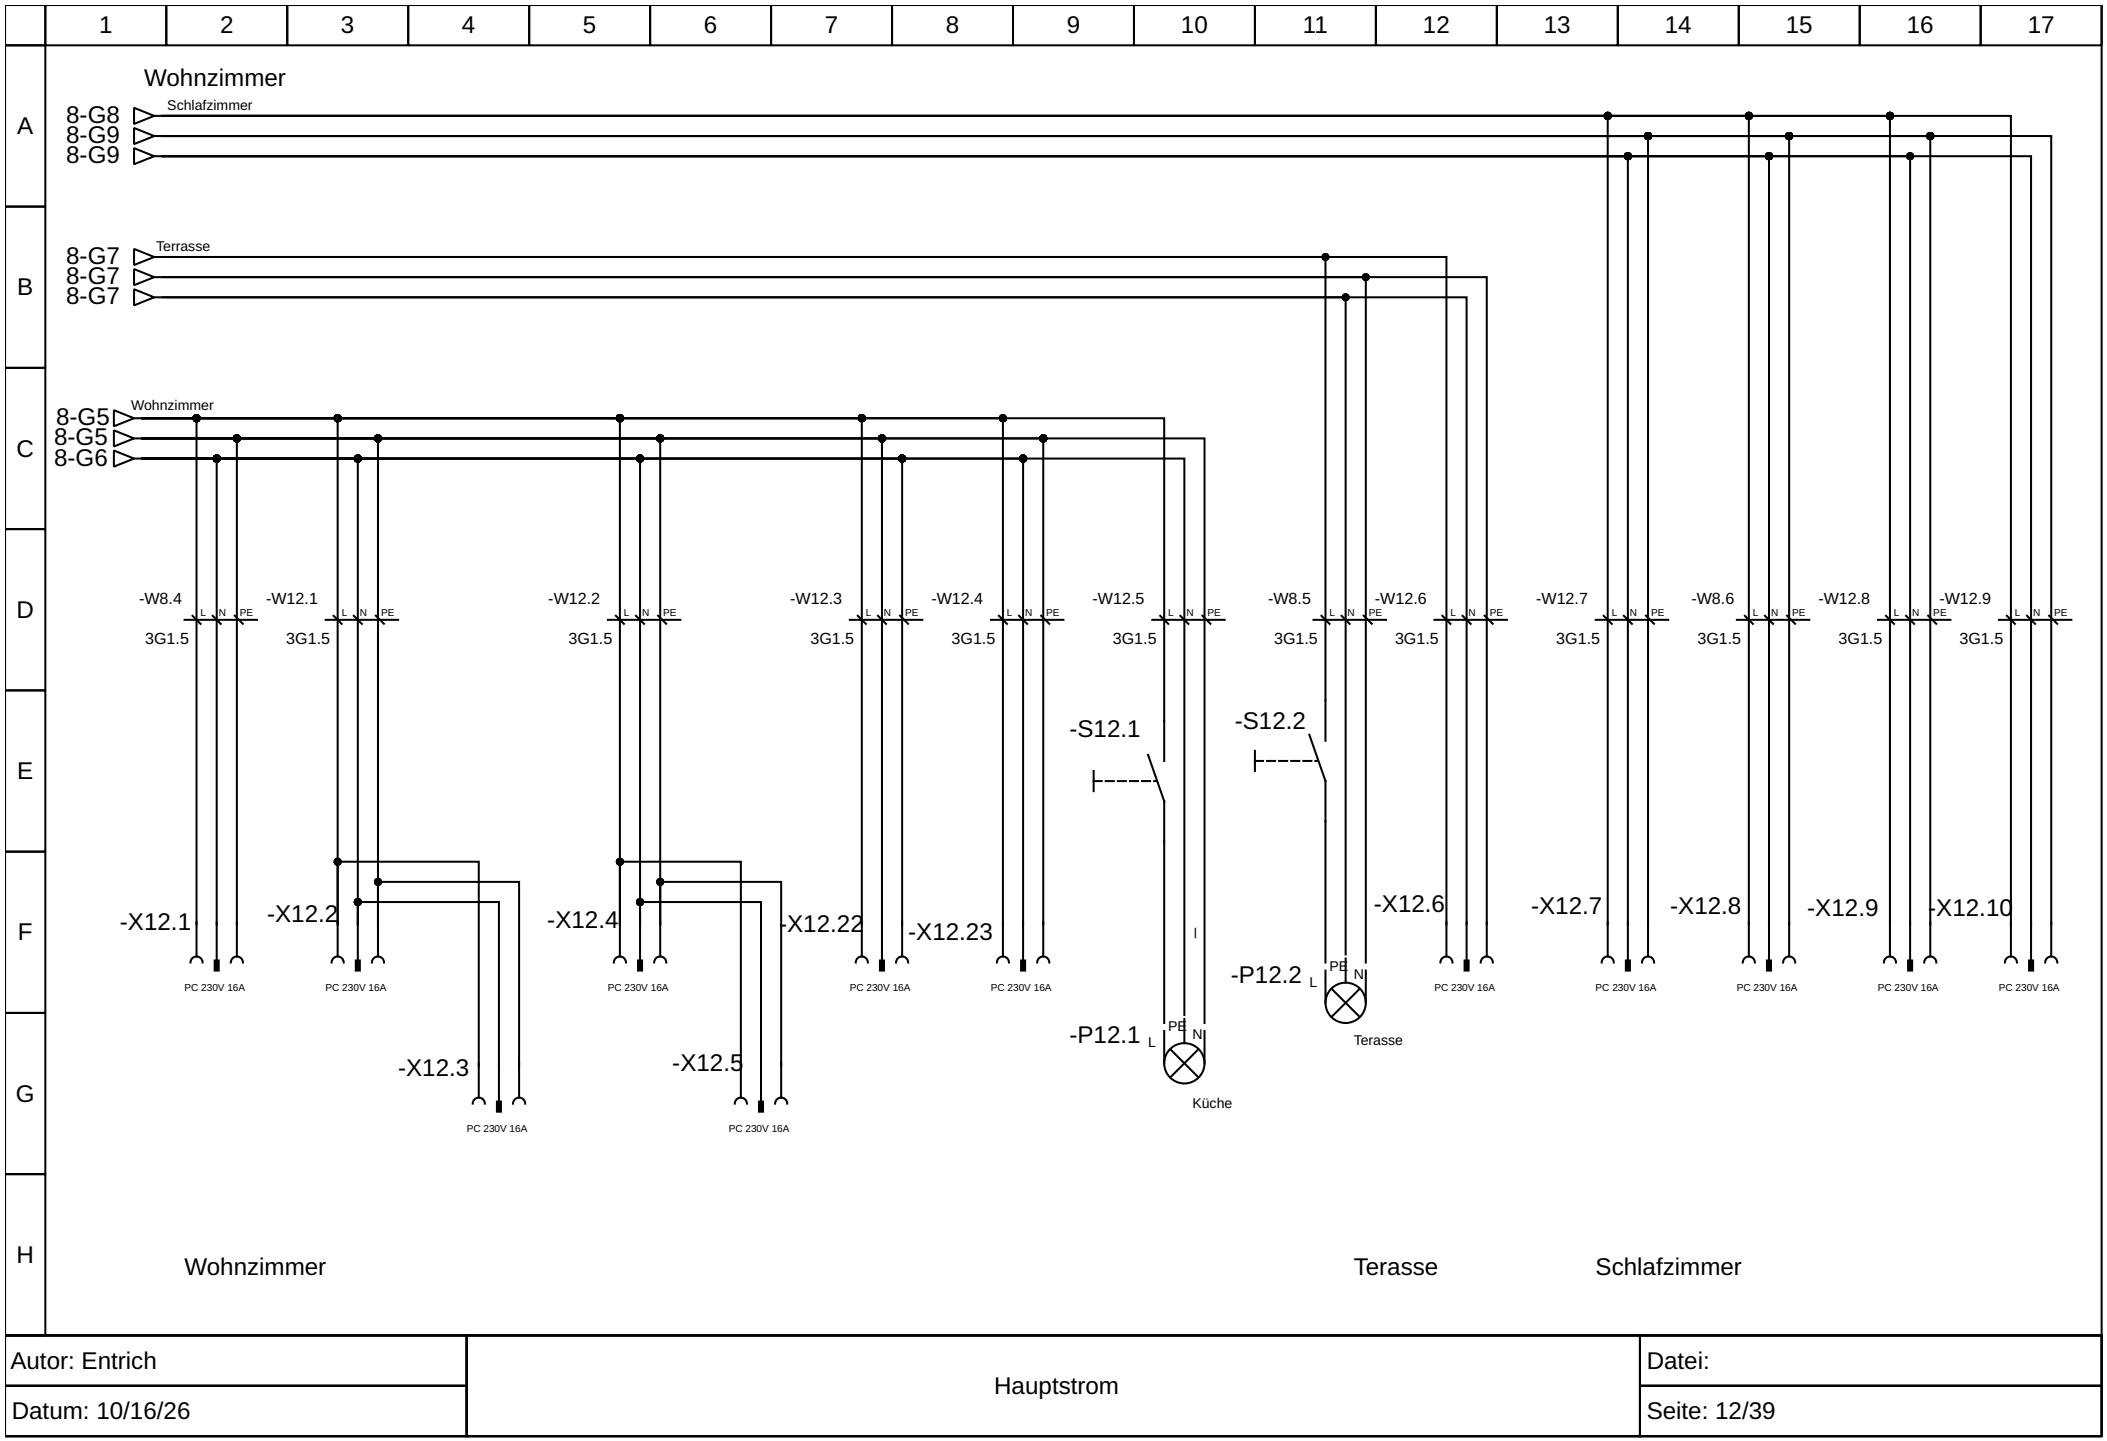



| | | |
|---|---|---|
| Autor: Entrich | Hauptstrom | Datei: |
| Datum: 10/16/26 | | Seite: 12/39 |

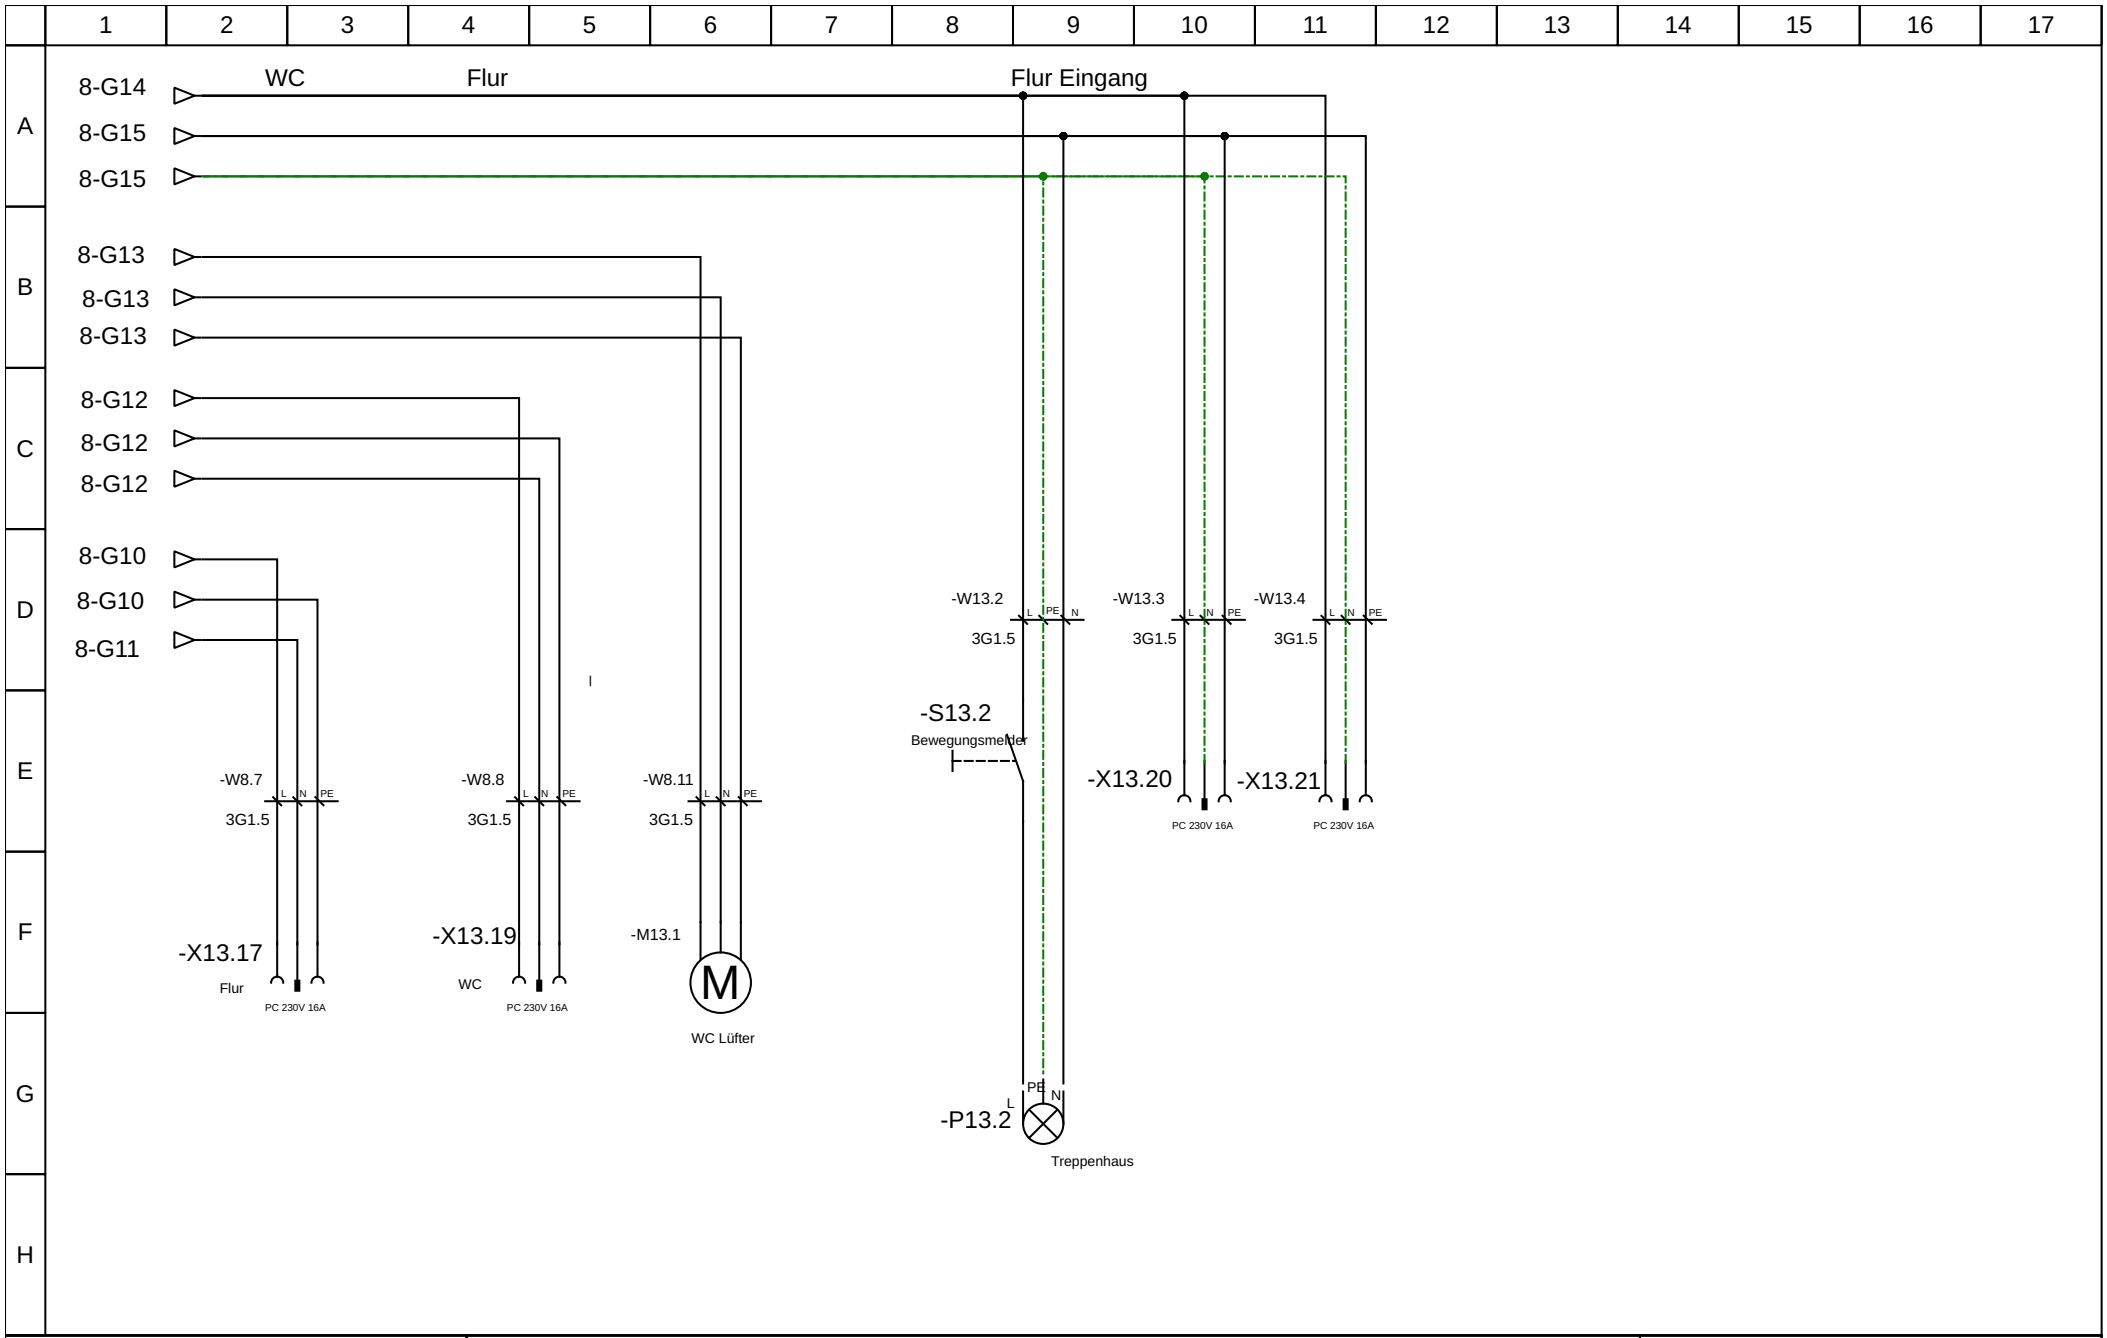



| | |
|---|---|
| Autor: Entrich | Hauptstrom |
| Datum: 10/16/26 | Datei: |
| | Seite: 13/39 |

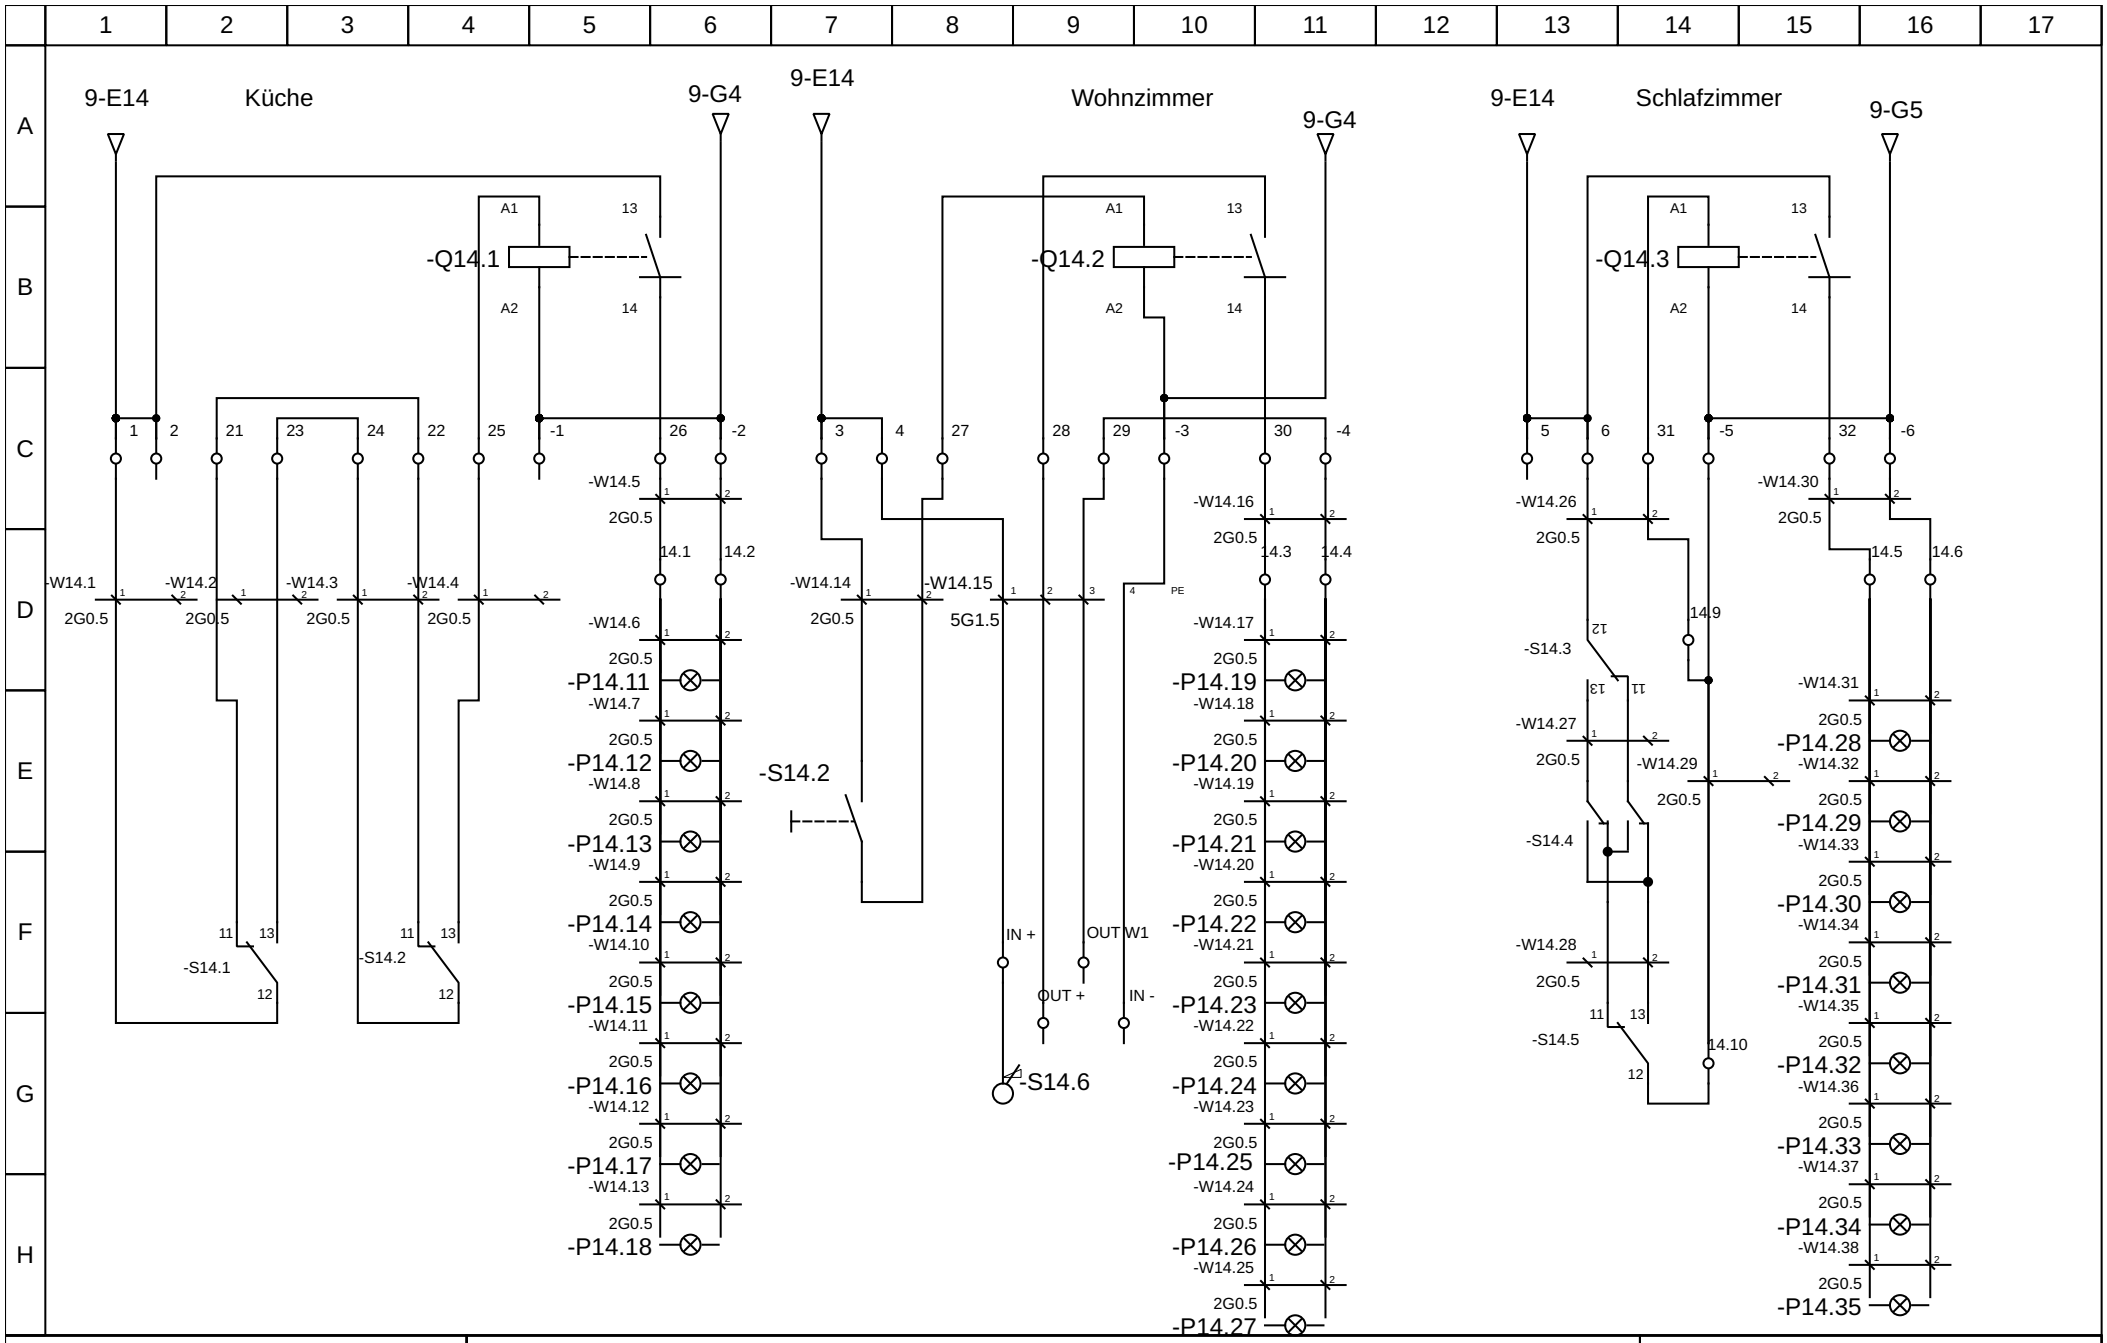



| | | |
|---|---|---|
| Autor: Entrich | Kleinspannung | Datei: |
| Datum: 10/16/26 | | Seite: 14/39 |

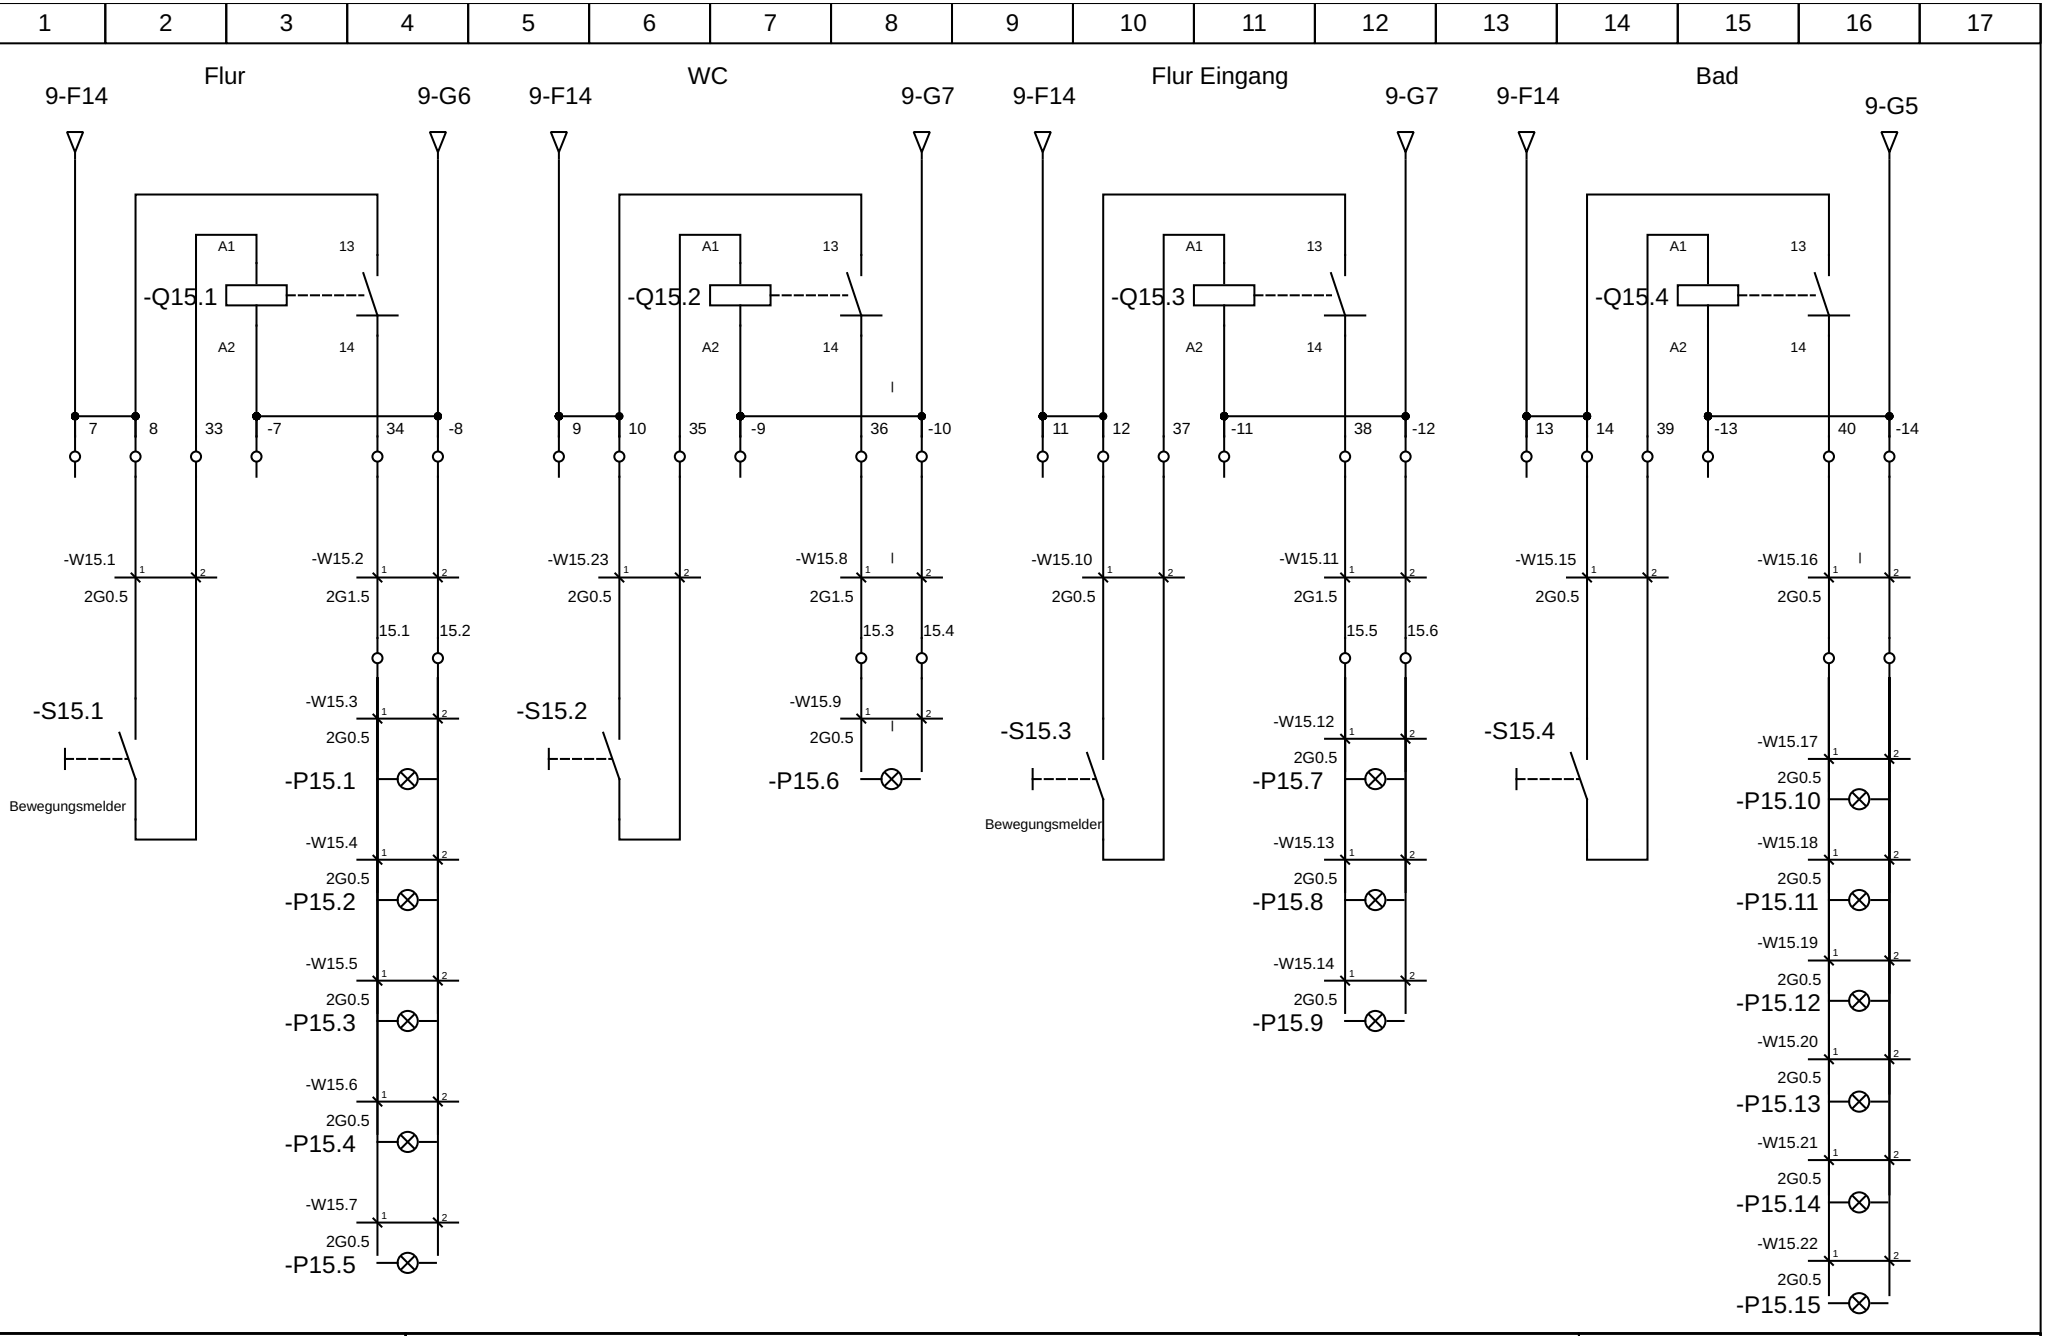



| | | |
|---|---|---|
| Autor: Entrich | Kleinspannung | Datei: |
| Datum: 10/16/26 | | Seite: 15/39 |

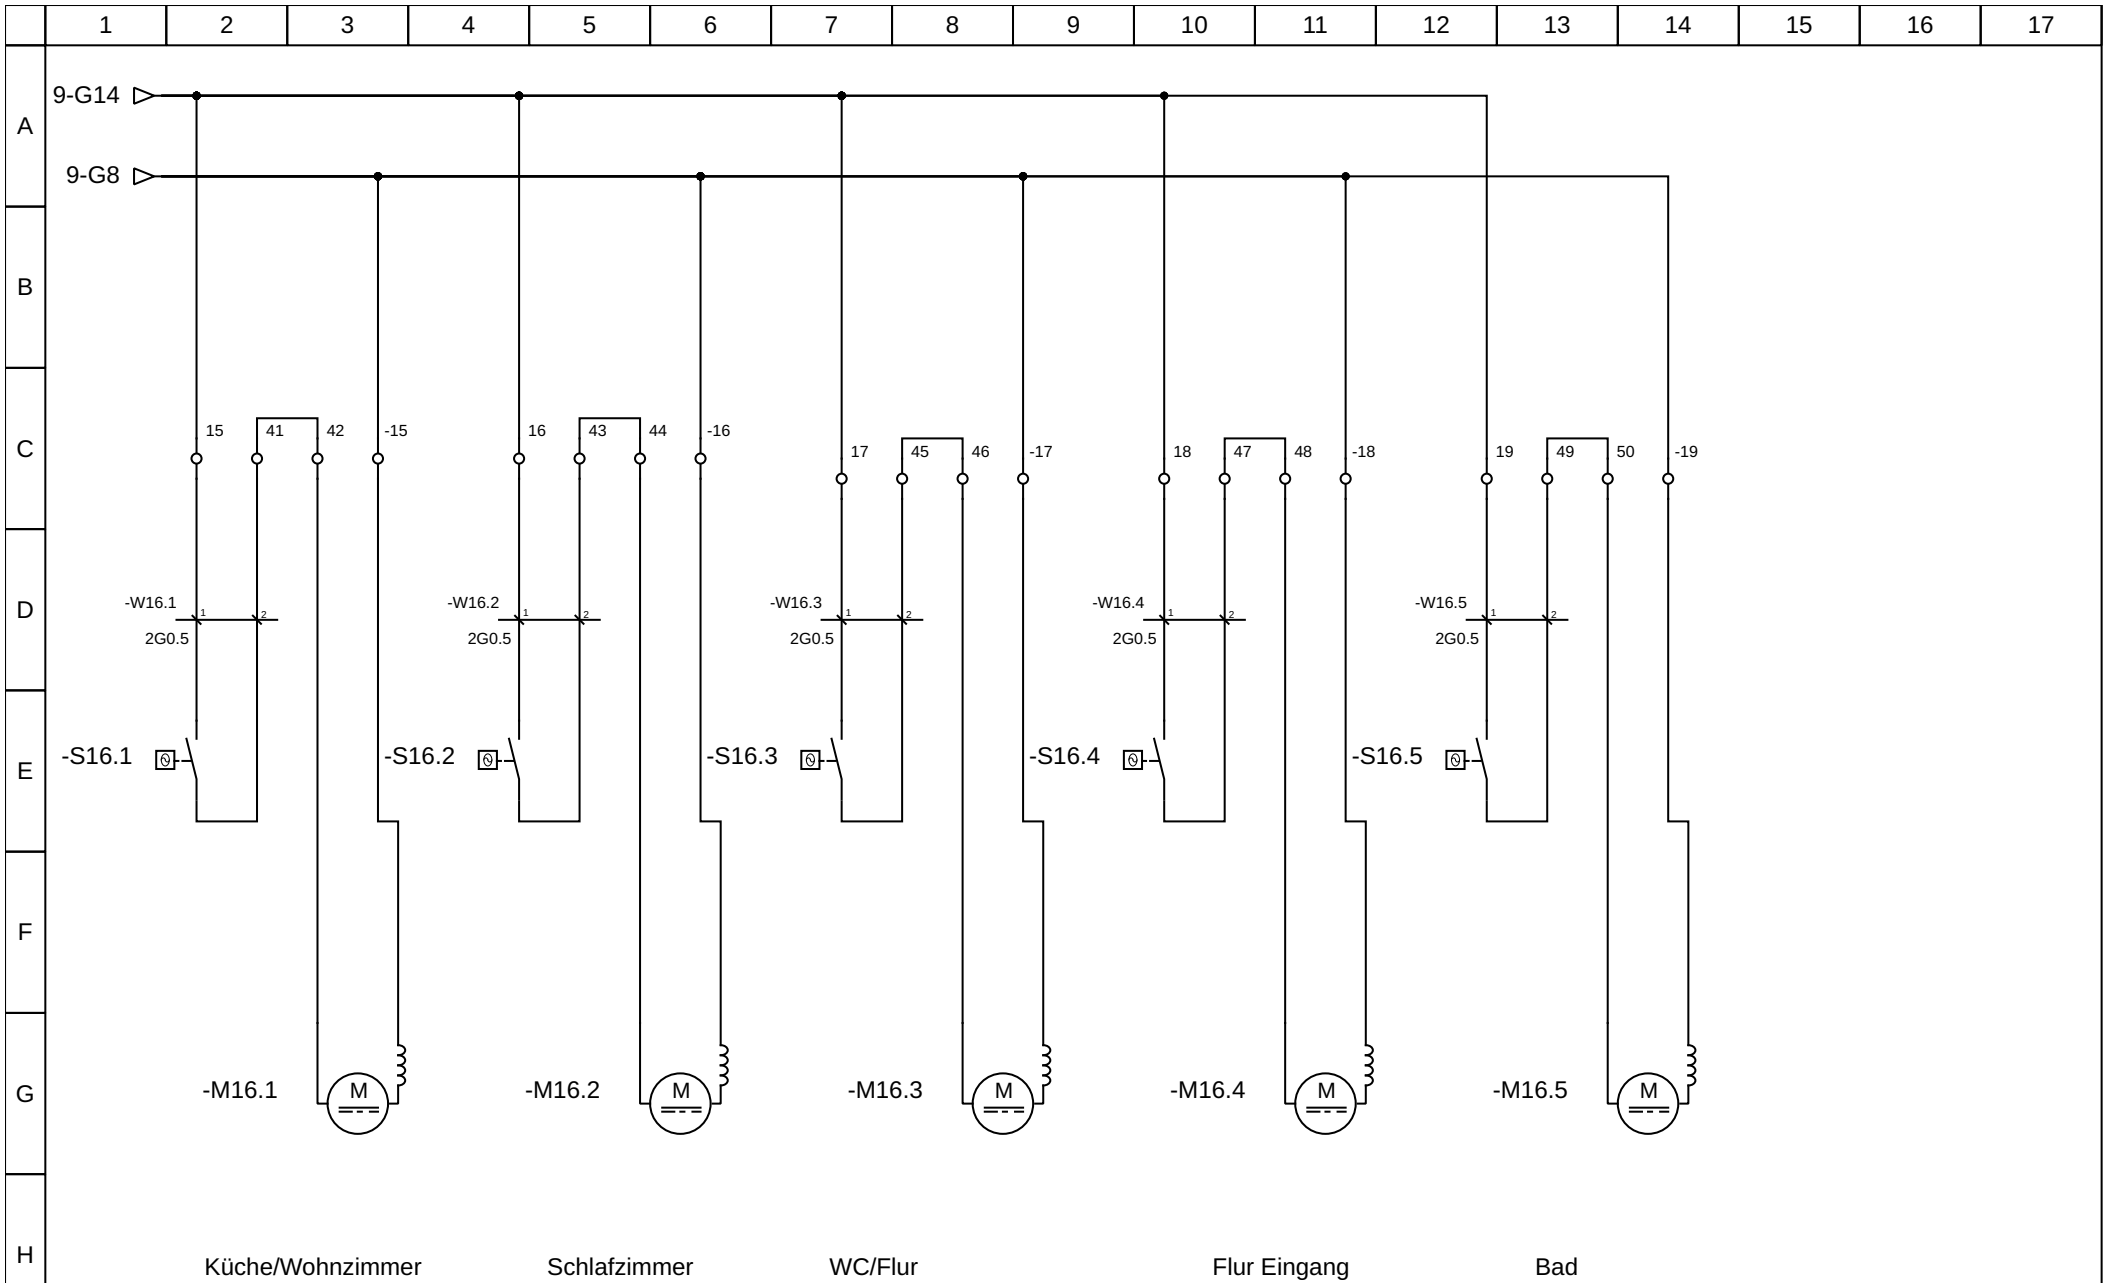



| | | |
|---|---|---|
| Autor: Entrich | Thermostate | Datei: |
| Datum: 10/16/26 | | Seite: 16/39 |

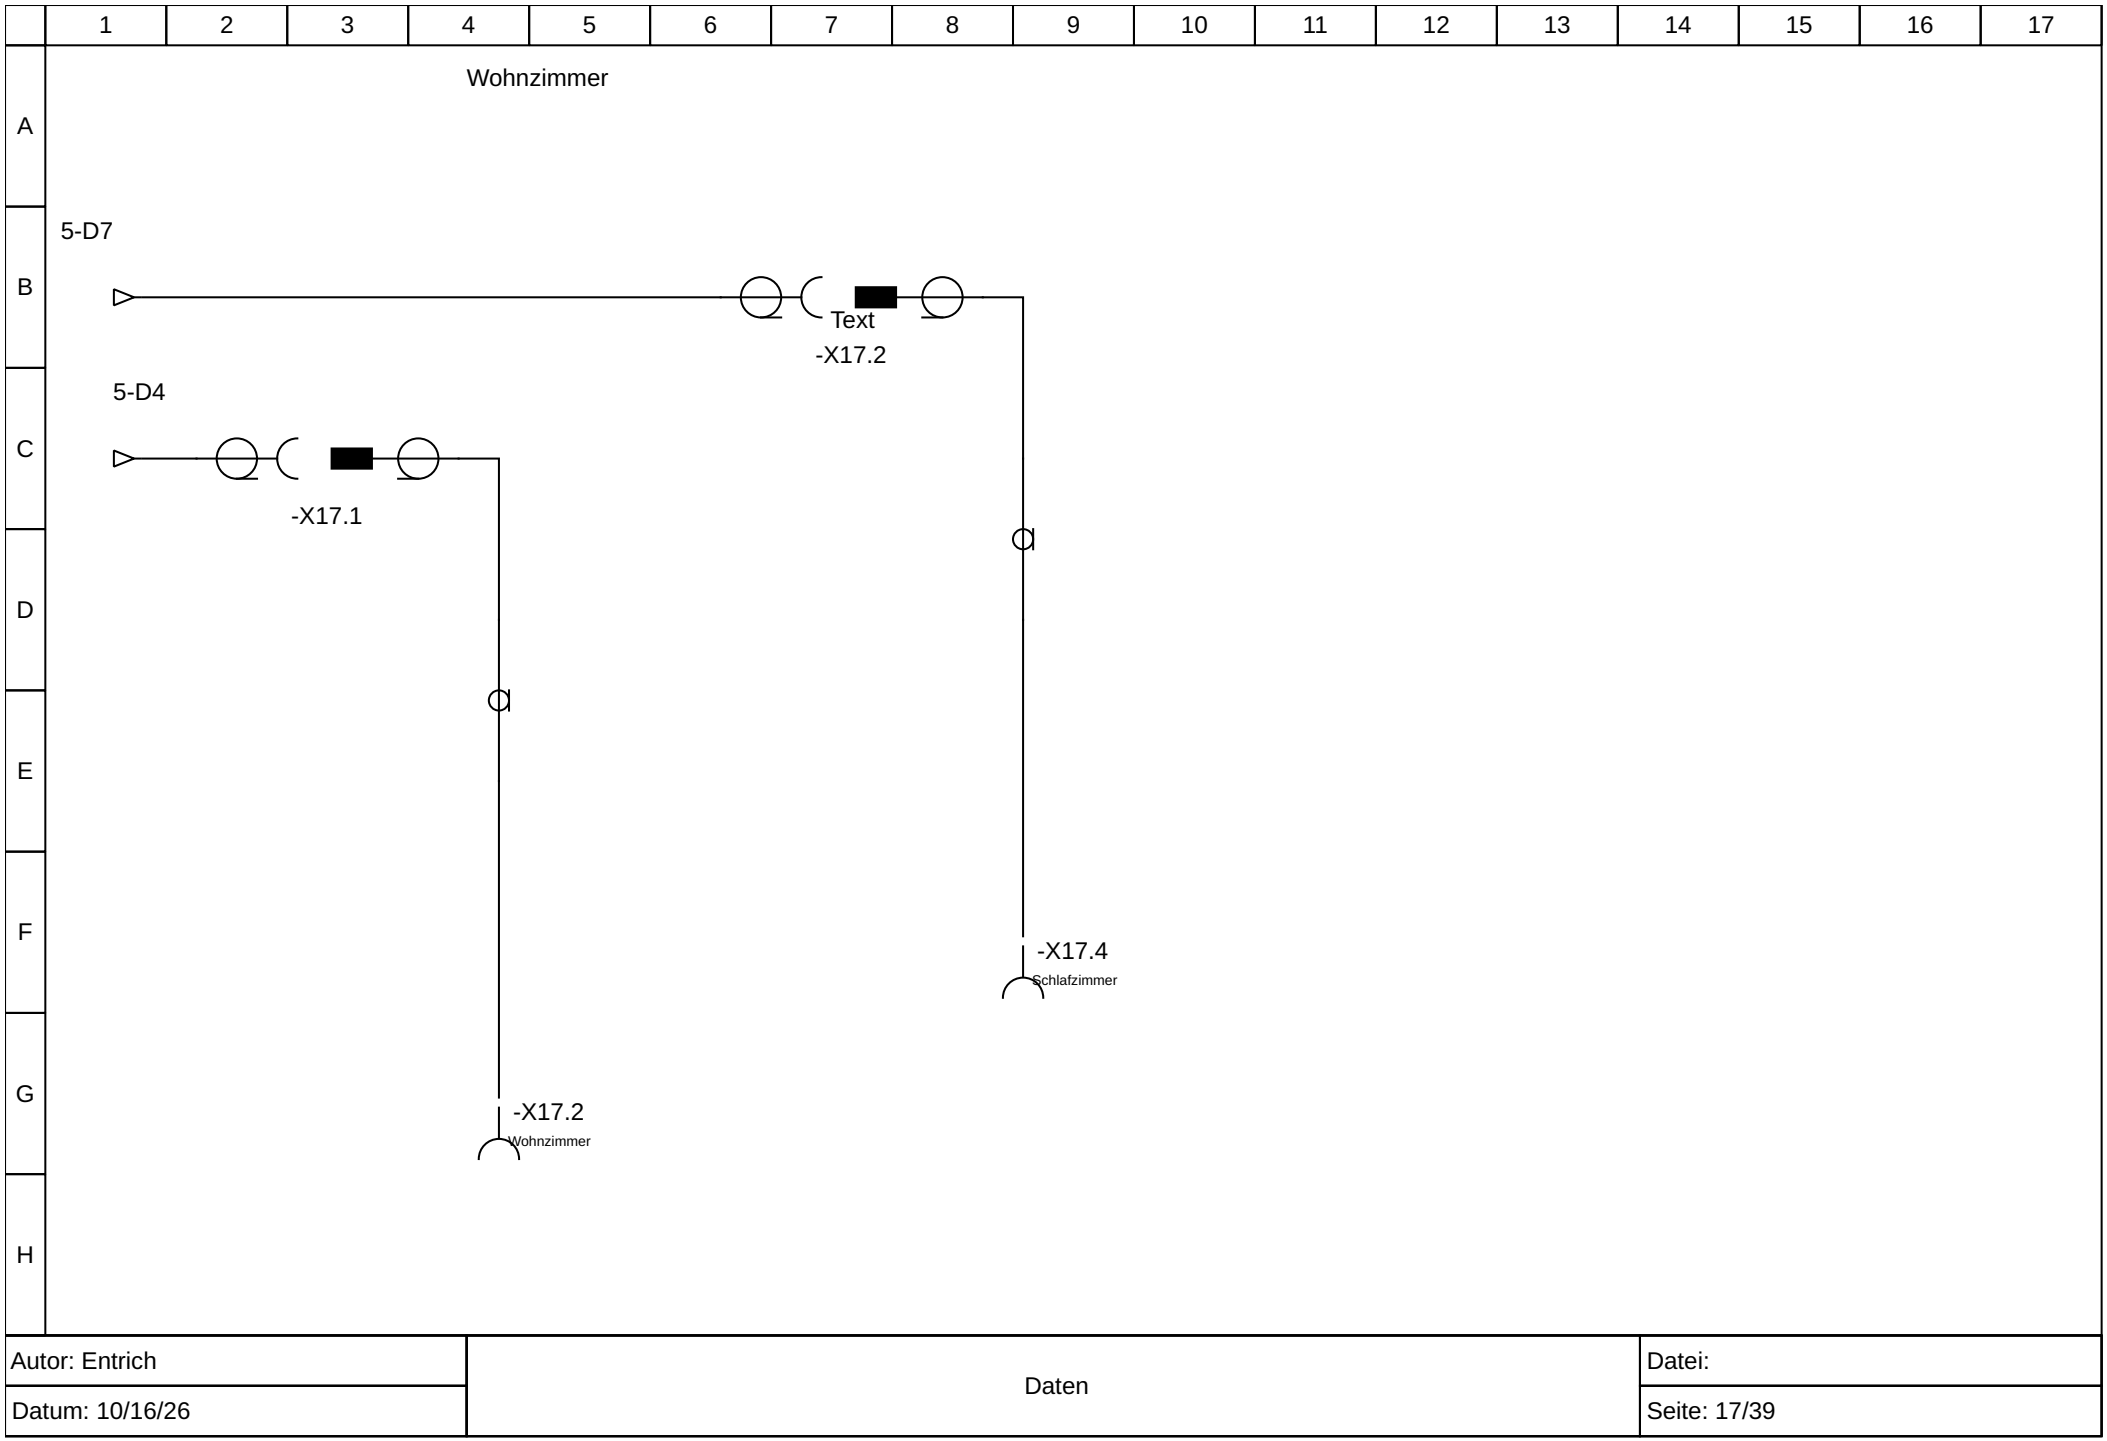



| | | |
|---|---|---|
| Autor: Entrich | Daten | Datei: |
| Datum: 10/16/26 | | Seite: 17/39 |

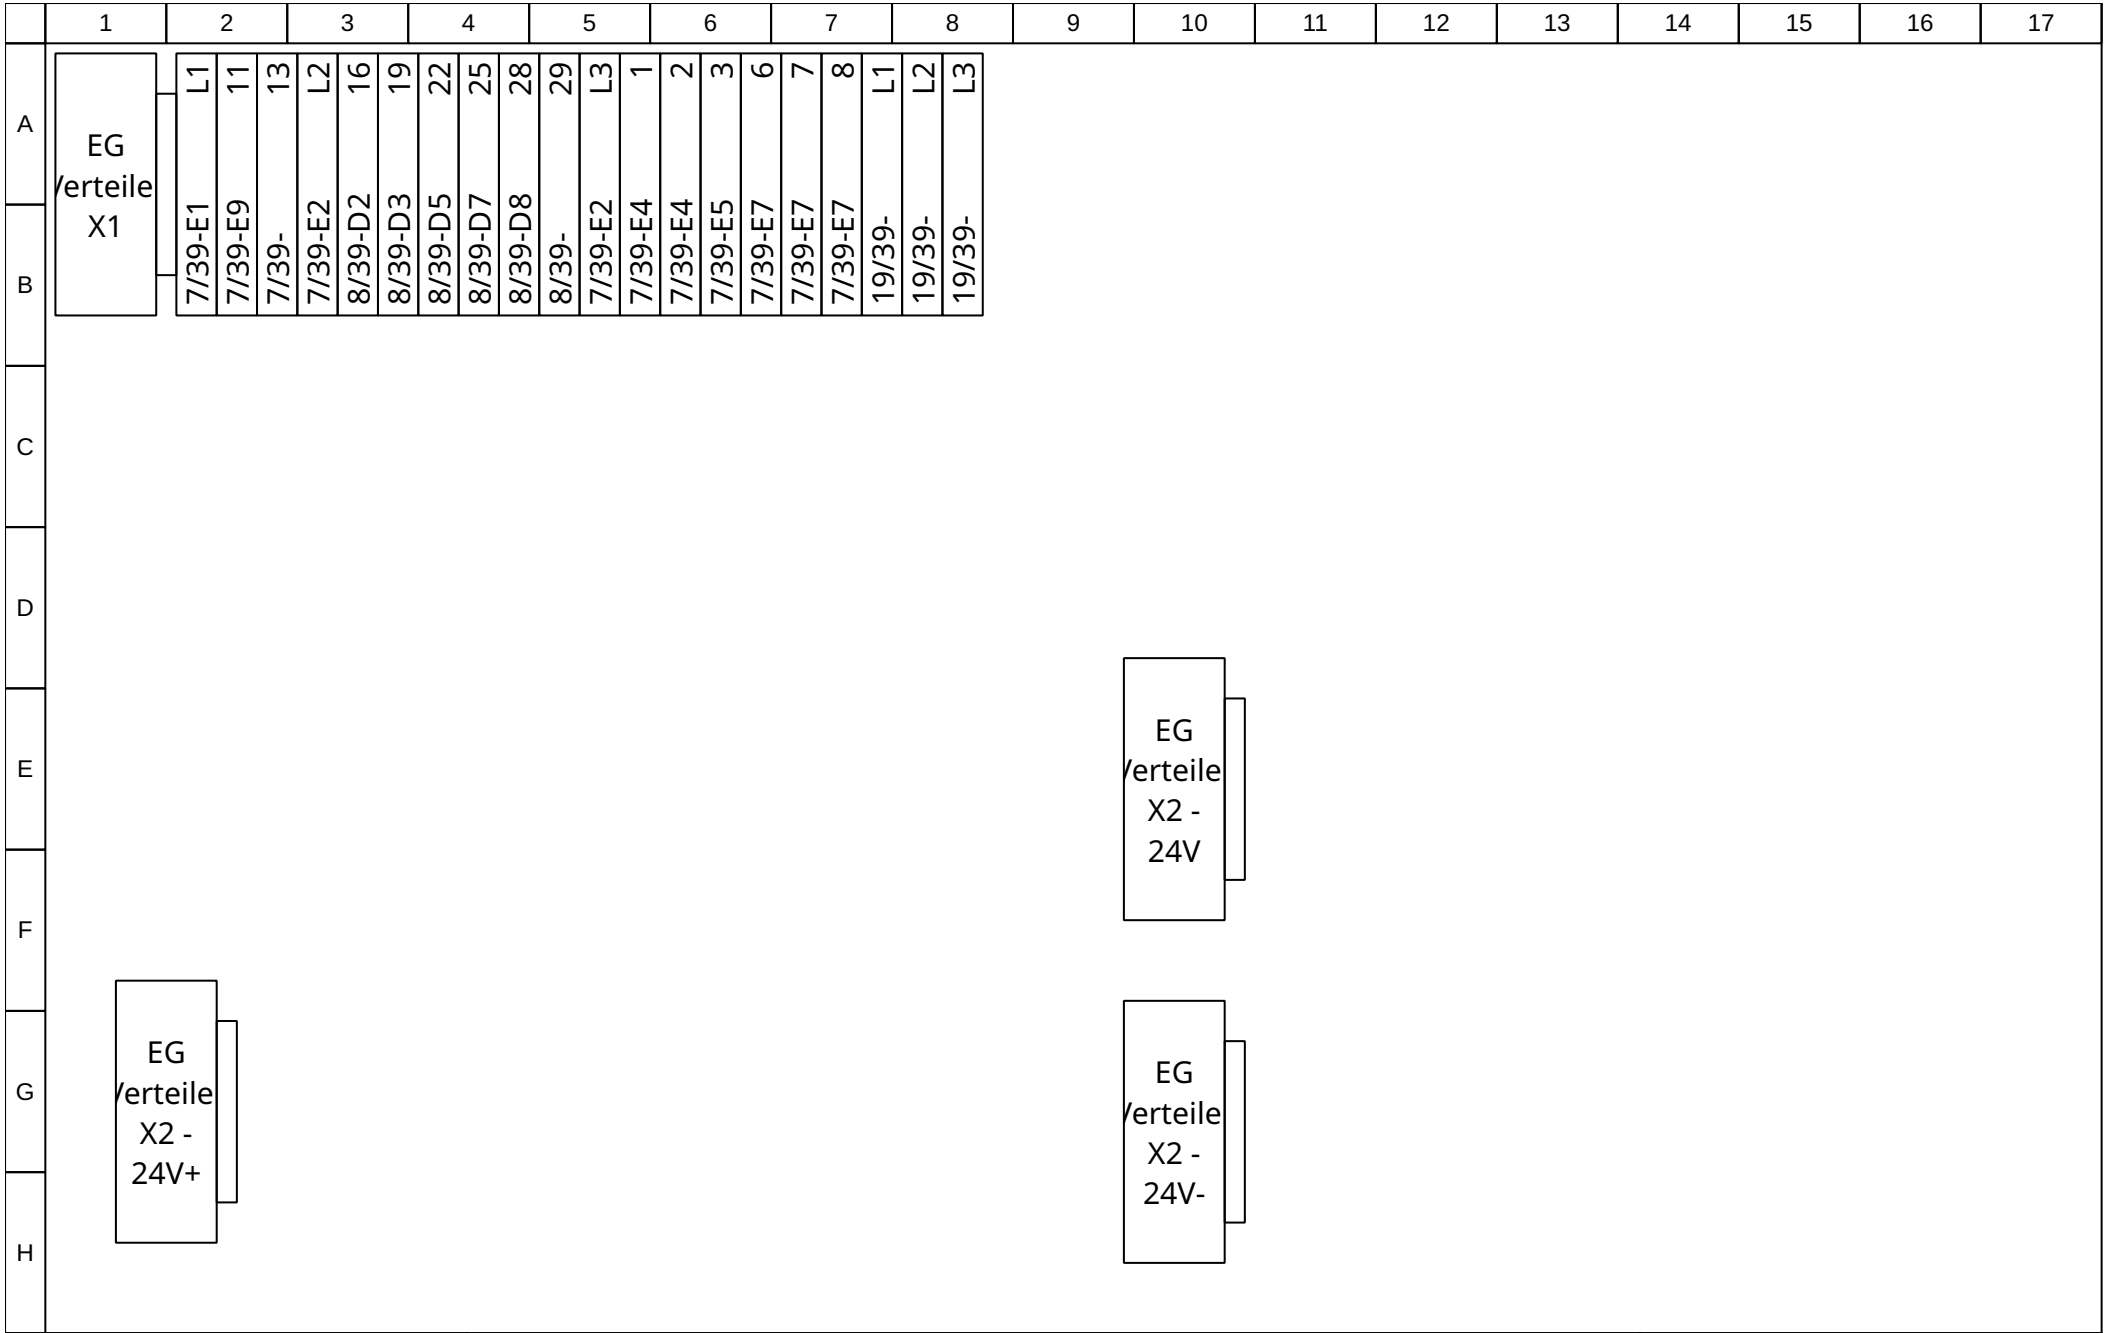



| | | |
|---|---|---|
| Autor: Entrich | Klemmenplan | Datei: |
| Datum: 10/16/26 | | Seite: 18/39 |

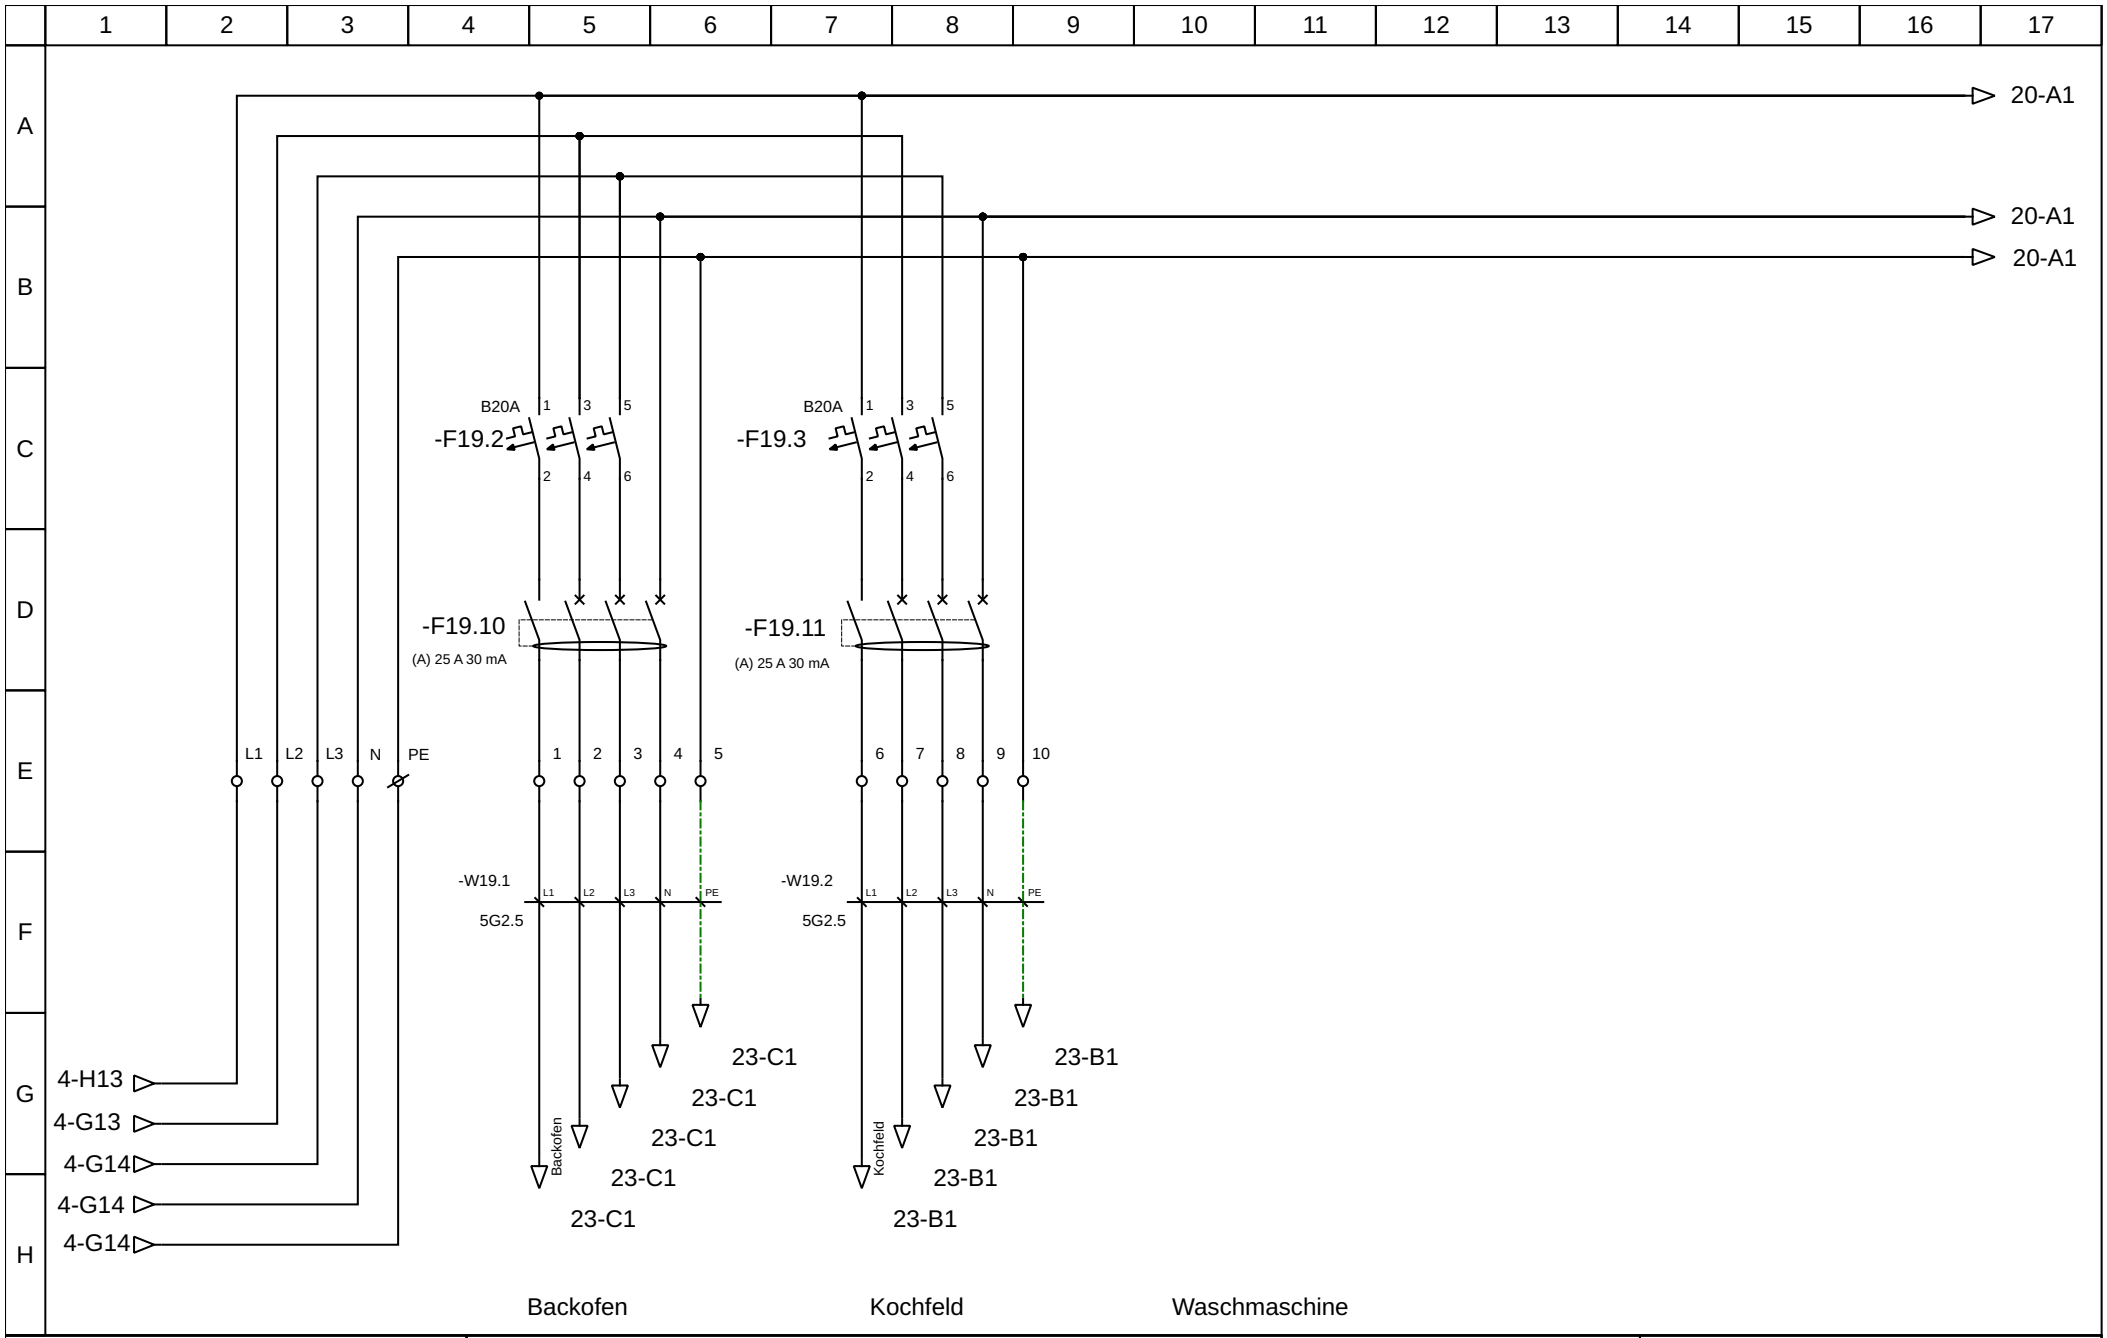



| | | |
|---|---|---|
| Autor: Entrich | Sicherung | Datei: |
| Datum: 10/16/26 | | Seite: 19/39 |

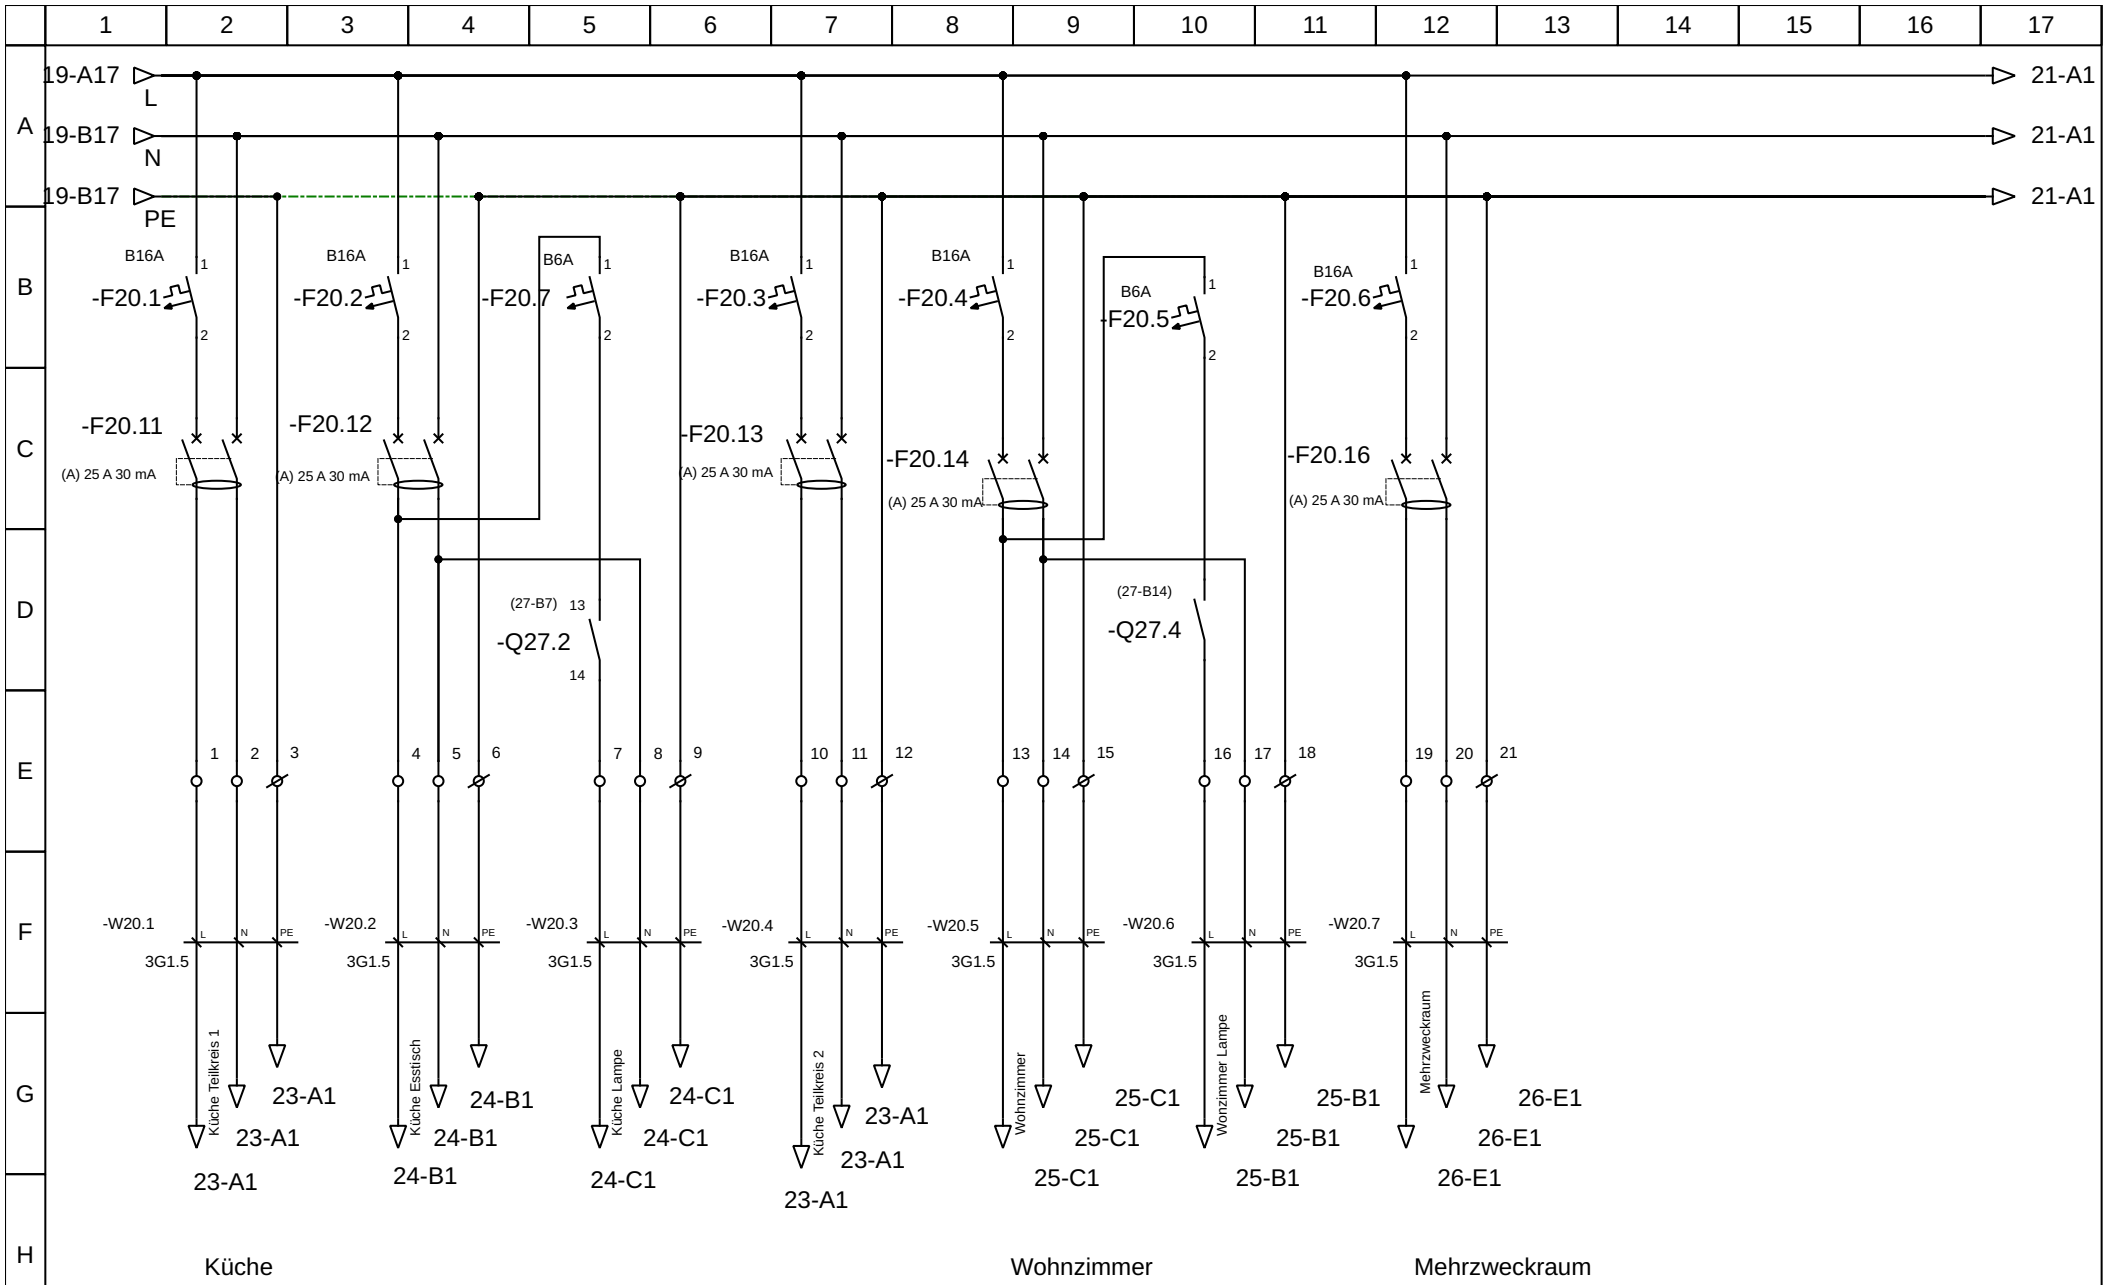



| | | |
|---|---|---|
| Autor: Entrich | Sicherung | Datei: |
| Datum: 10/16/26 | | Seite: 20/39 |

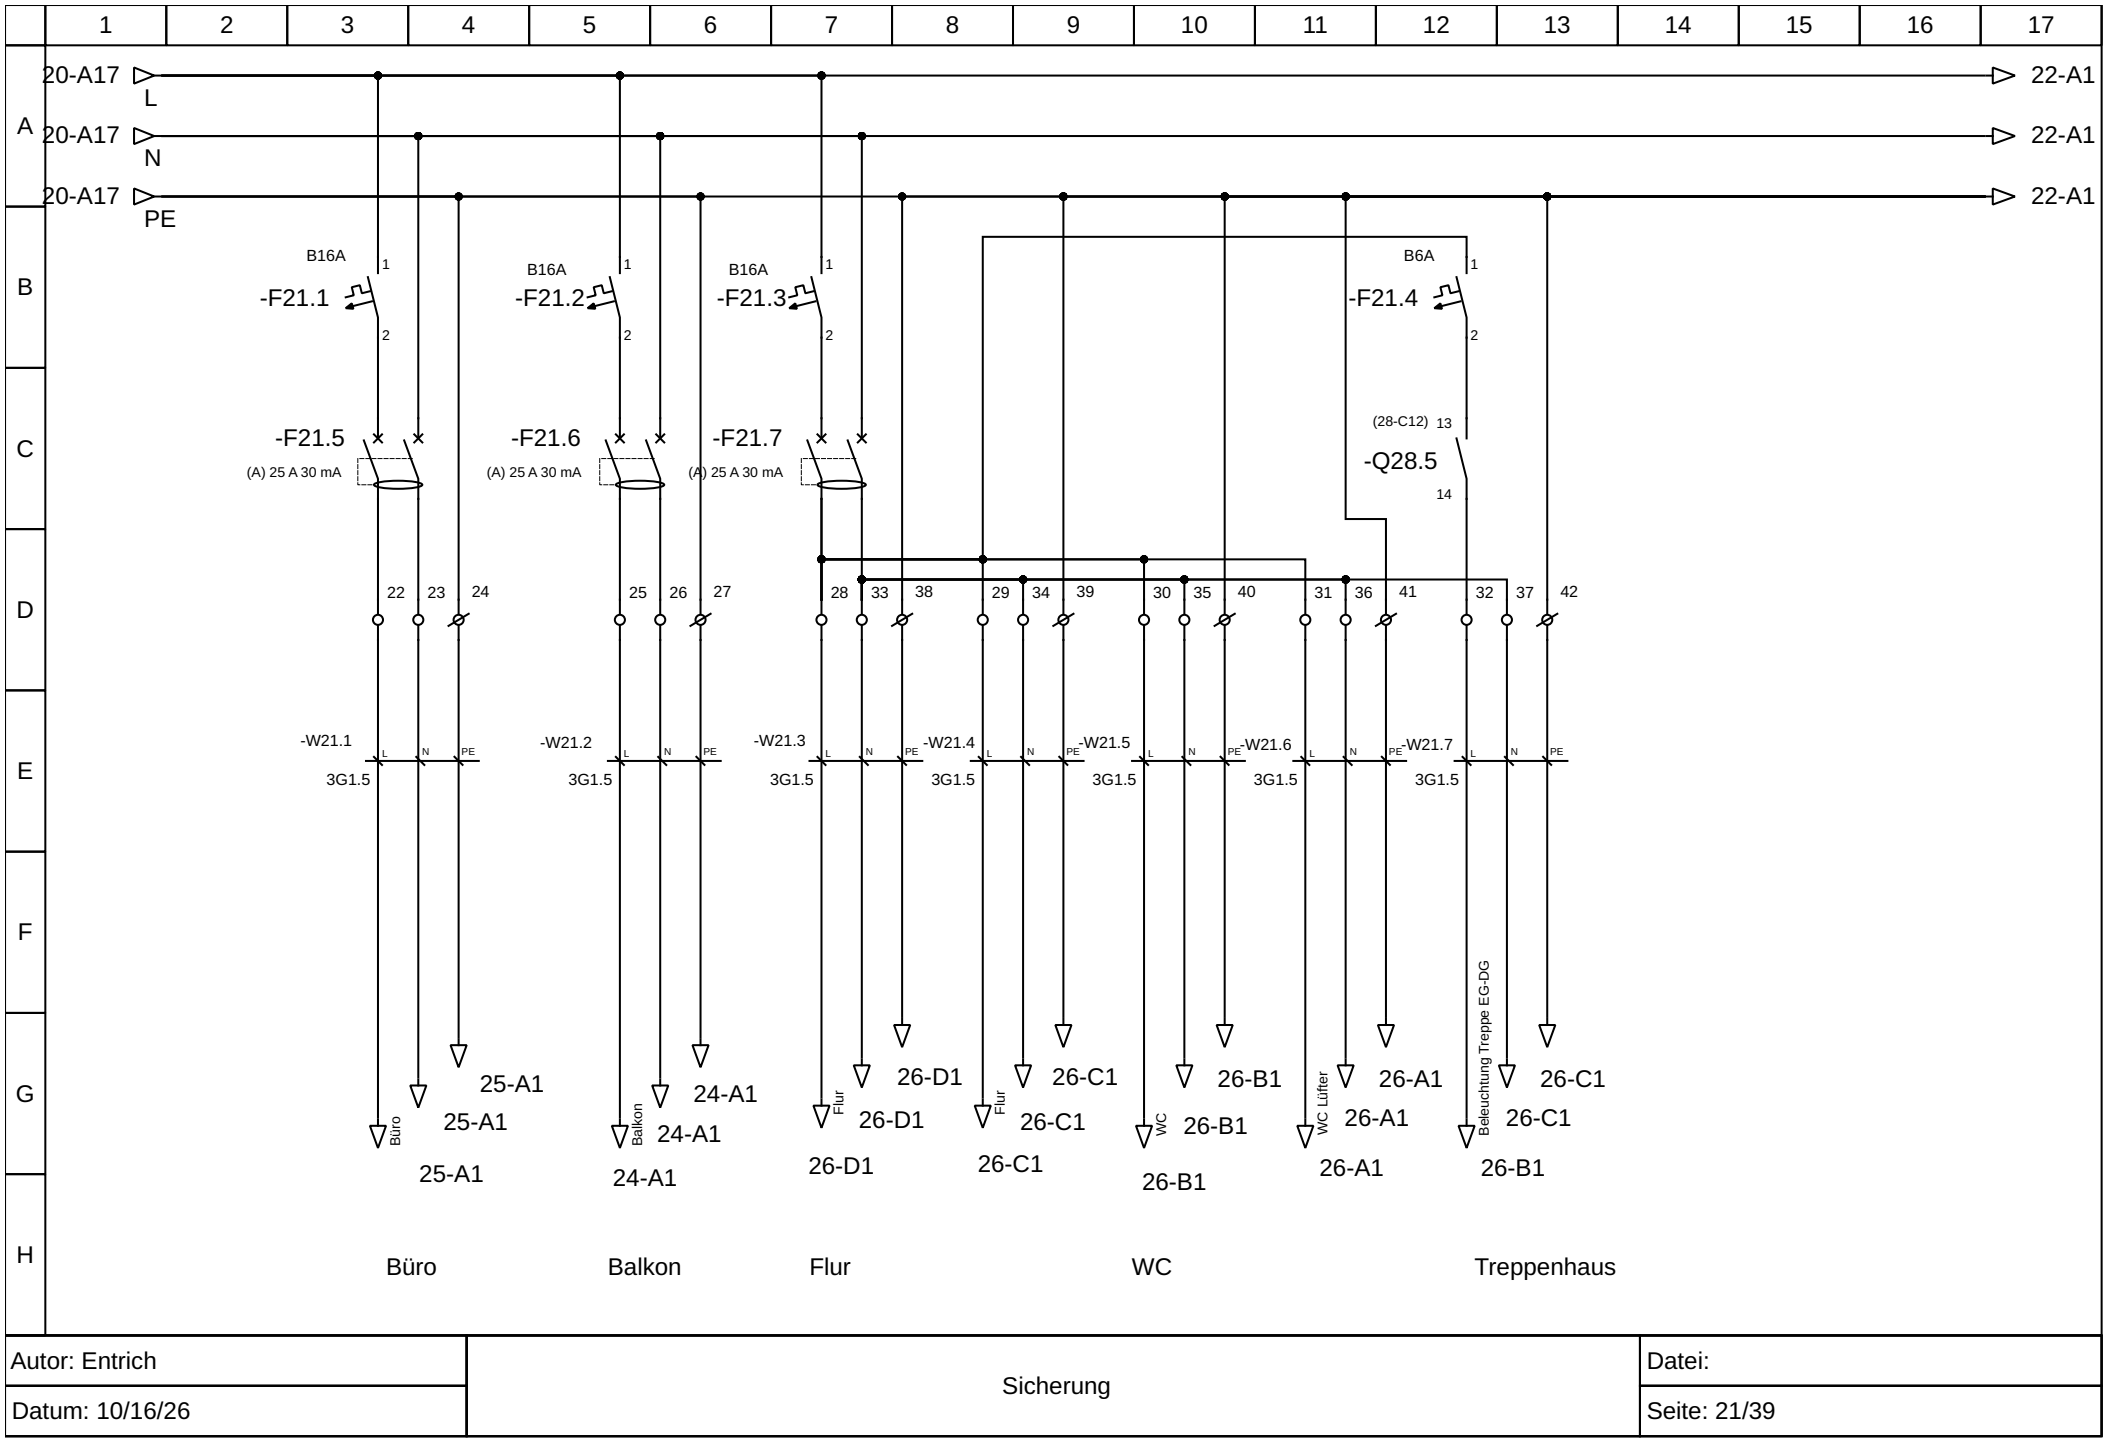



| | | |
|---|---|---|
| Autor: Entrich | Sicherung | Datei: |
| Datum: 10/16/26 | | Seite: 21/39 |

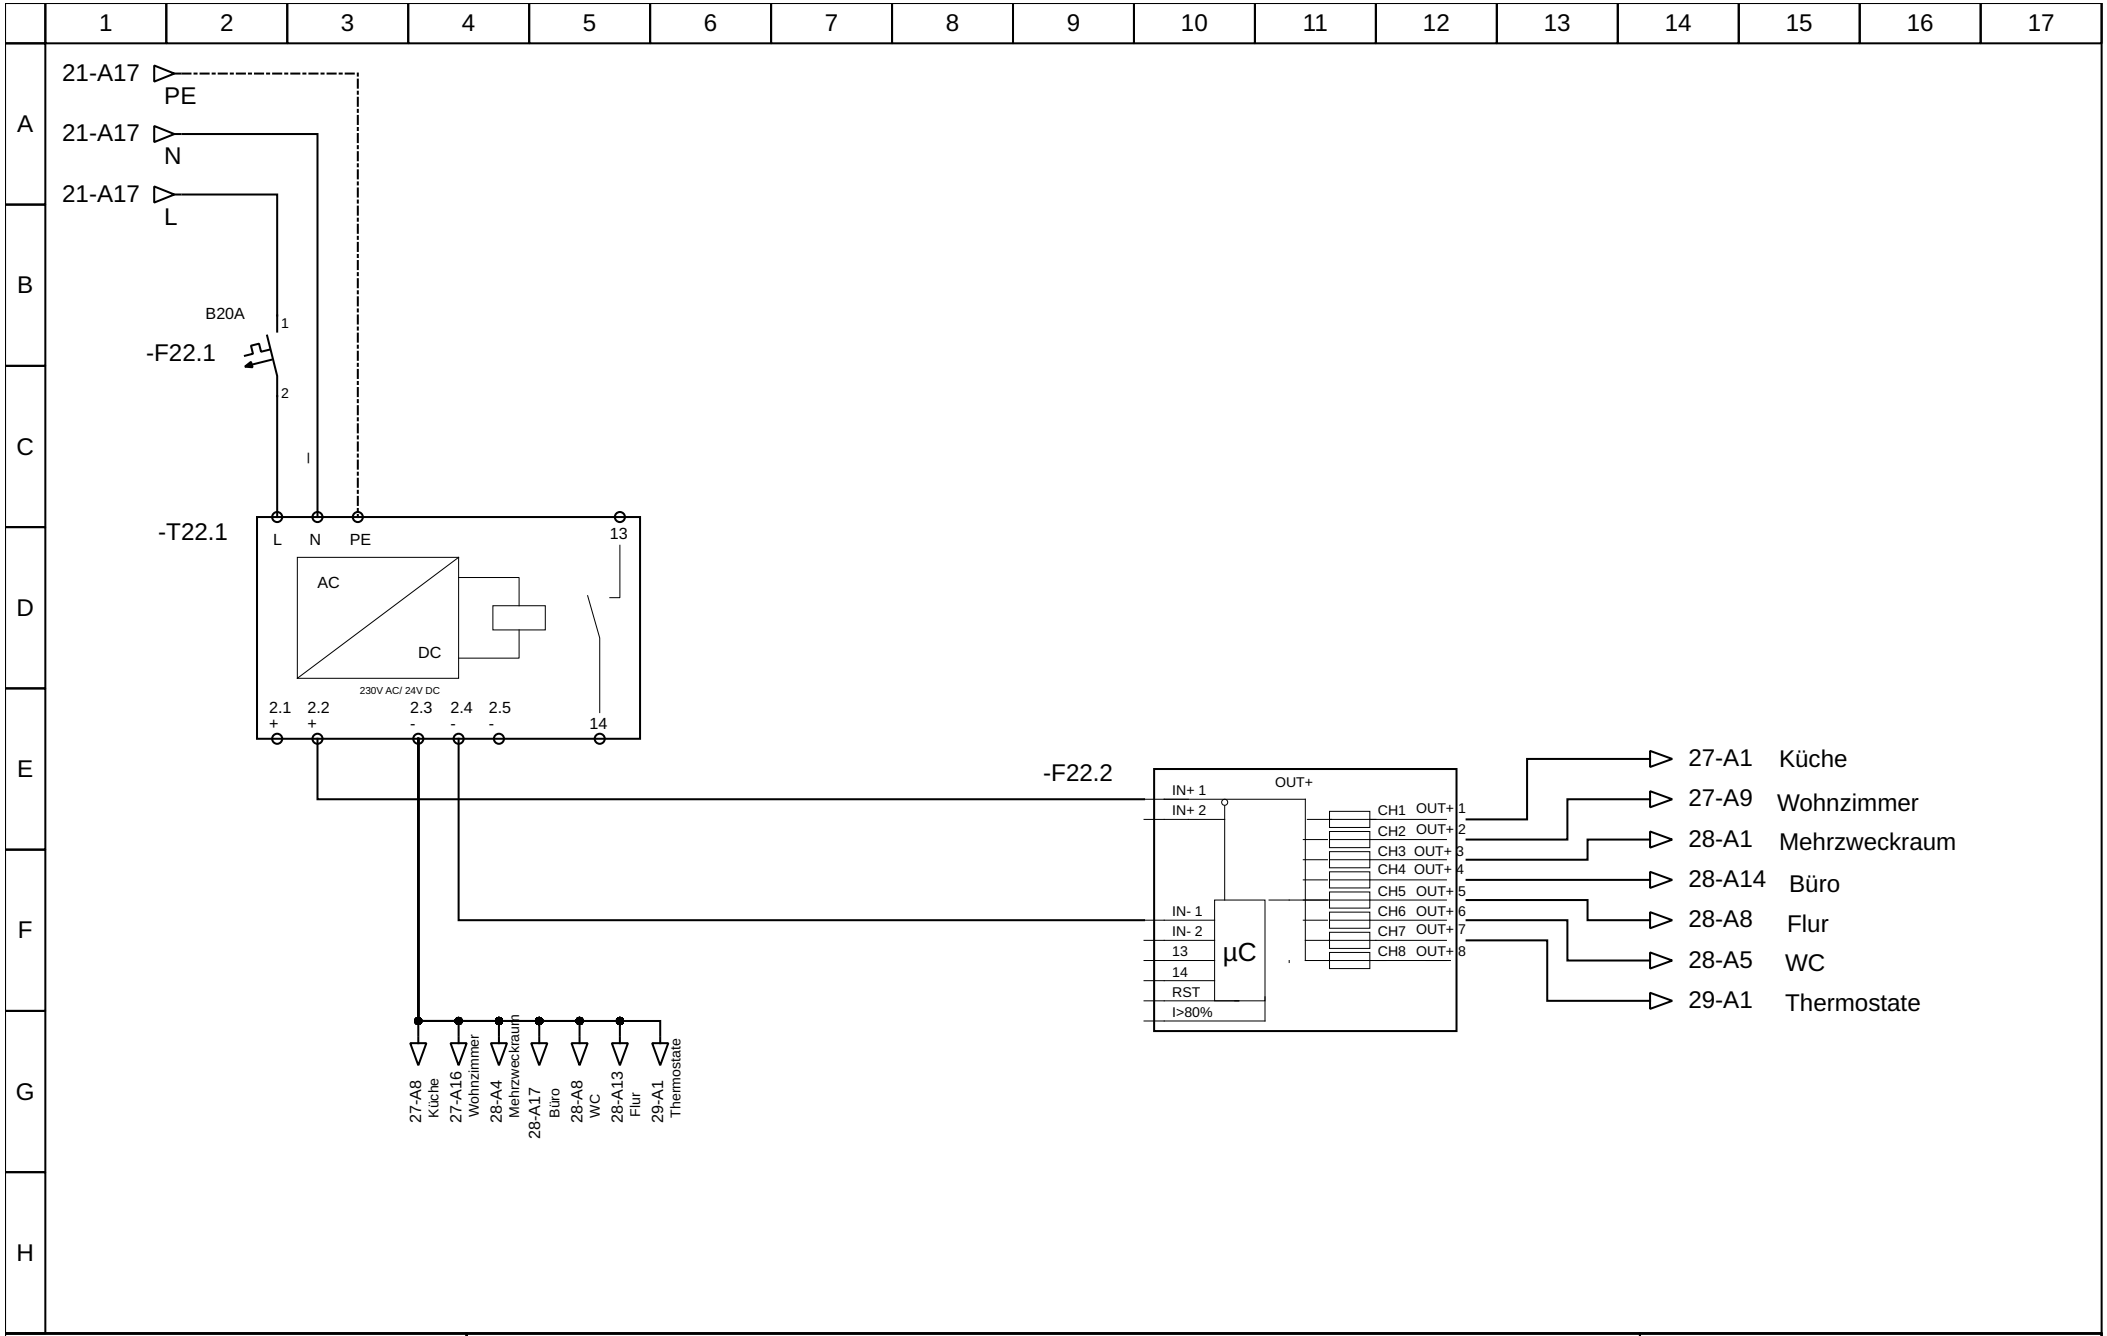



| | | |
|---|---|---|
| Autor: Entrich | Kleinspannungsversorgung | Datei: |
| Datum: 10/16/26 | | Seite: 22/39 |

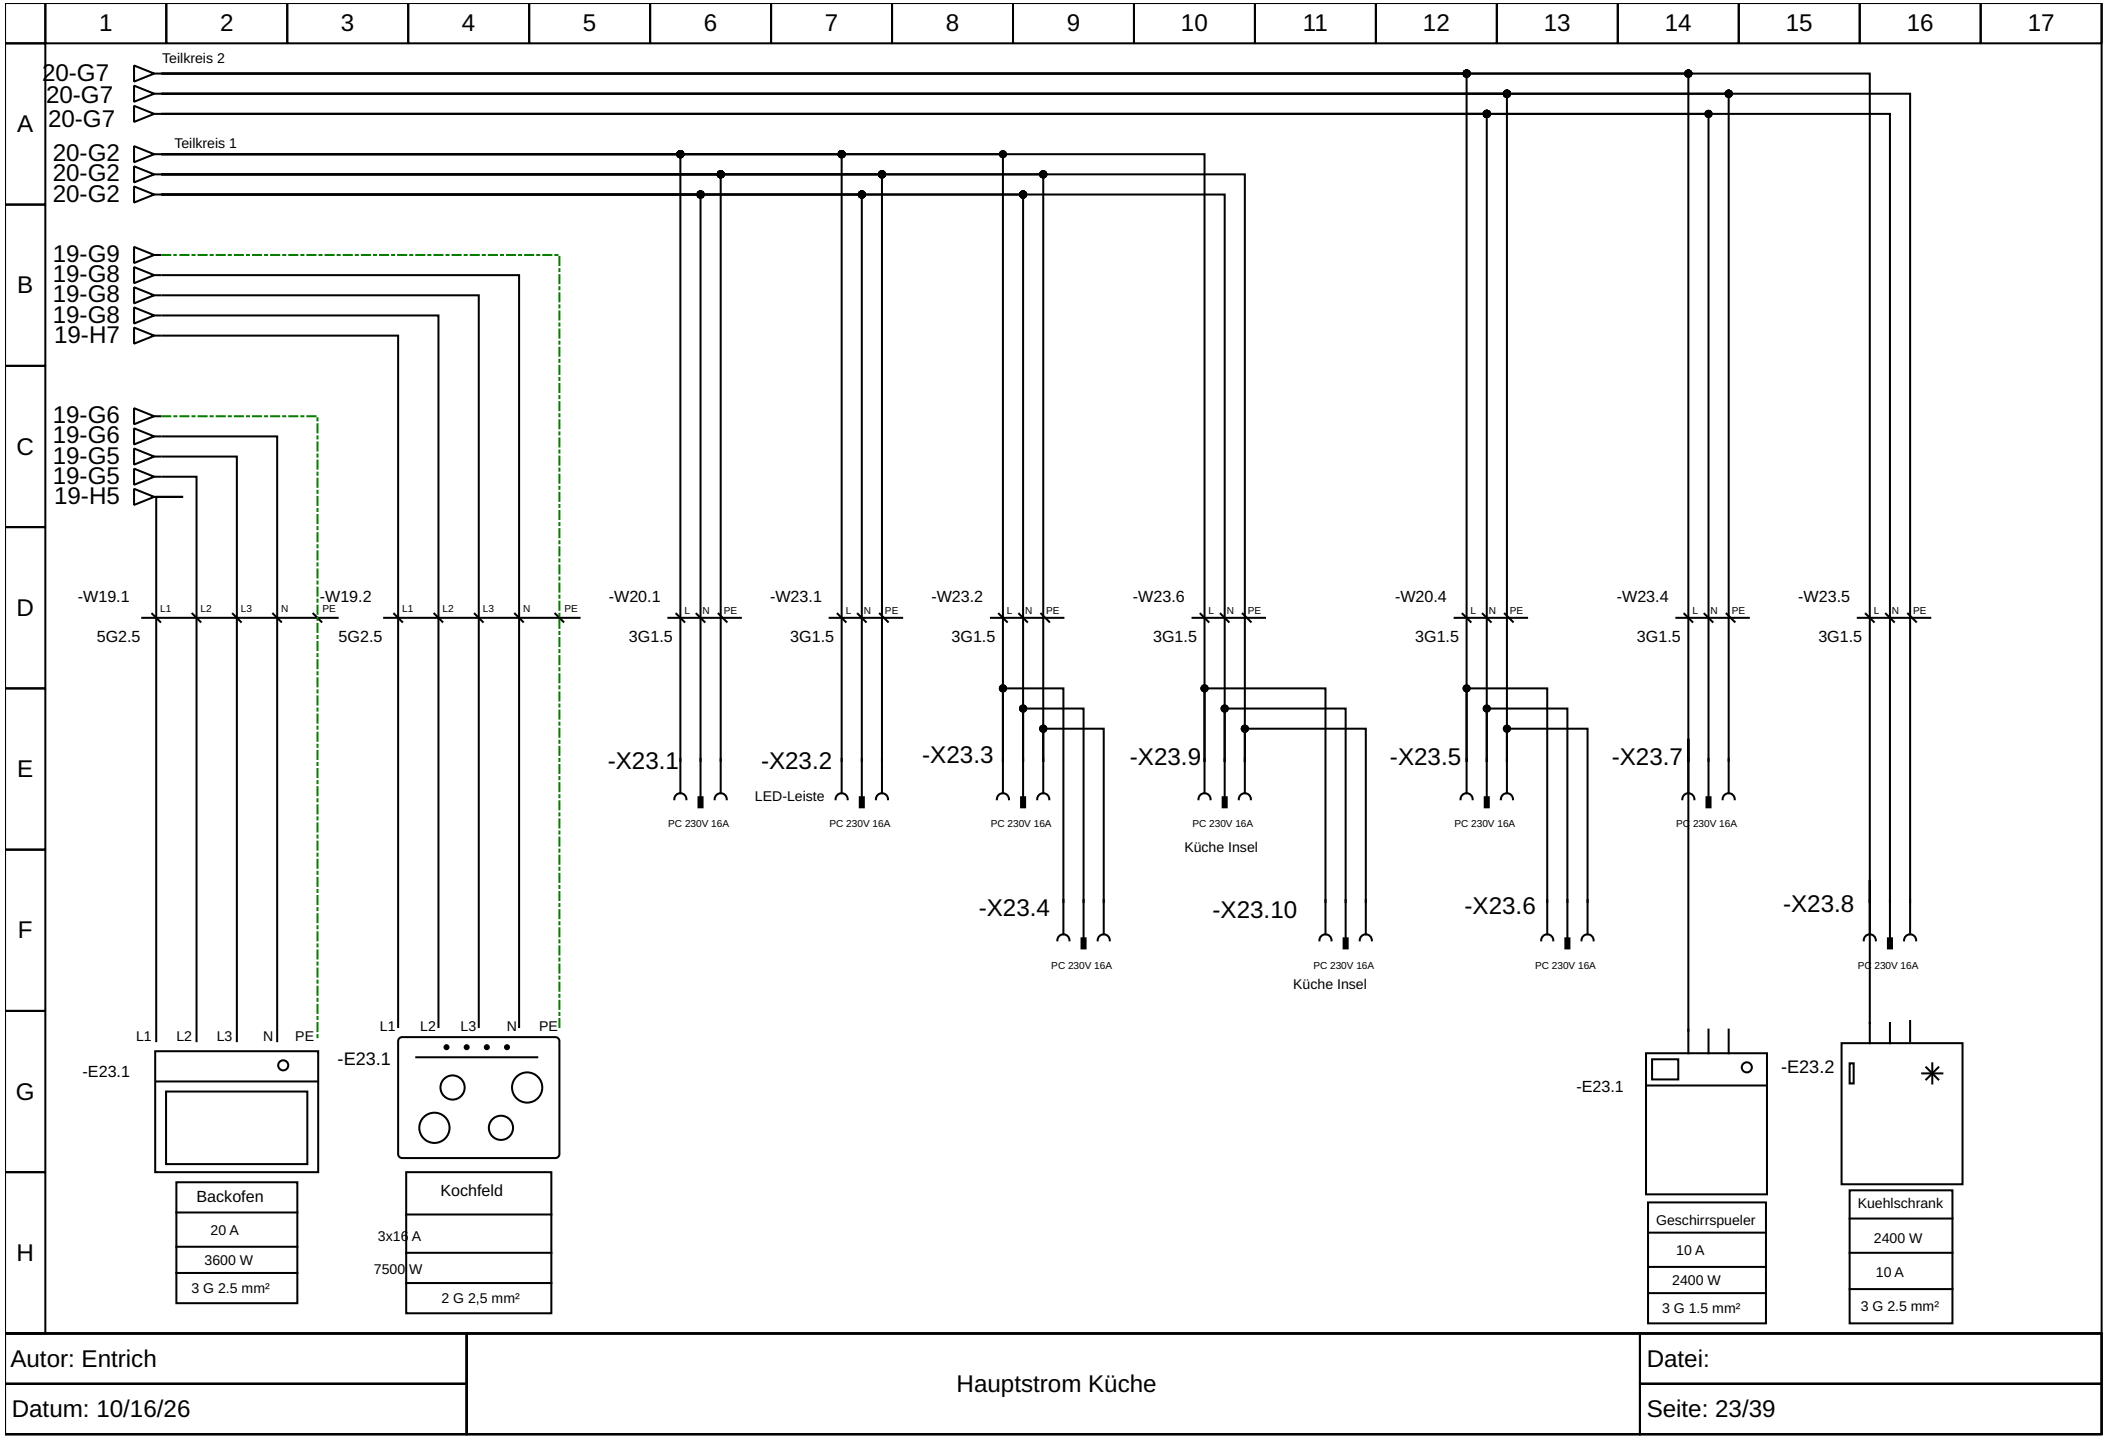



| | | |
|---|---|---|
| Autor: Entrich | Hauptstrom Küche | Datei: |
| Datum: 10/16/26 | | Seite: 23/39 |

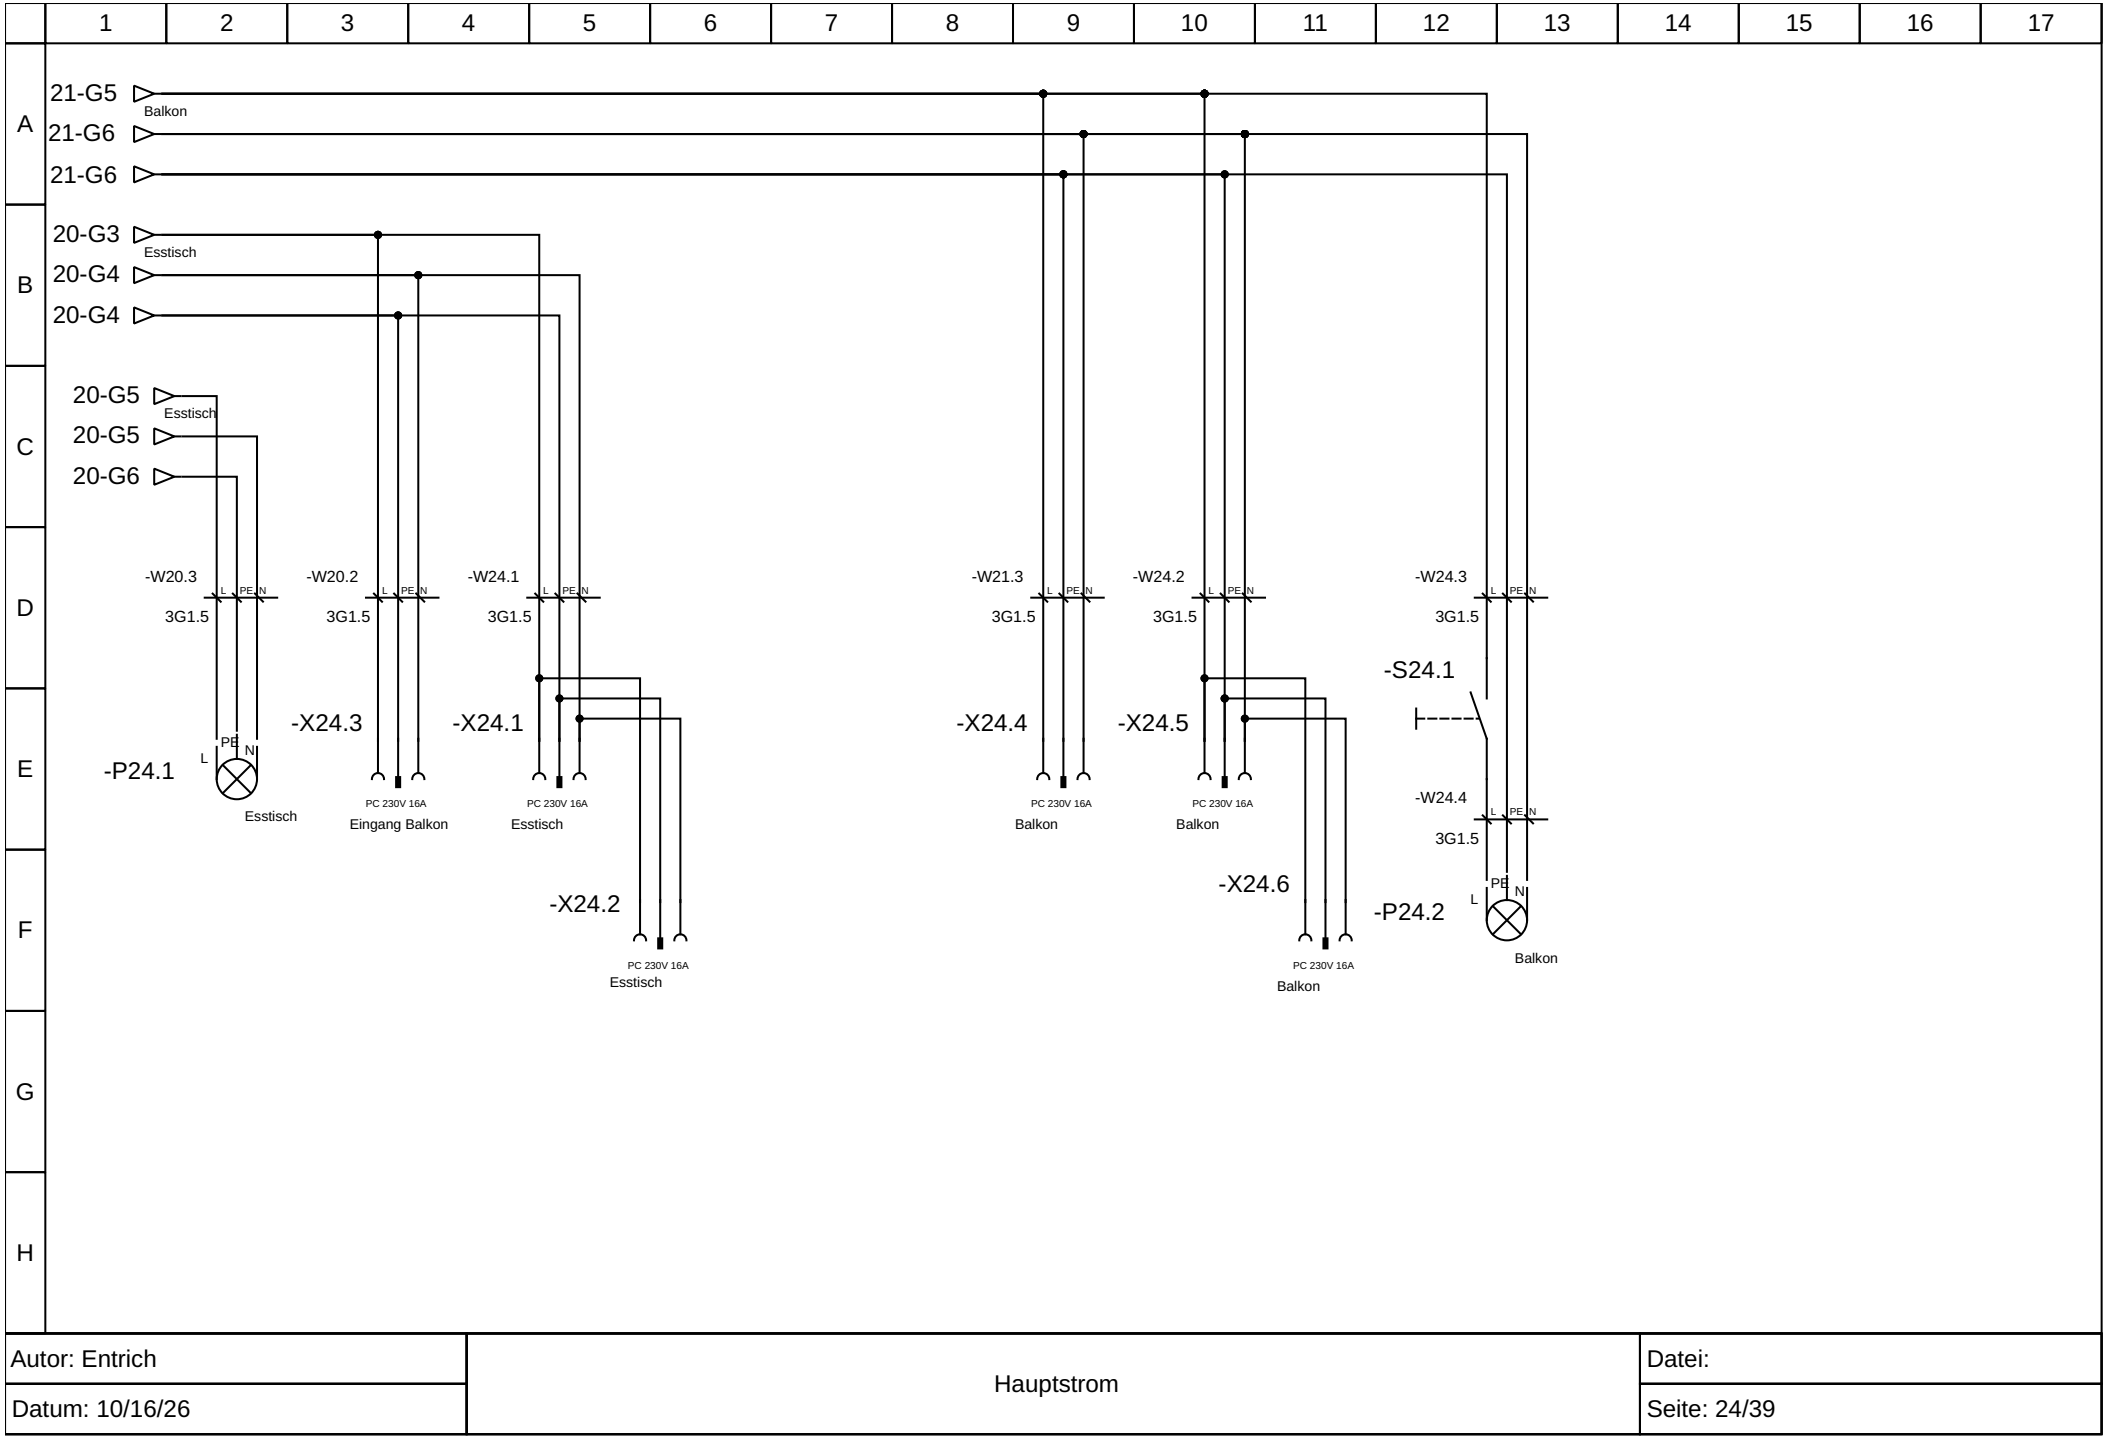



| | | |
|---|---|---|
| Autor: Entrich | Hauptstrom | Datei: |
| Datum: 10/16/26 | | Seite: 24/39 |

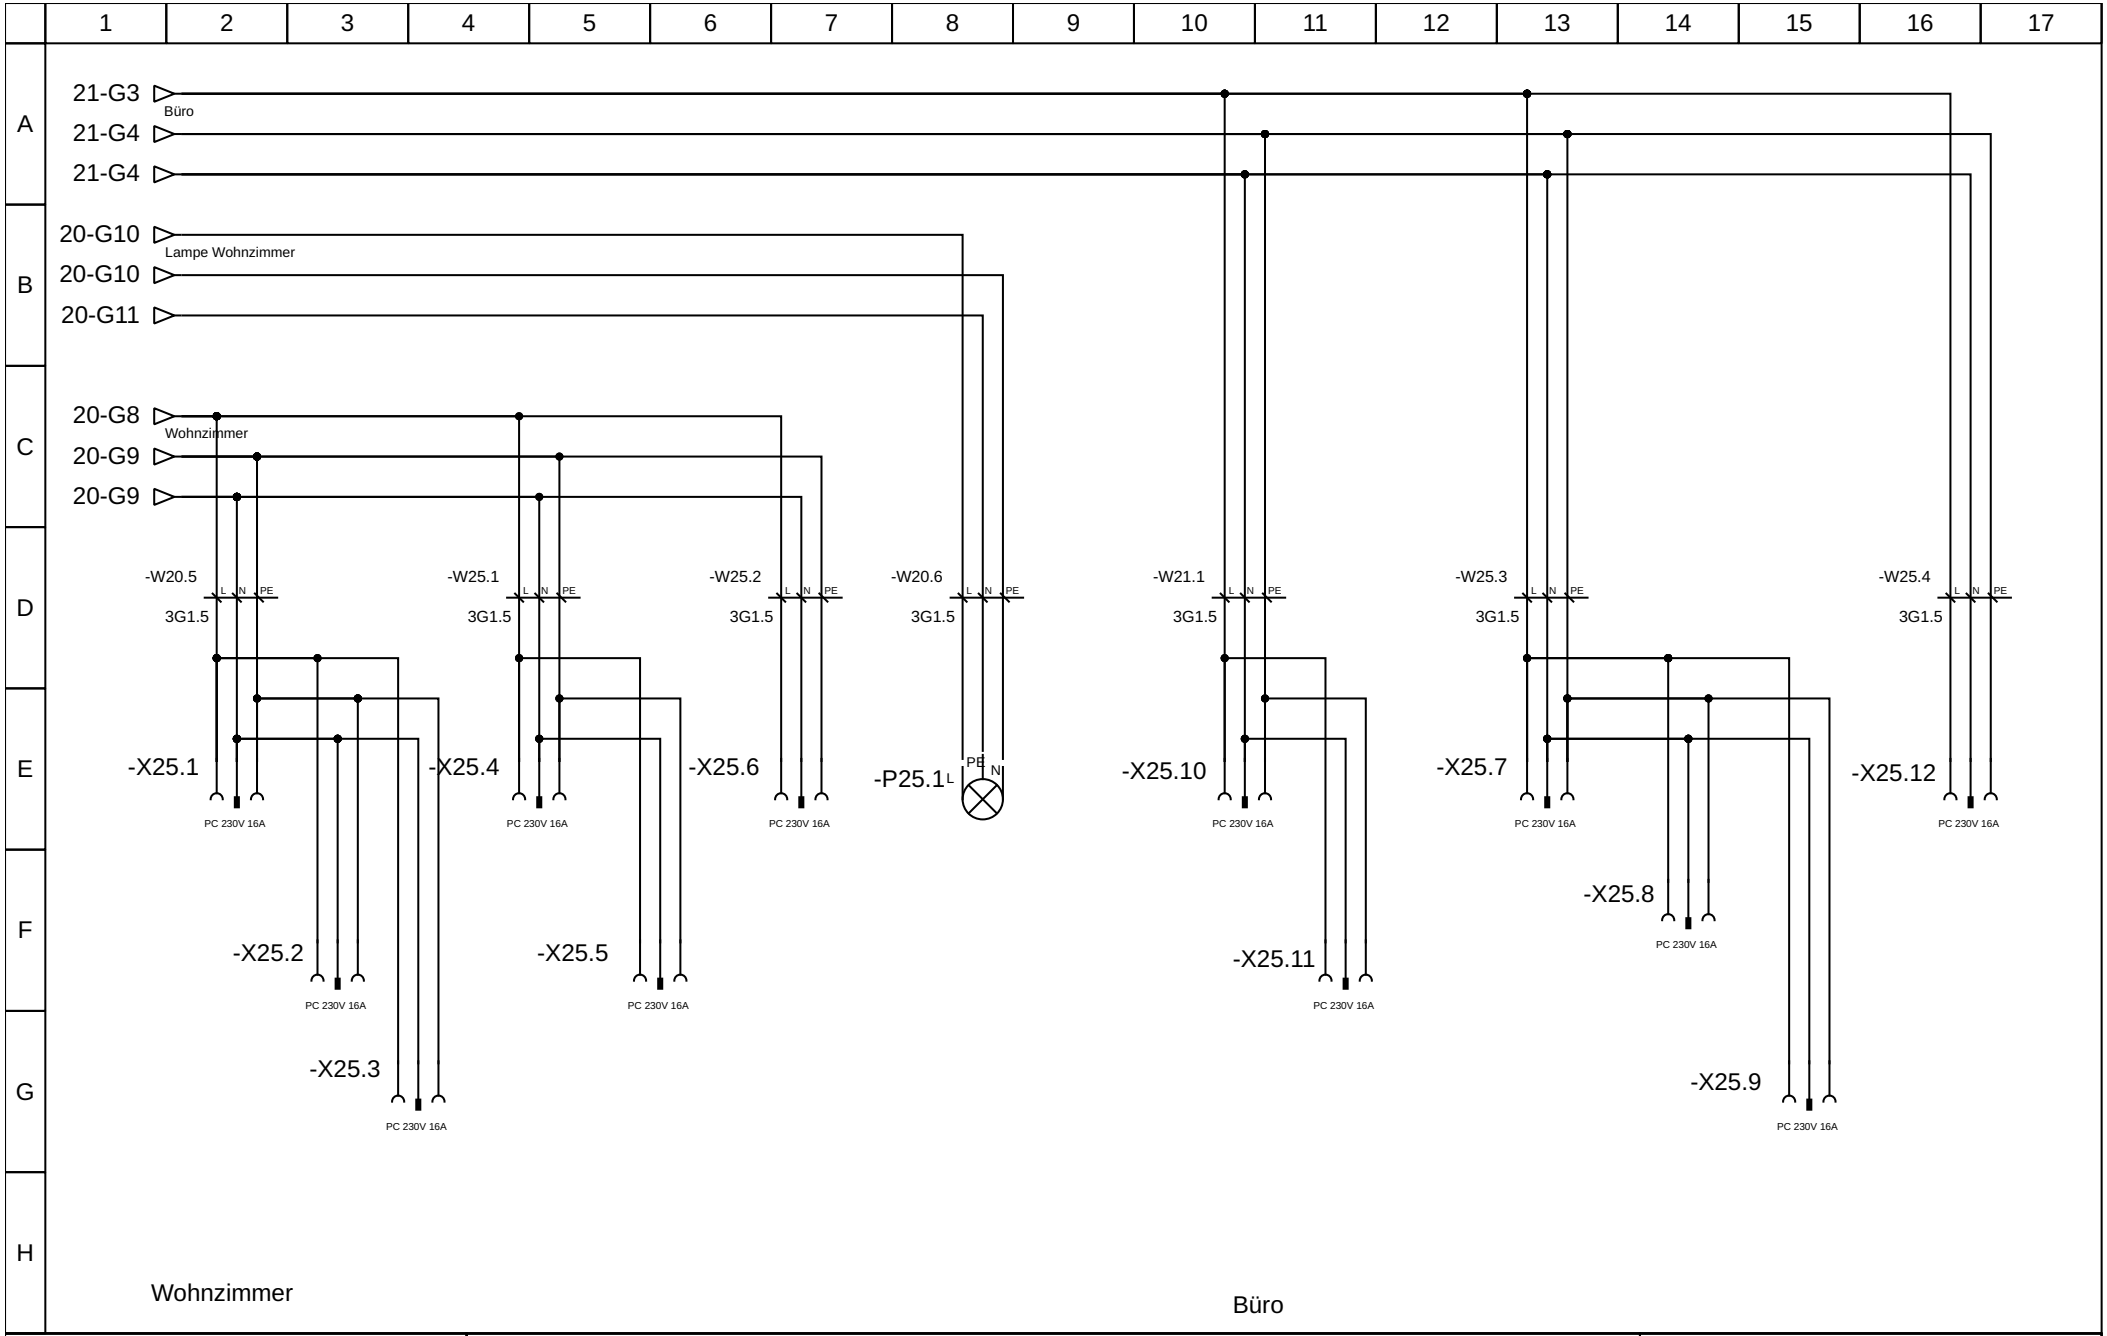



| | | |
|---|---|---|
| Autor: Entrich | Hauptstrom | Datei: |
| Datum: 10/16/26 | | Seite: 25/39 |

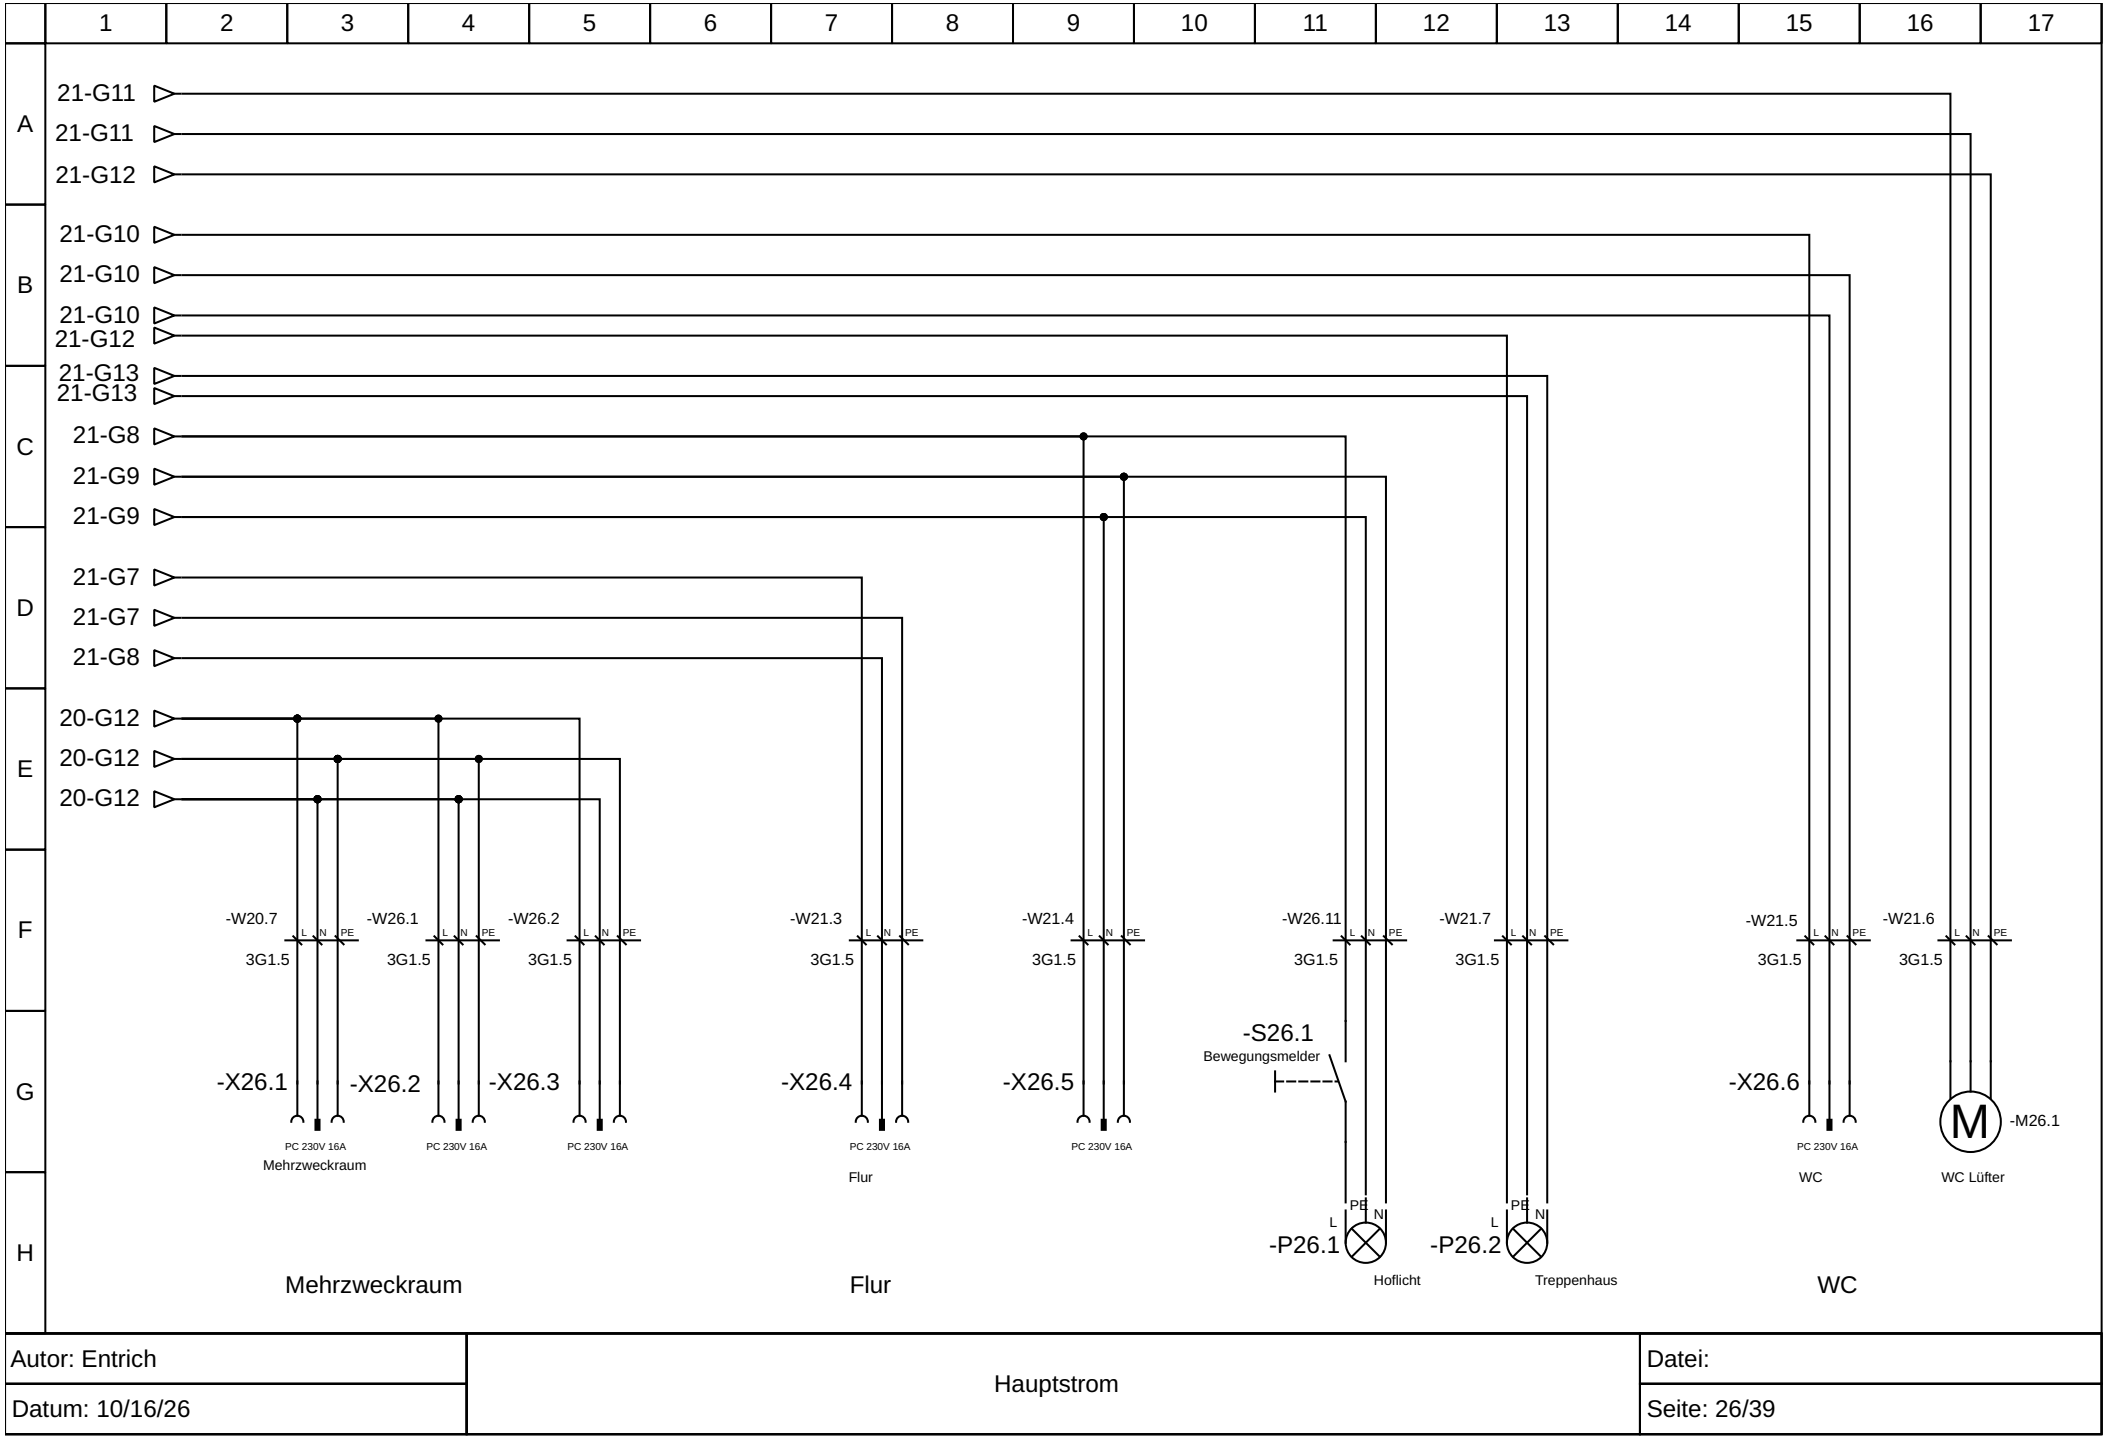



| | | |
|---|---|---|
| Autor: Entrich | Hauptstrom | Datei: |
| Datum: 10/16/26 | | Seite: 26/39 |

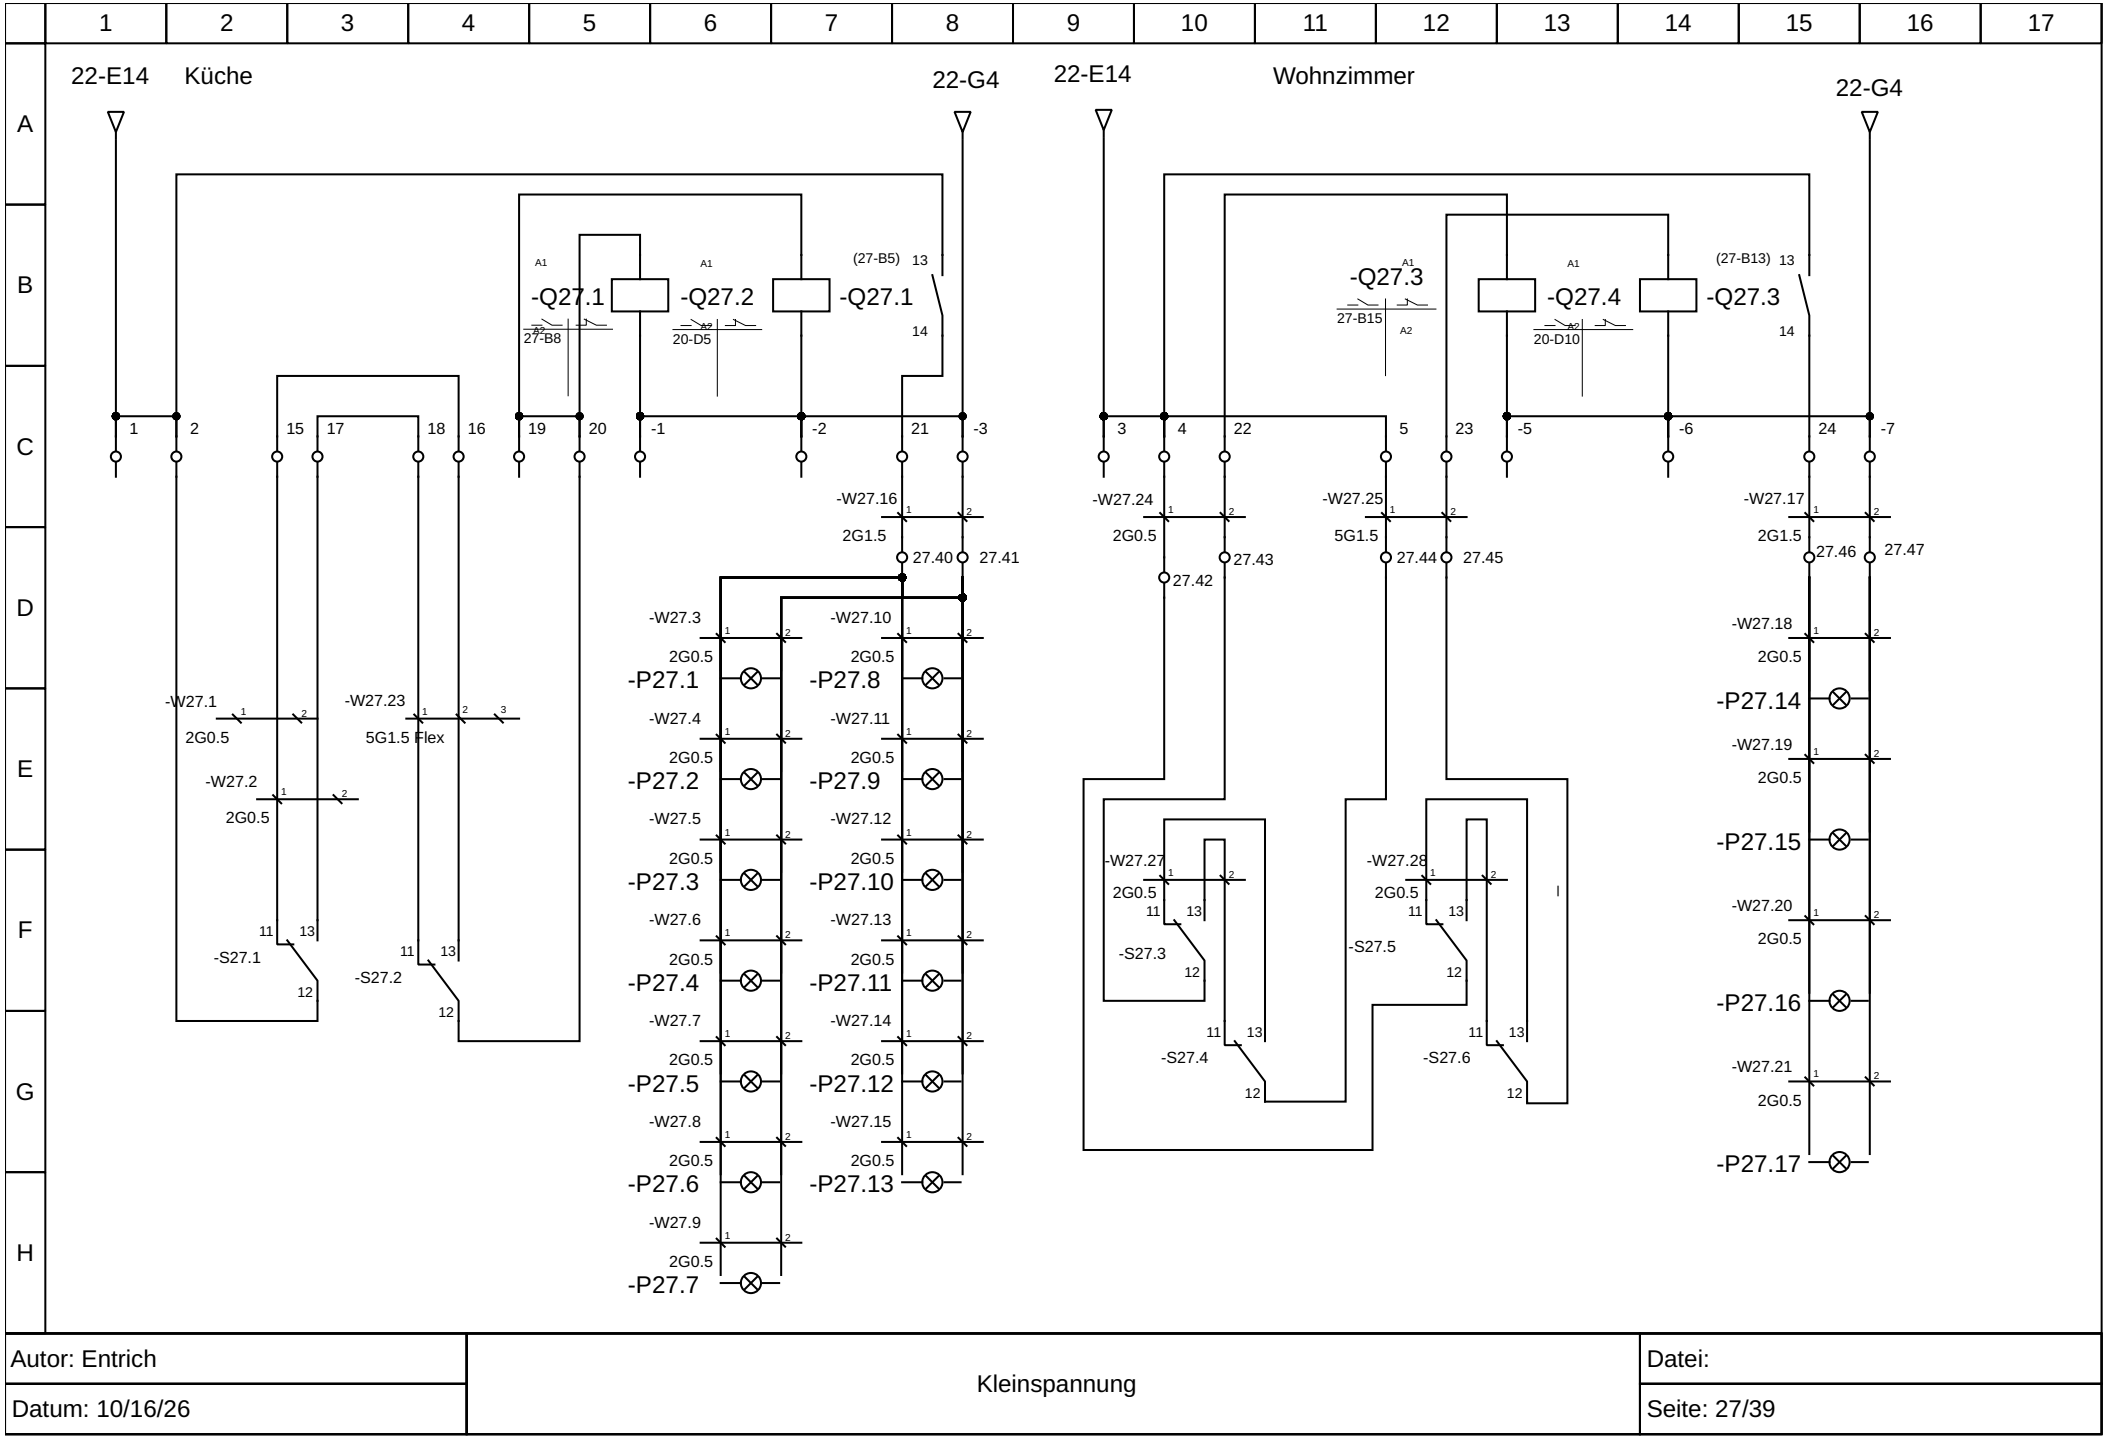


| | |
|---|---|
| Autor: Entrich | Datei: |
| Datum: 10/16/26 | Kleinspannung |
| | Seite: 27/39 |

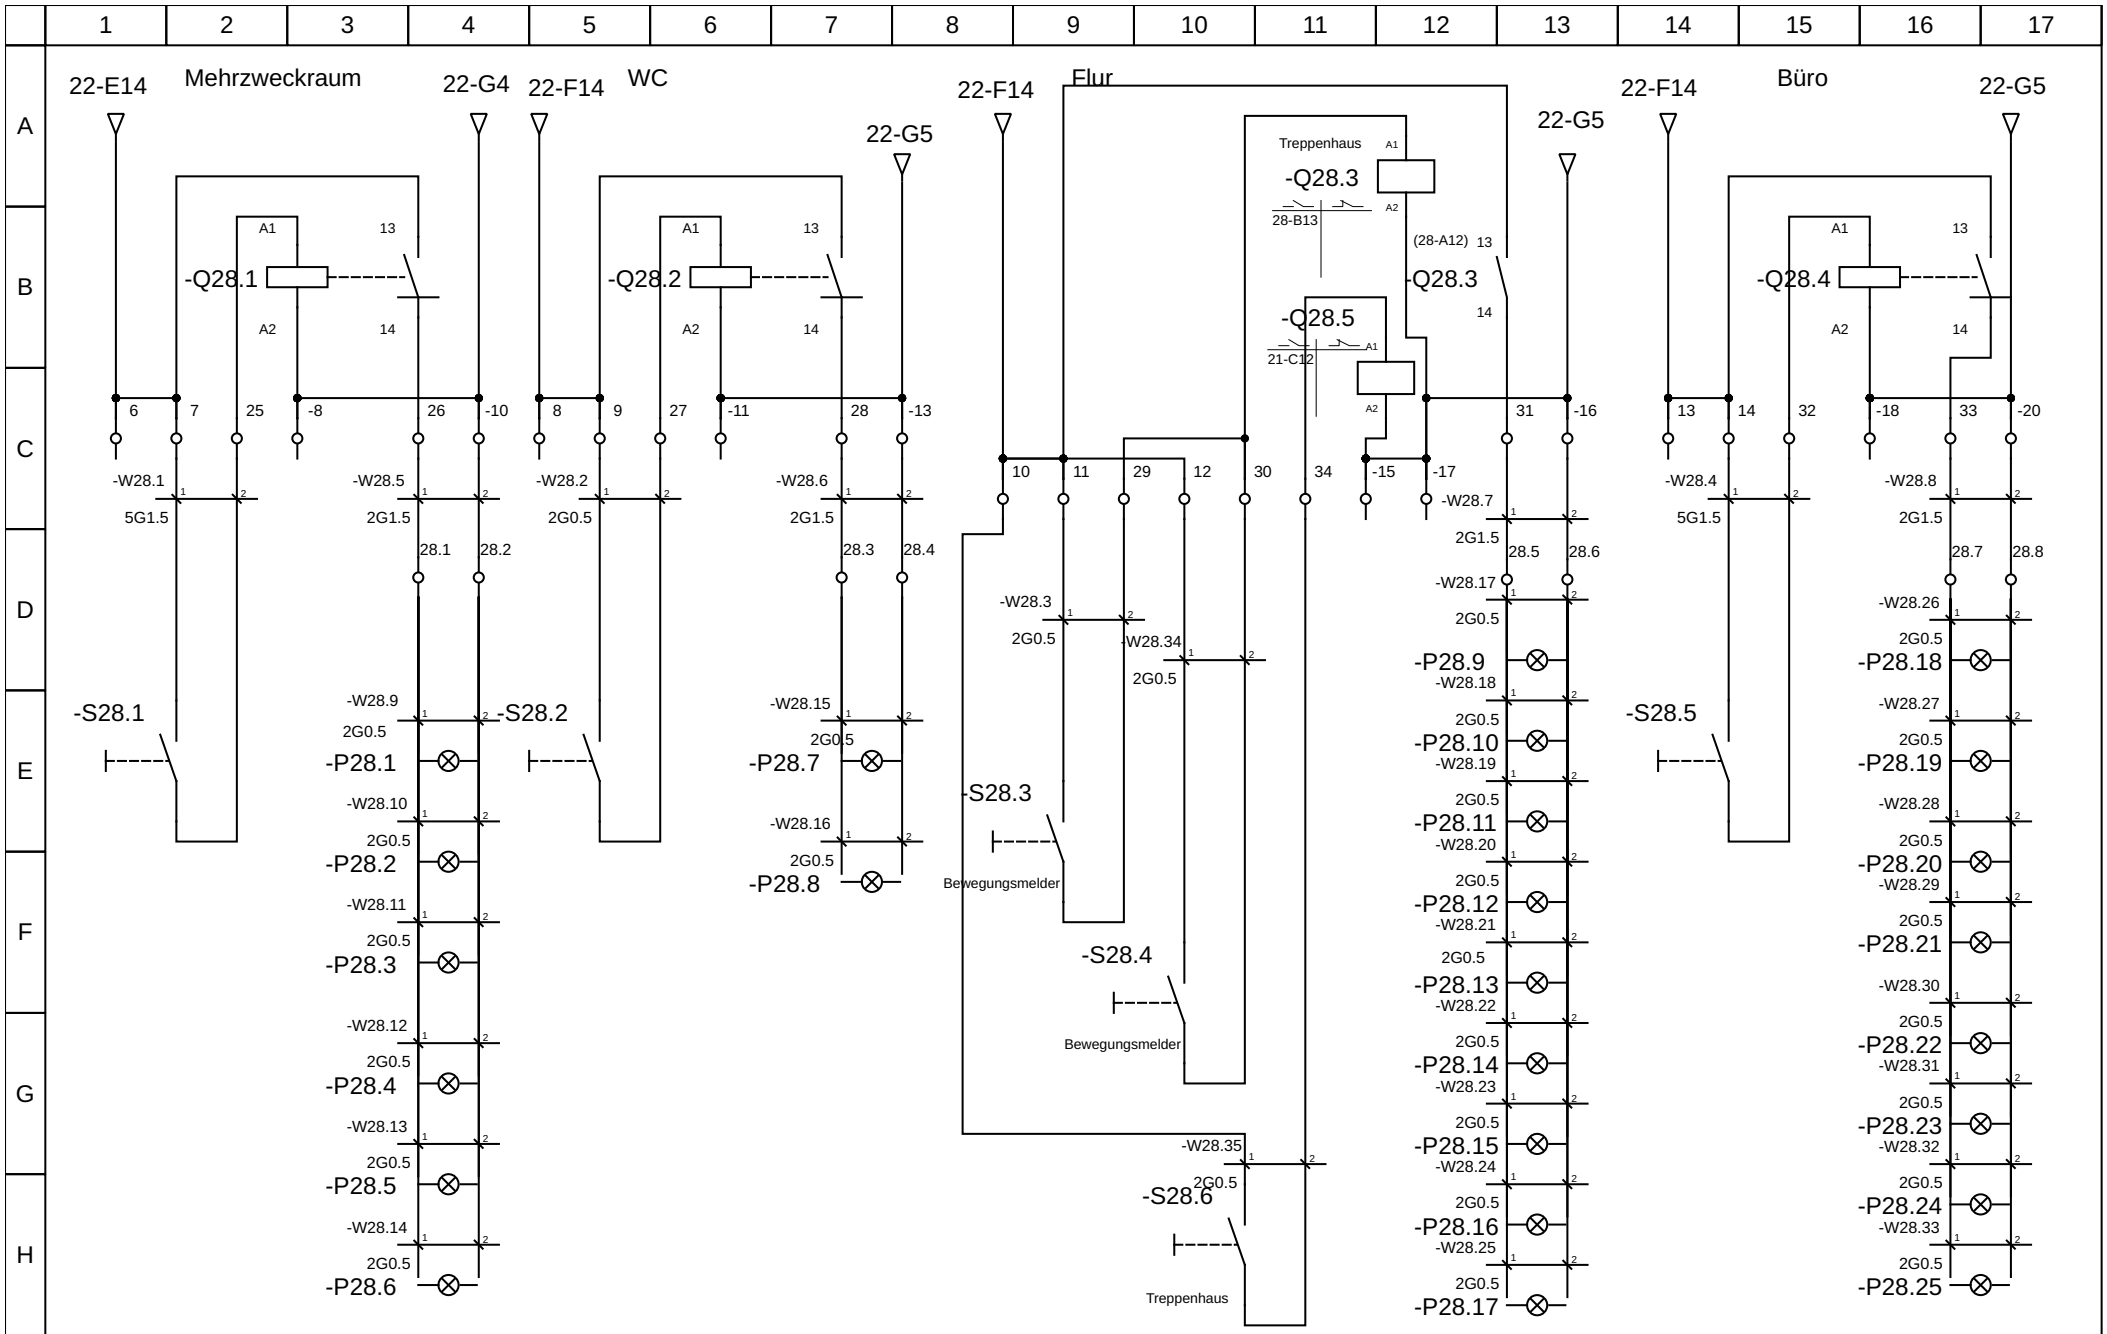



| | |
|---|---|
| Autor: Entrich | Datei: |
| Datum: 10/16/26 | Kleinspannung |
| | Seite: 28/39 |

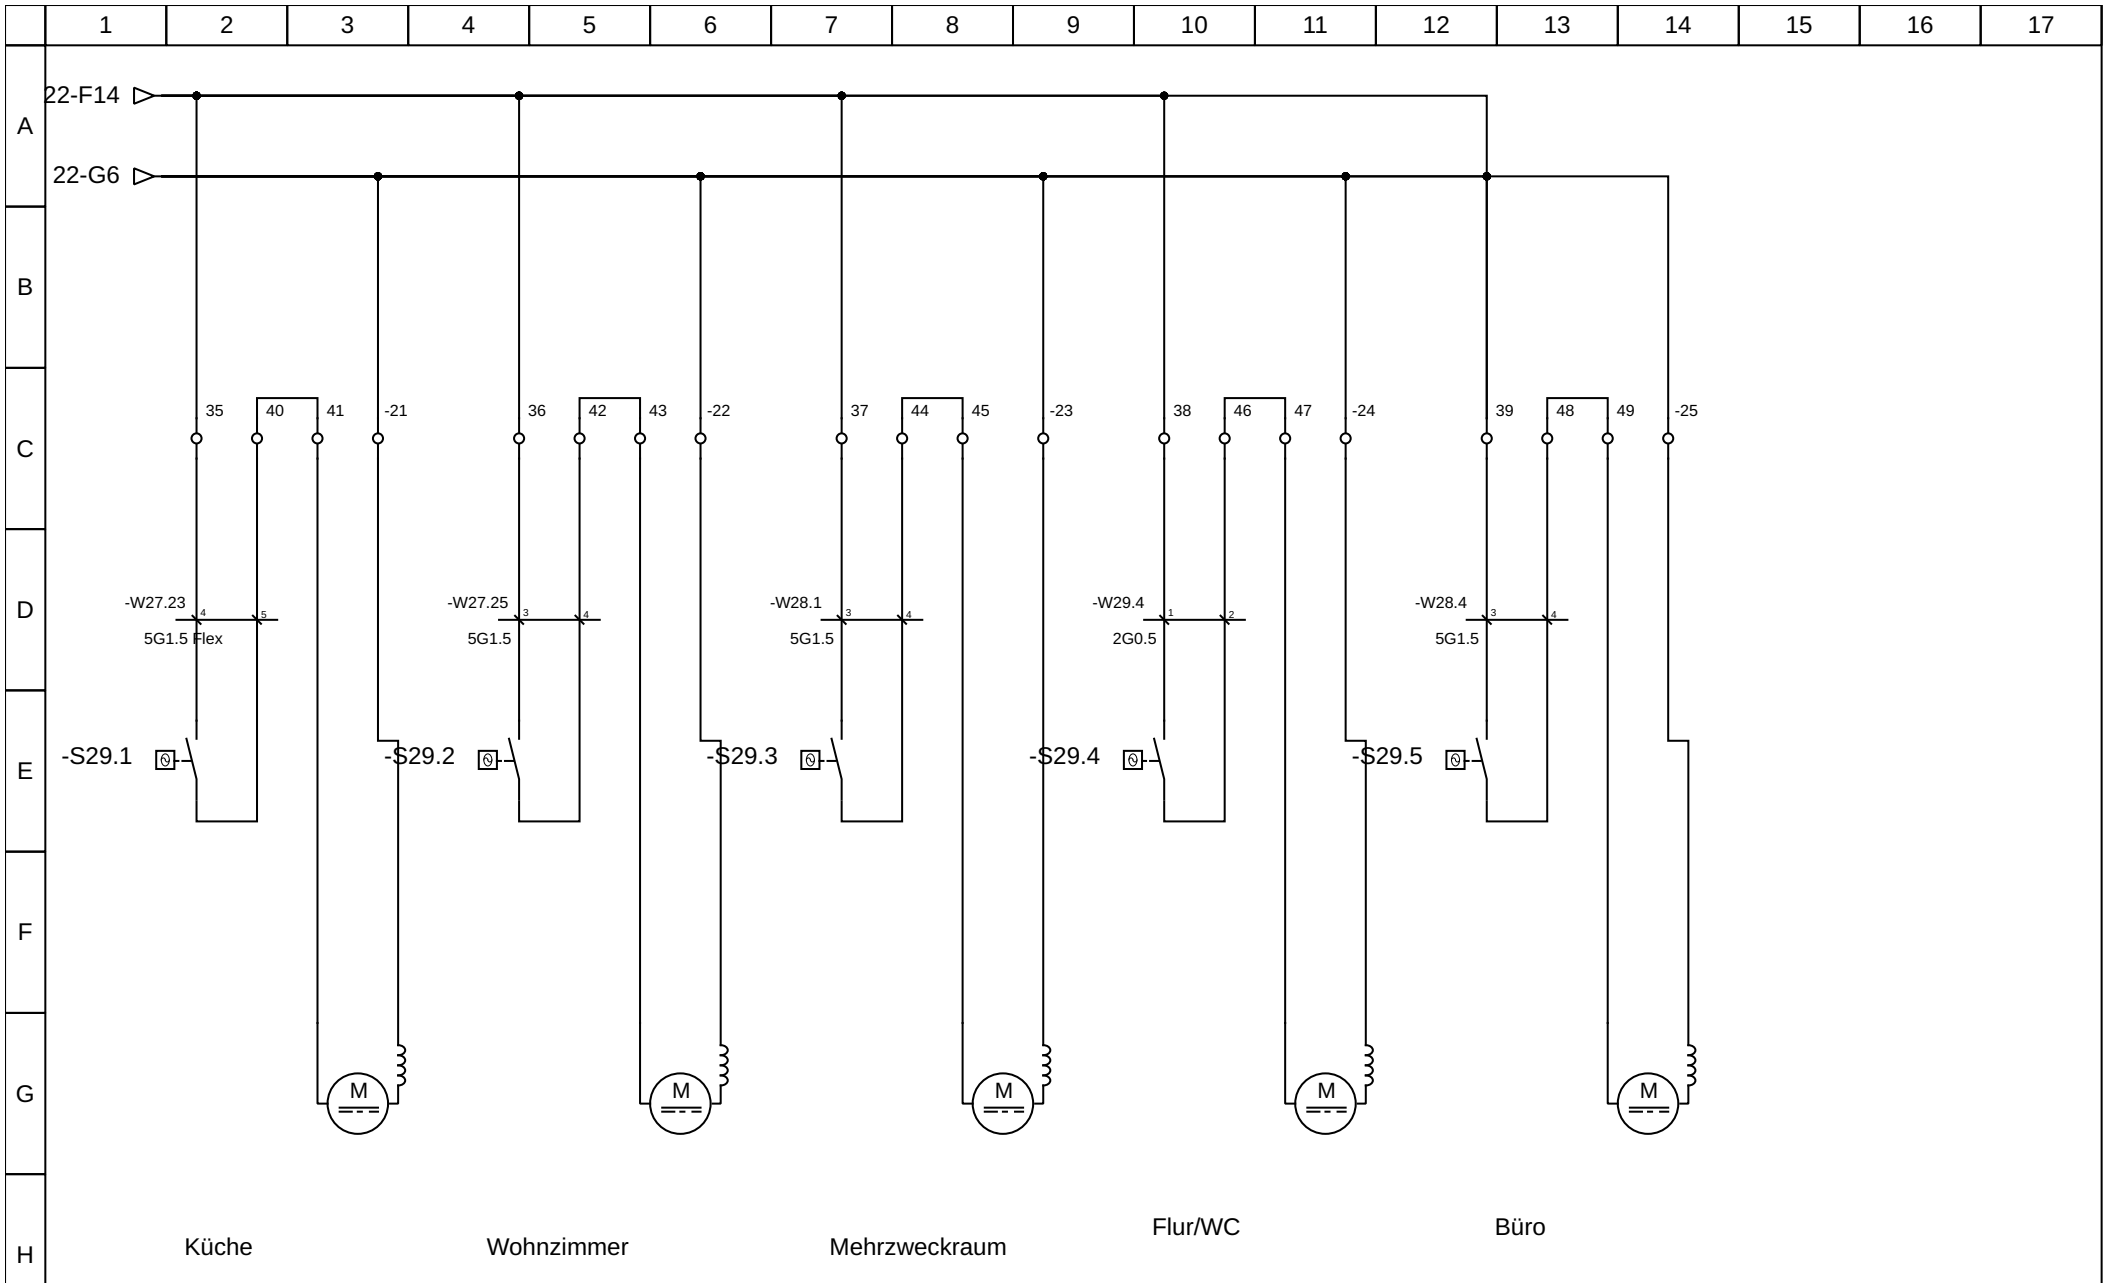



| | | |
|---|---|---|
| Autor: Entrich | Thermostate | Datei: |
| Datum: 10/16/26 | | Seite: 29/39 |

| | 1 | 2 | 3 | 4 | 5 | 6 | 7 | 8 | 9 | 10 | 11 | 12 | 13 | 14 | 15 | 16 | 17 |
|---|---|---|---|---|---|---|---|---|---|---|---|---|---|---|---|---|---|
| A | | | | | | | | | | | | | | | | | |
| B | | | | | | | | | | | | | | | | | |
| C | | | | | | | | | | | | | | | | | |
| D | | | | | | | | | | | | | | | | | |
| E | | | | | | | | | | | | | | | | | |
| F | | | | | | | | | | | | | | | | | |
| G | | | | | | | | | | | | | | | | | |
| H | | | | | | | | | | | | | | | | | |


| | | |
|---|---|---|
| Autor: Entrich | Daten | Datei: |
| Datum: 10/16/26 | | Seite: 30/39 |

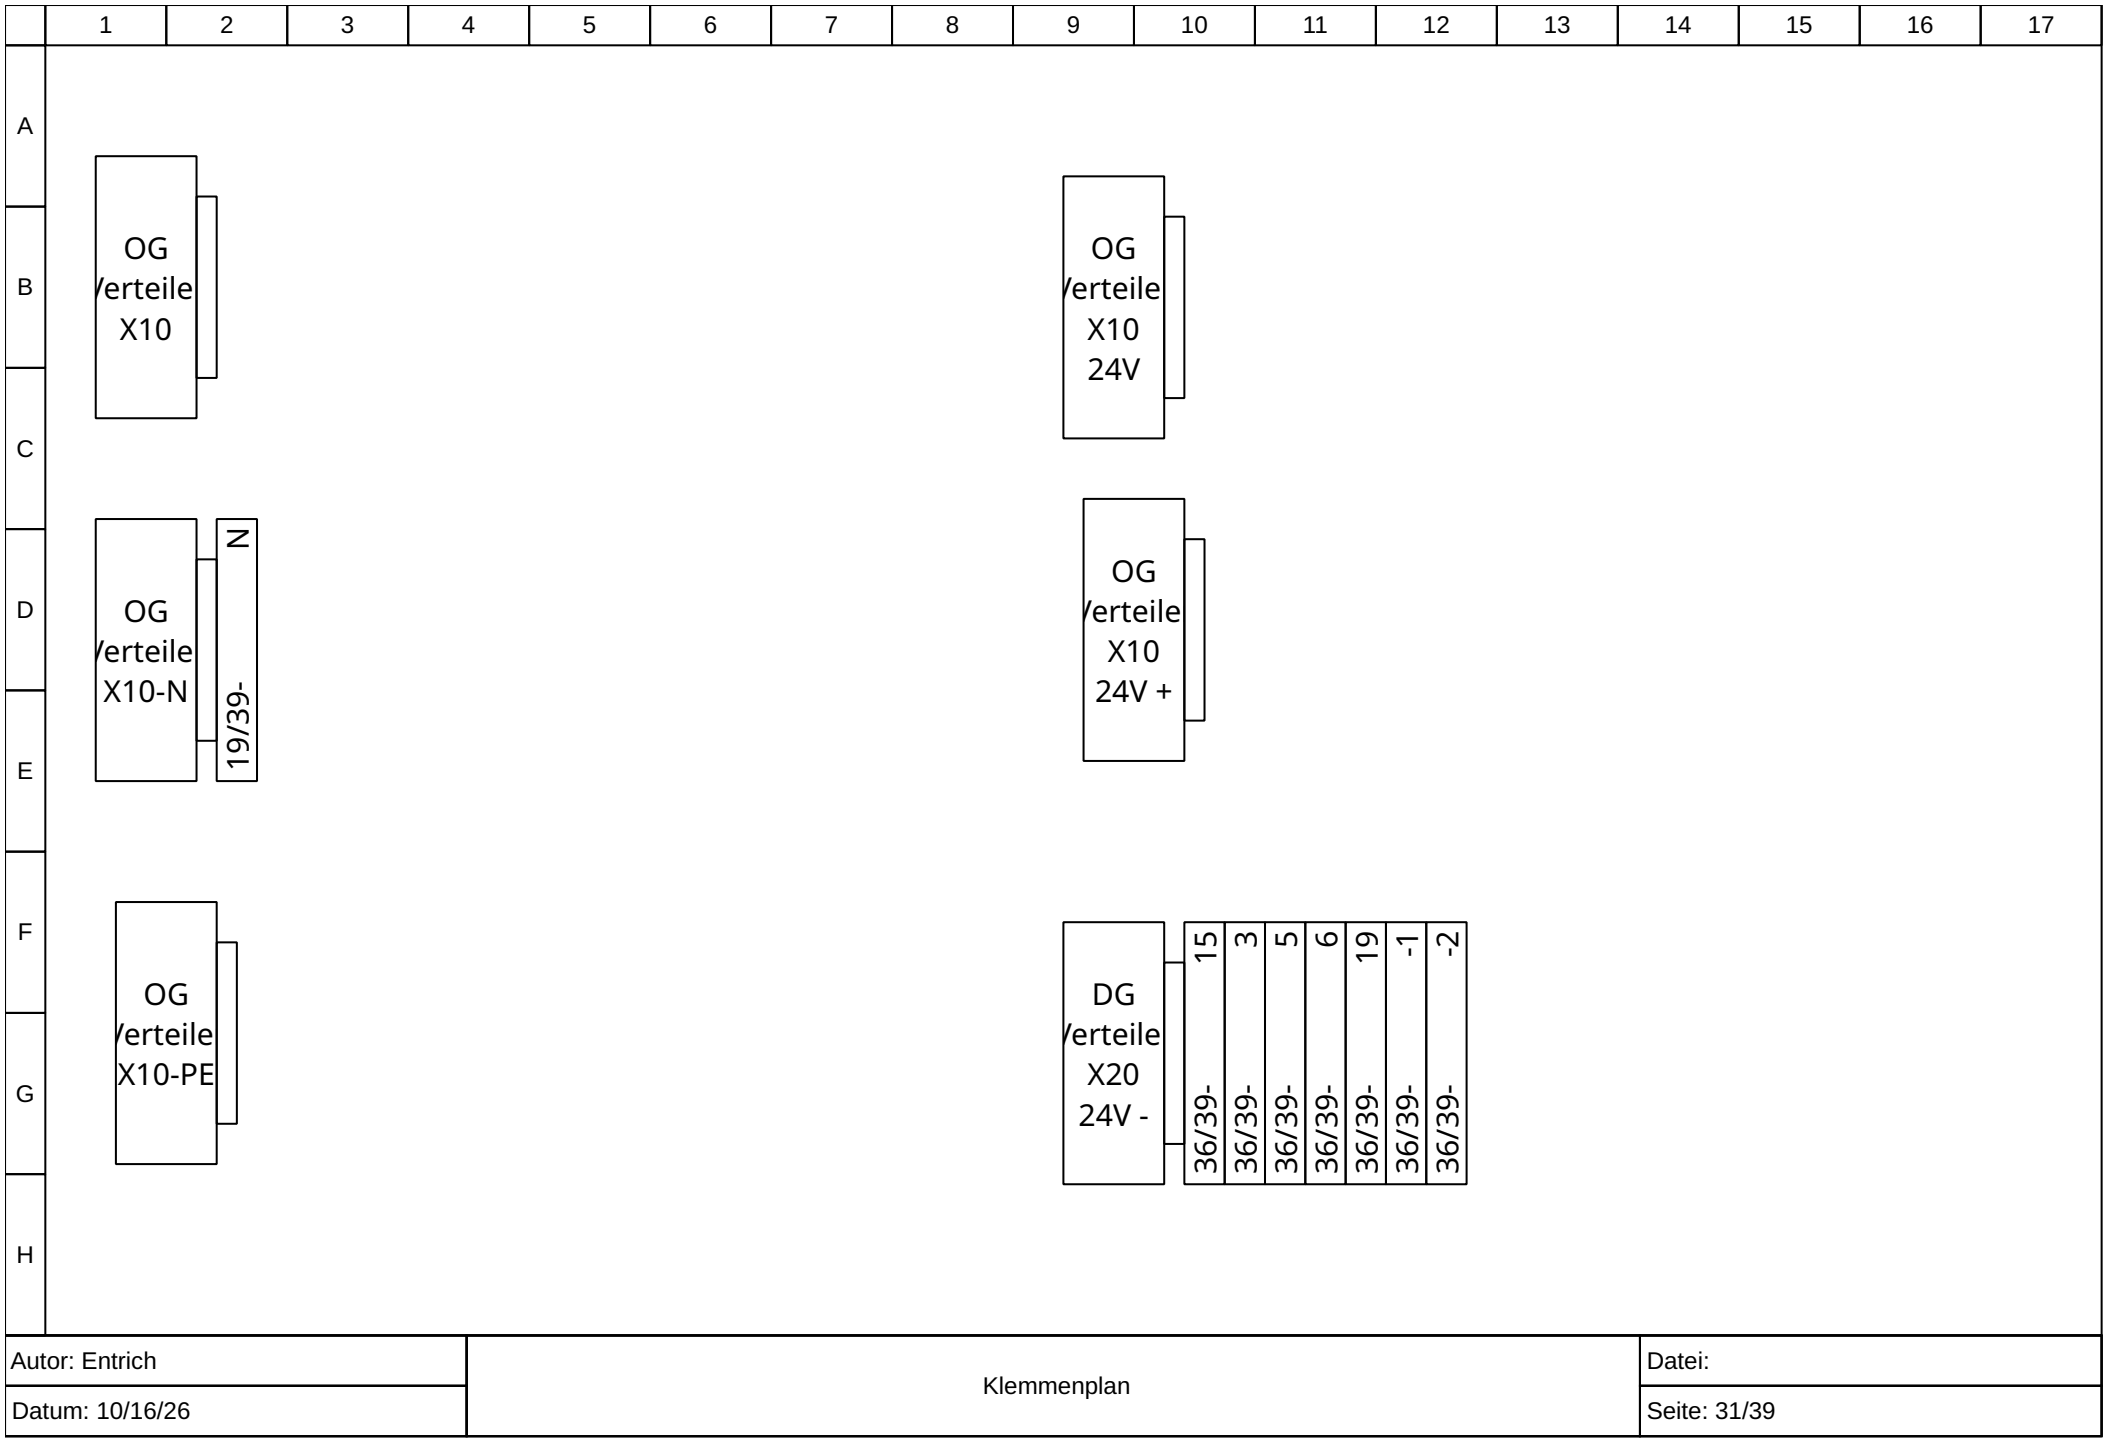



| | | |
|---|---|---|
| Autor: Entrich | Klemmenplan | Datei: |
| Datum: 10/16/26 | | Seite: 31/39 |

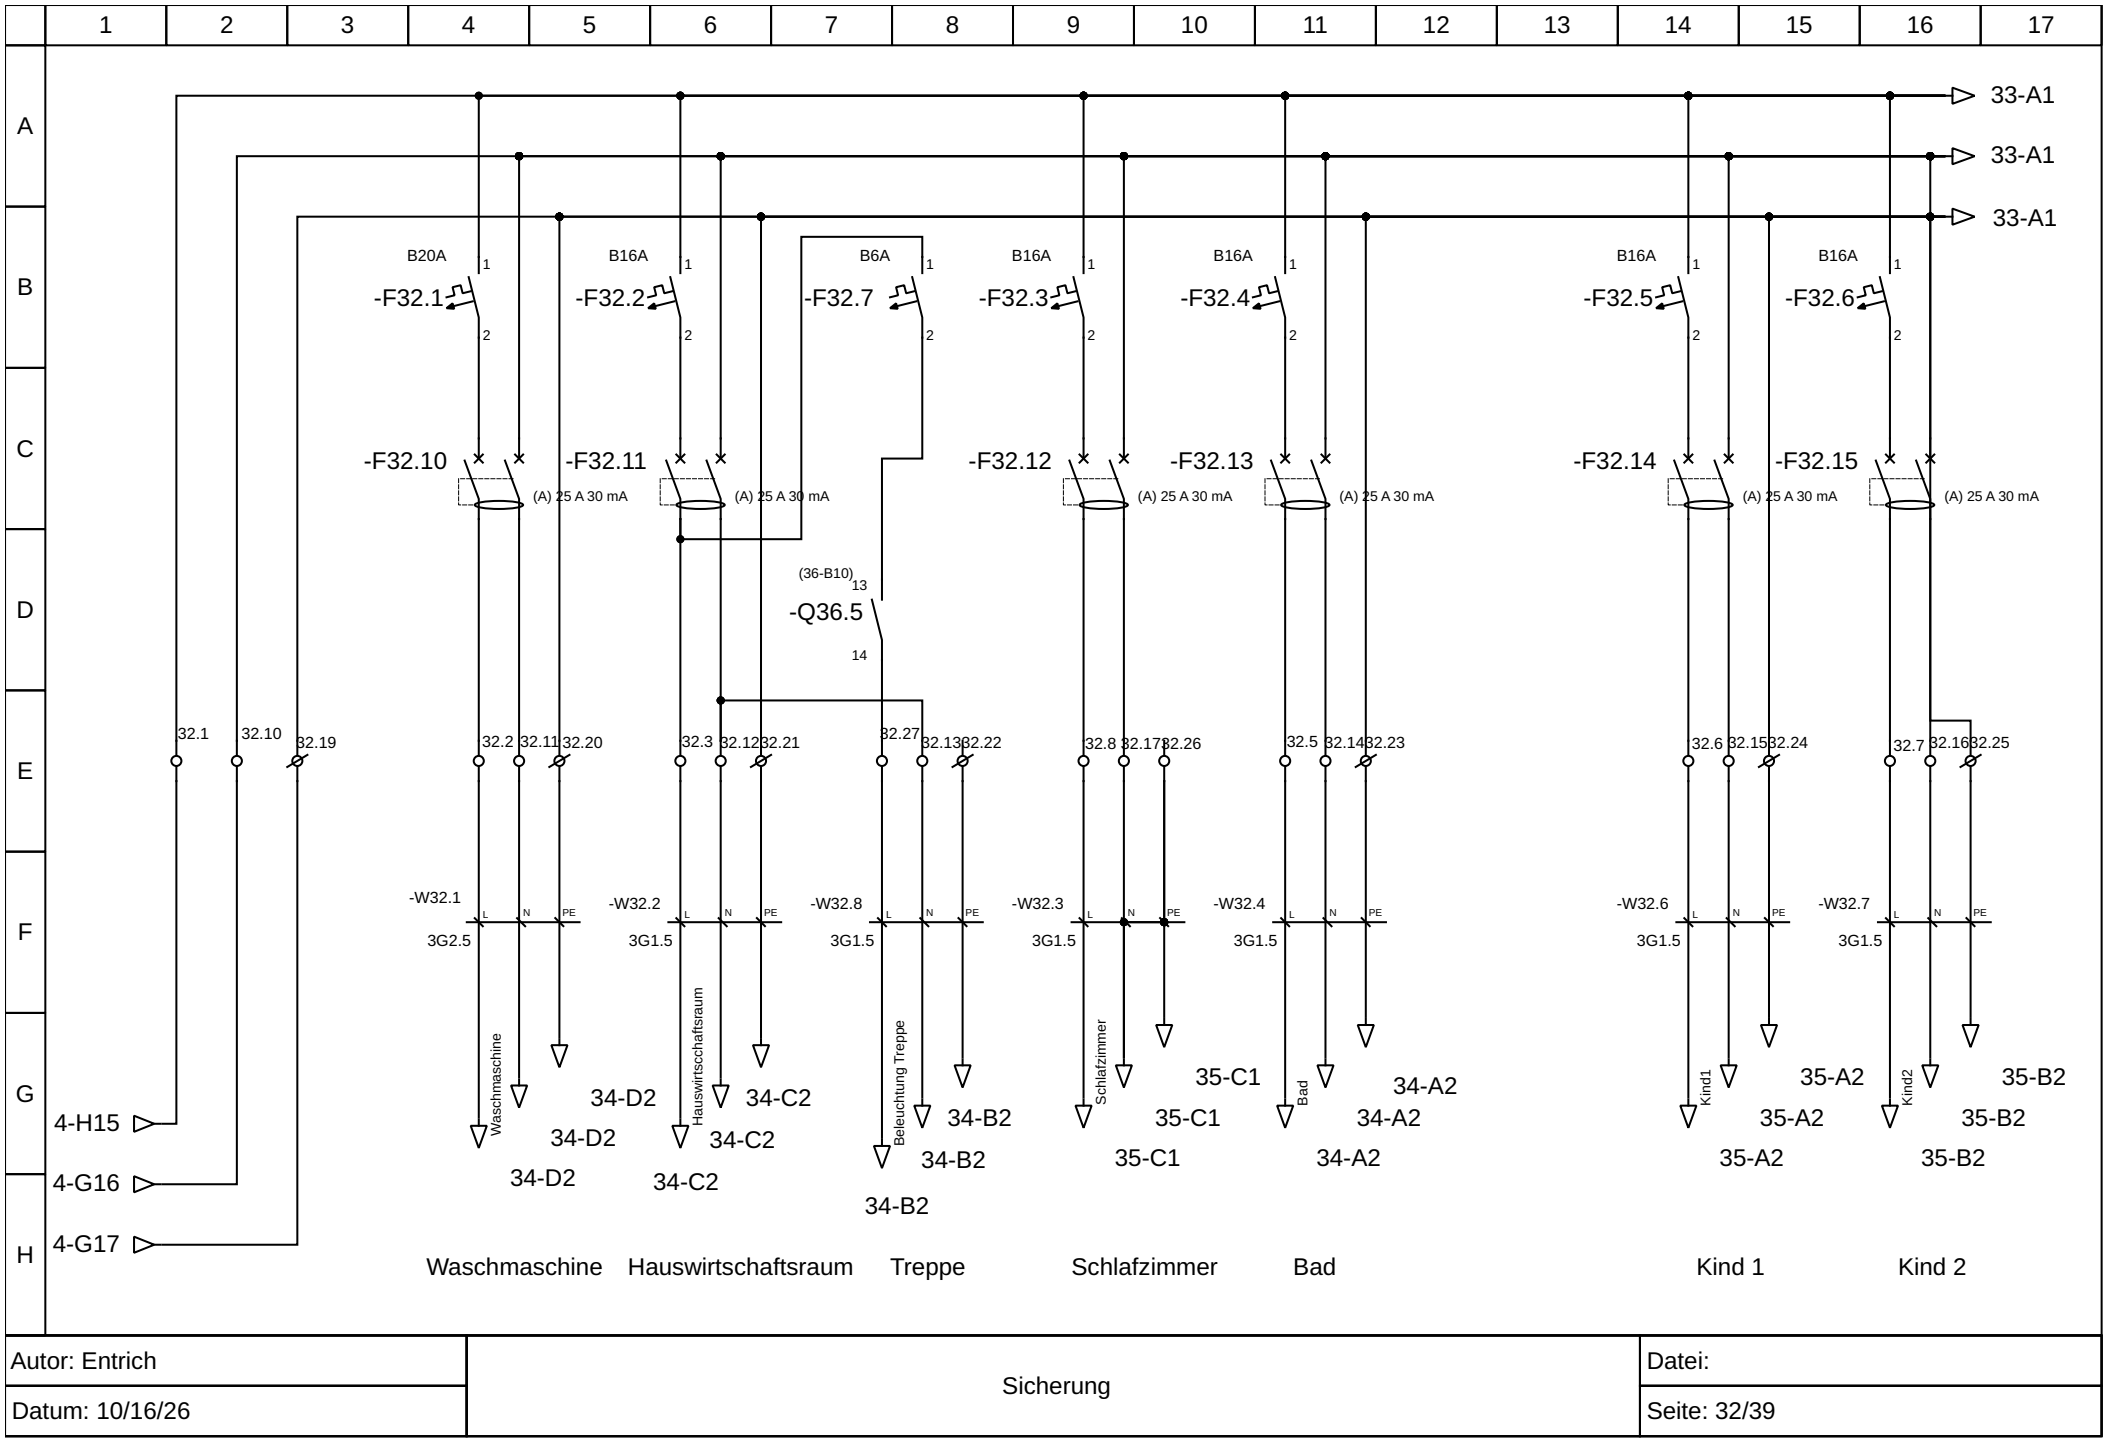



| | | |
|---|---|---|
| Autor: Entrich | Sicherung | Datei: |
| Datum: 10/16/26 | | Seite: 32/39 |

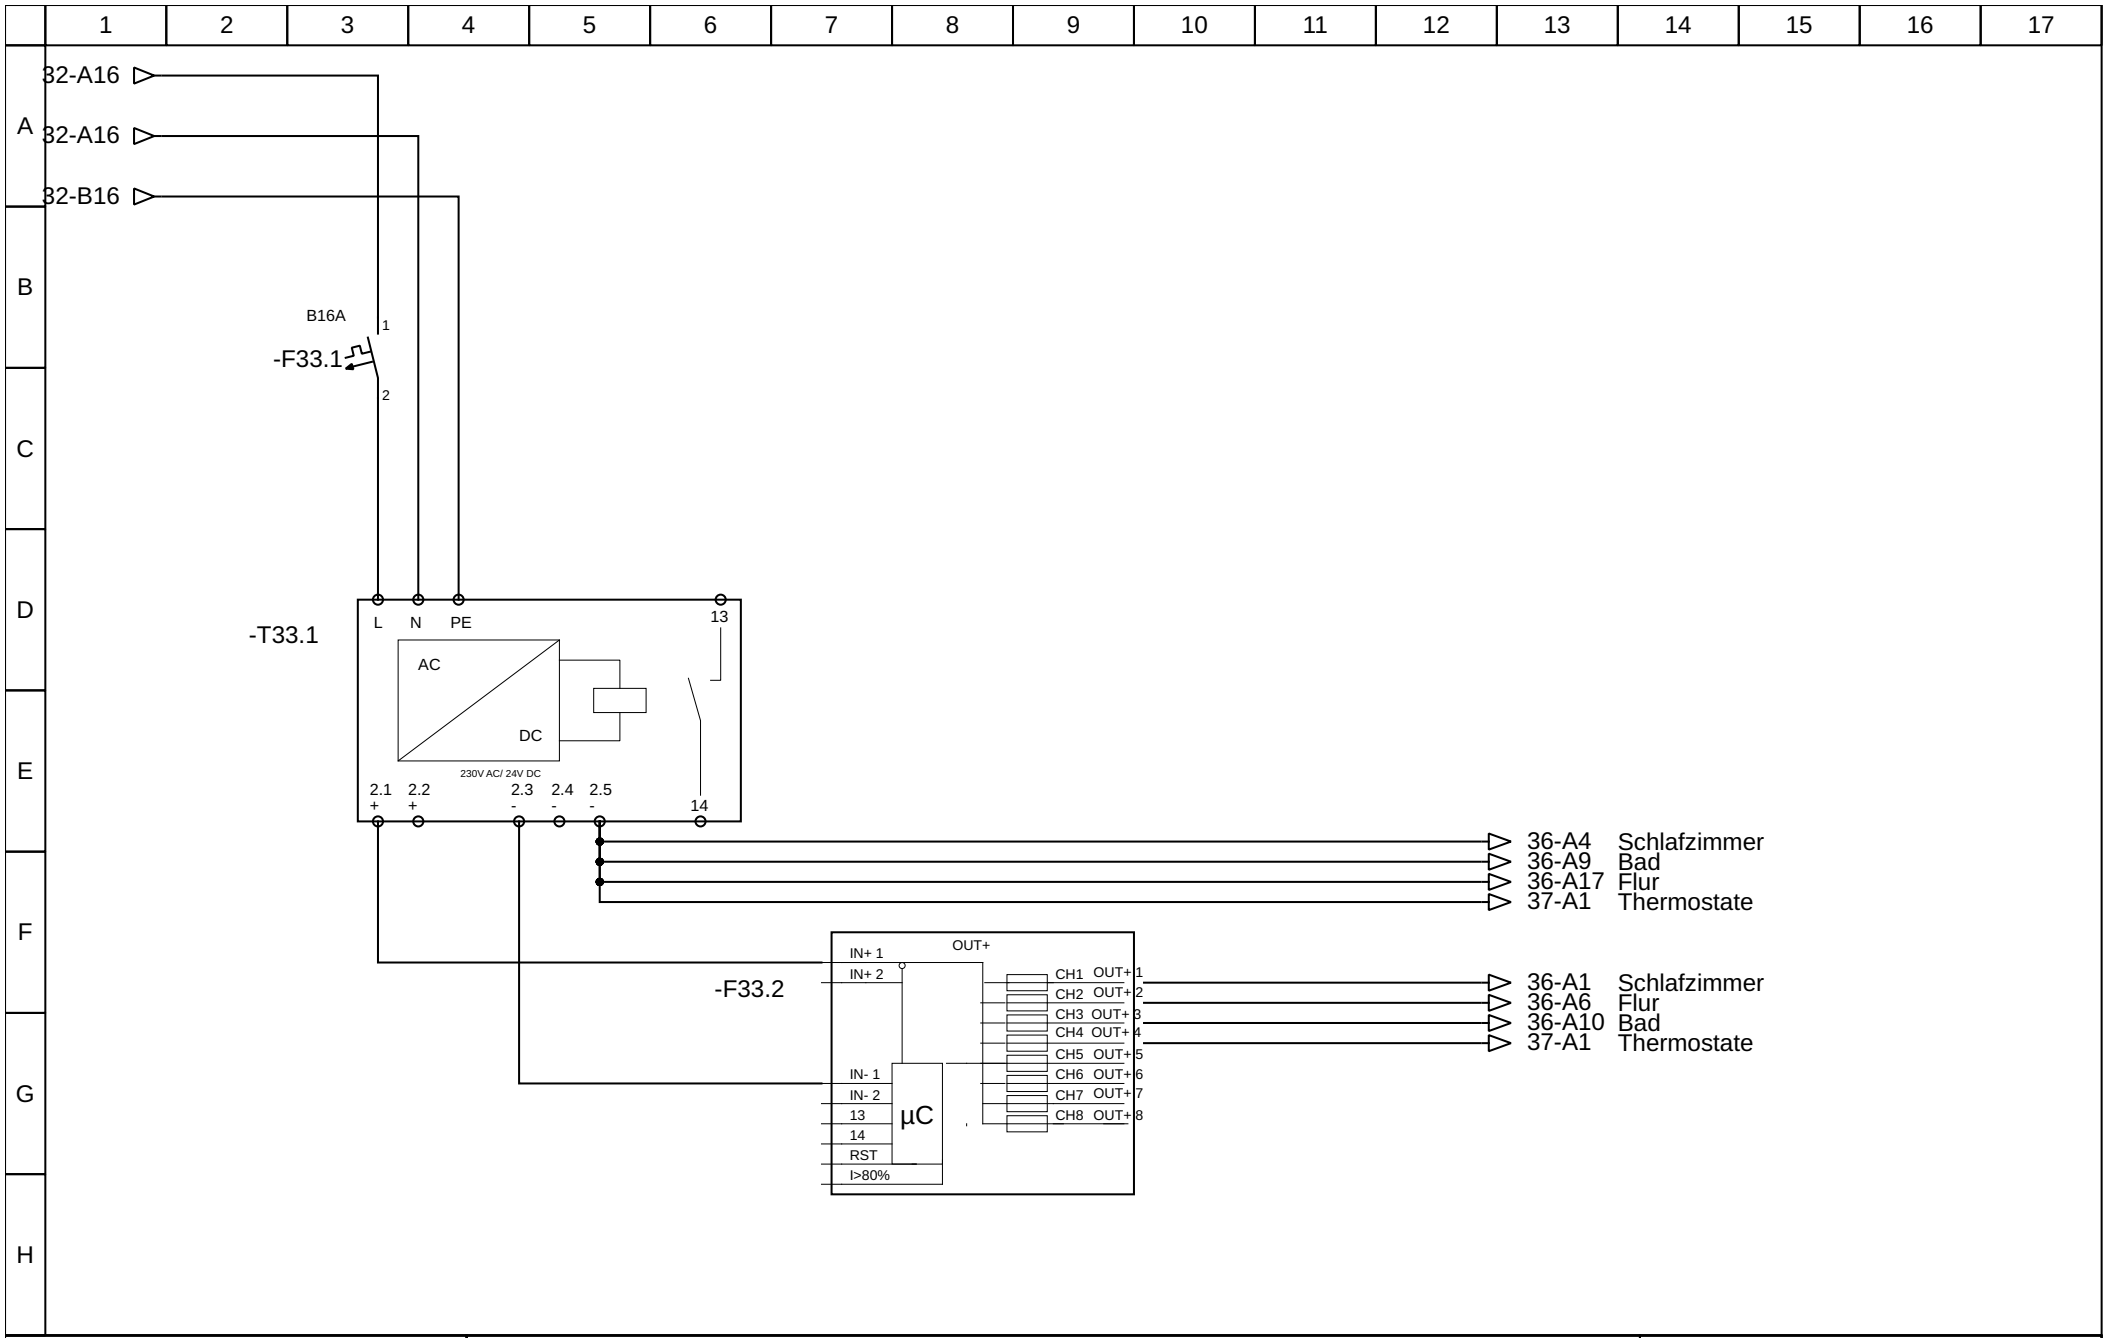



| | | |
|---|---|---|
| Autor: Entrich | Kleinspannungsversorgung | Datei: |
| Datum: 10/16/26 | | Seite: 33/39 |

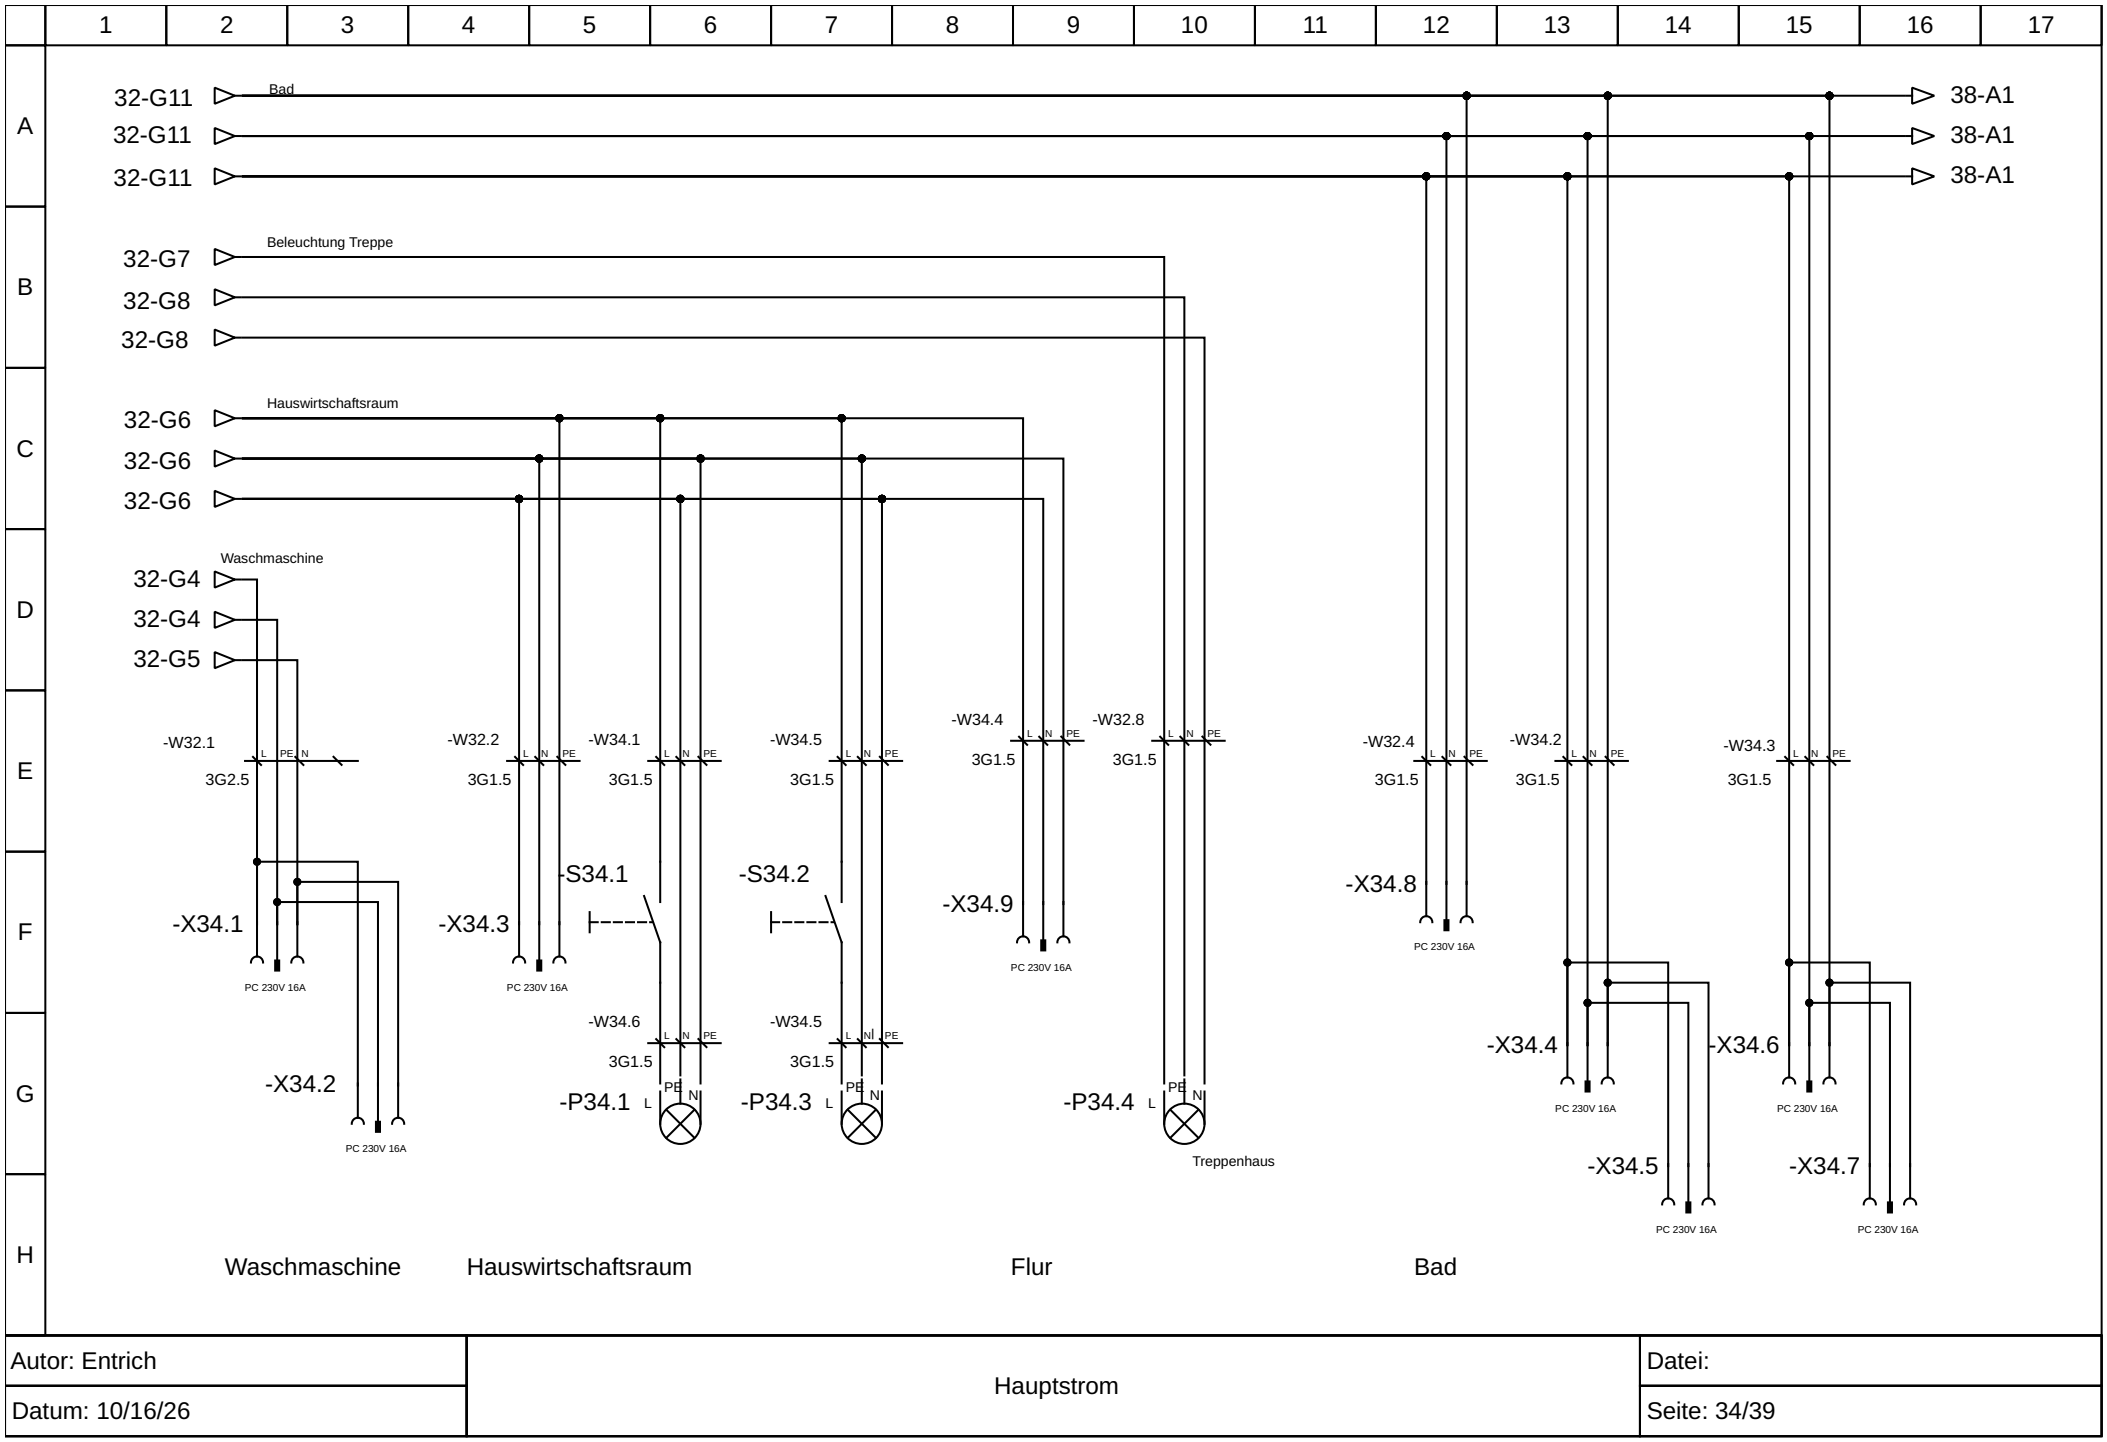



| | | |
|---|---|---|
| Autor: Entrich | Hauptstrom | Datei: |
| Datum: 10/16/26 | | Seite: 34/39 |

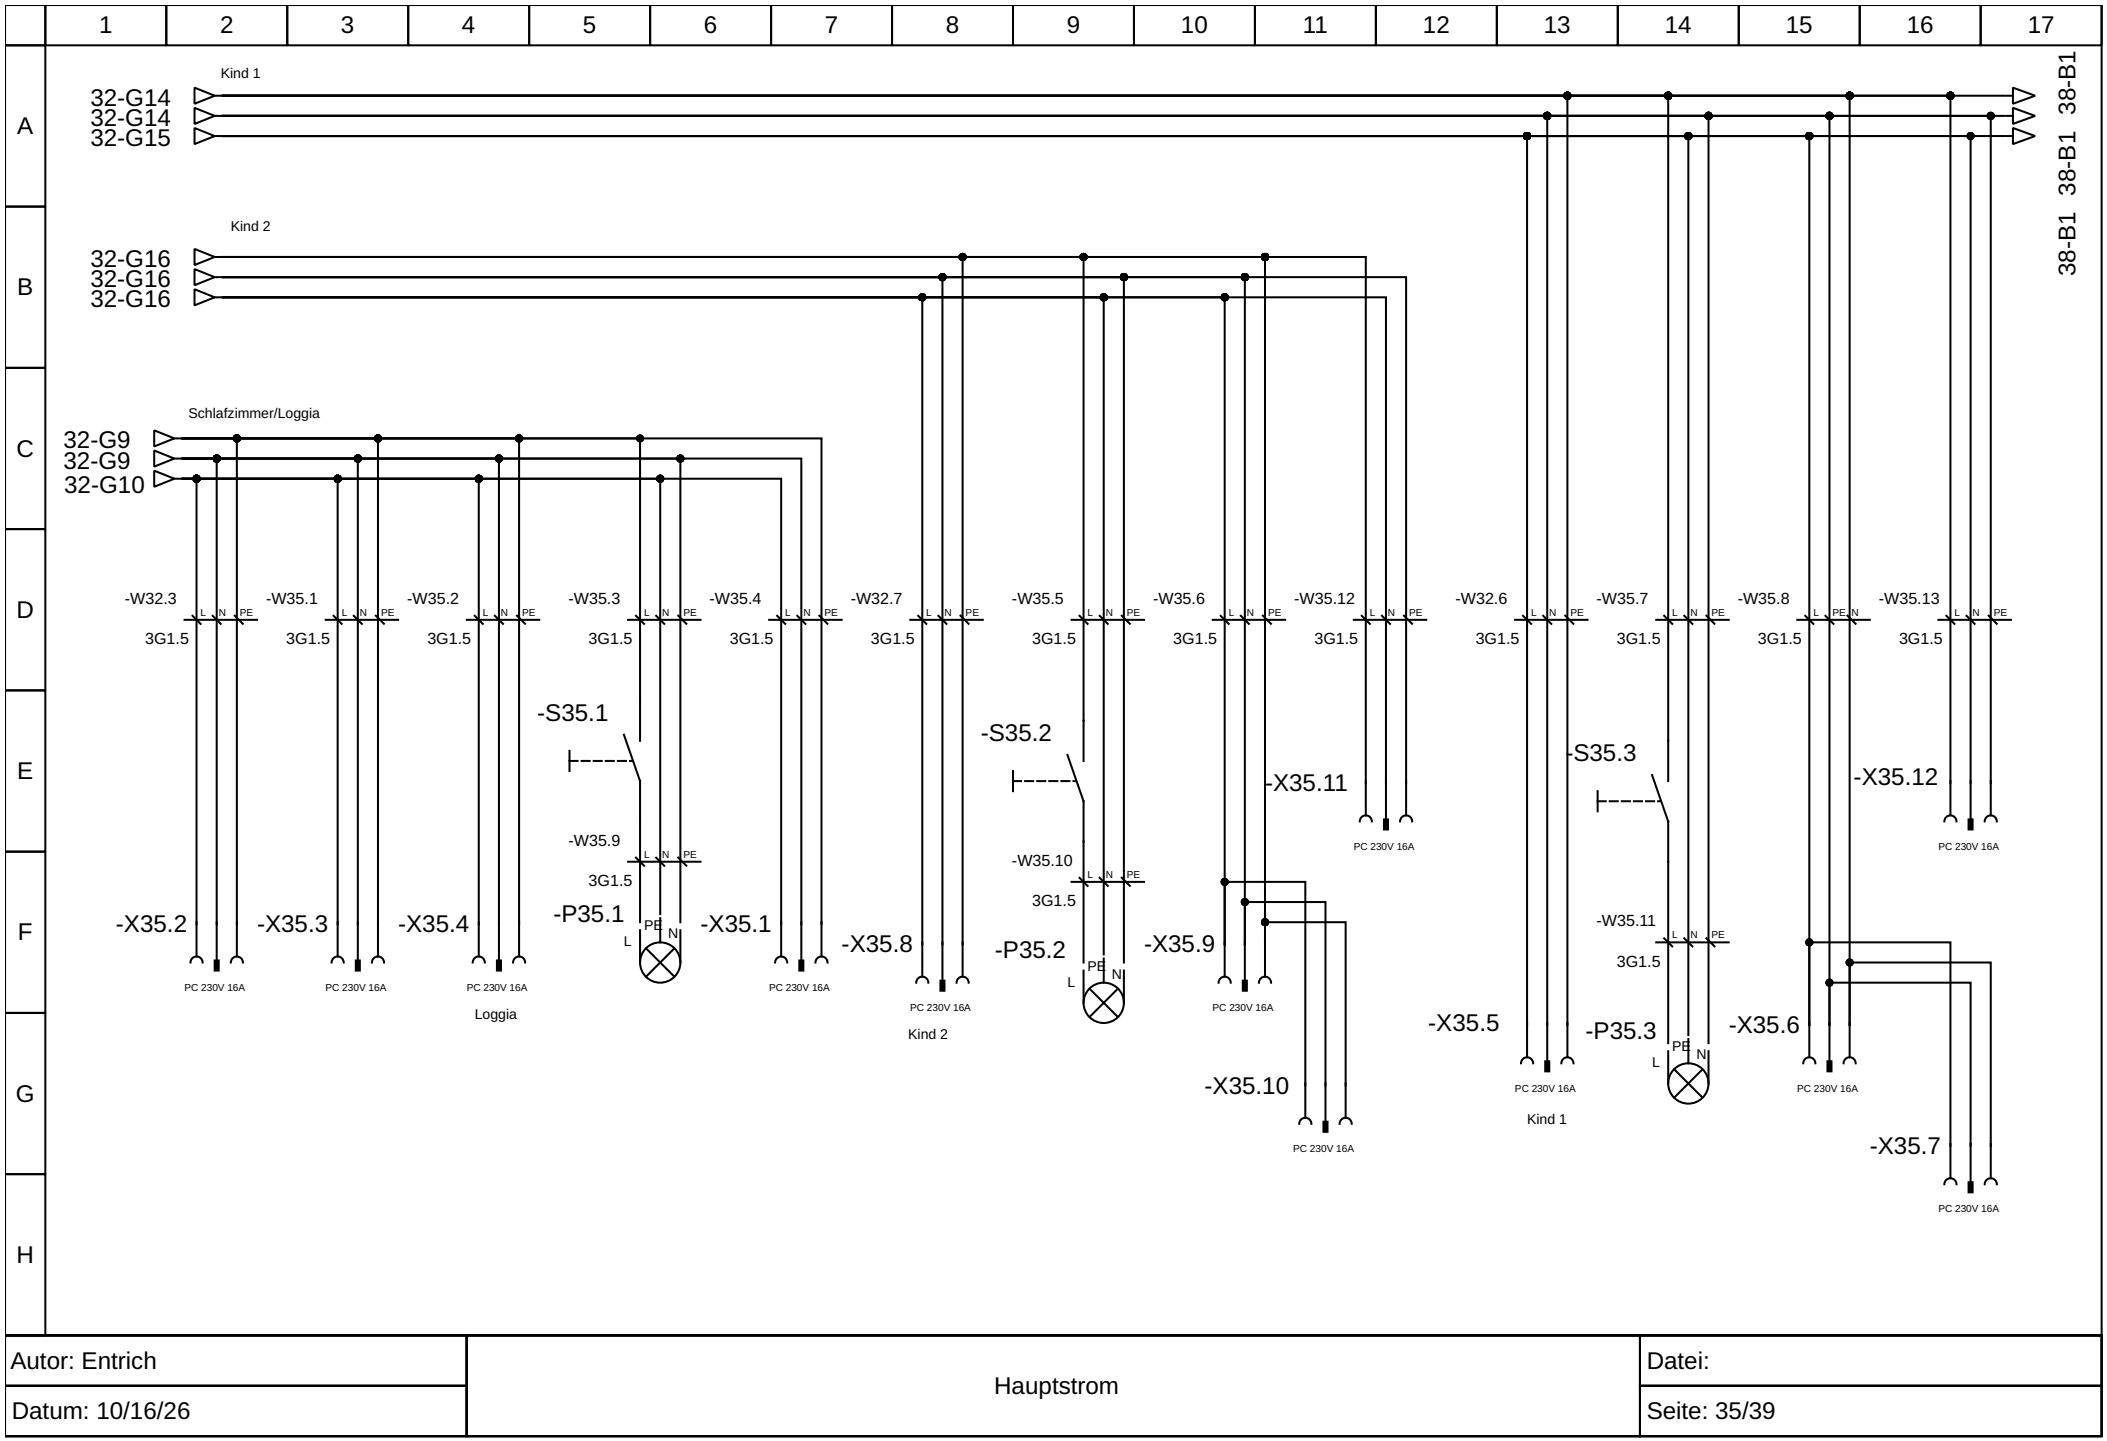



| | | |
|---|---|---|
| Autor: Entrich | Hauptstrom | Datei: |
| Datum: 10/16/26 | | Seite: 35/39 |

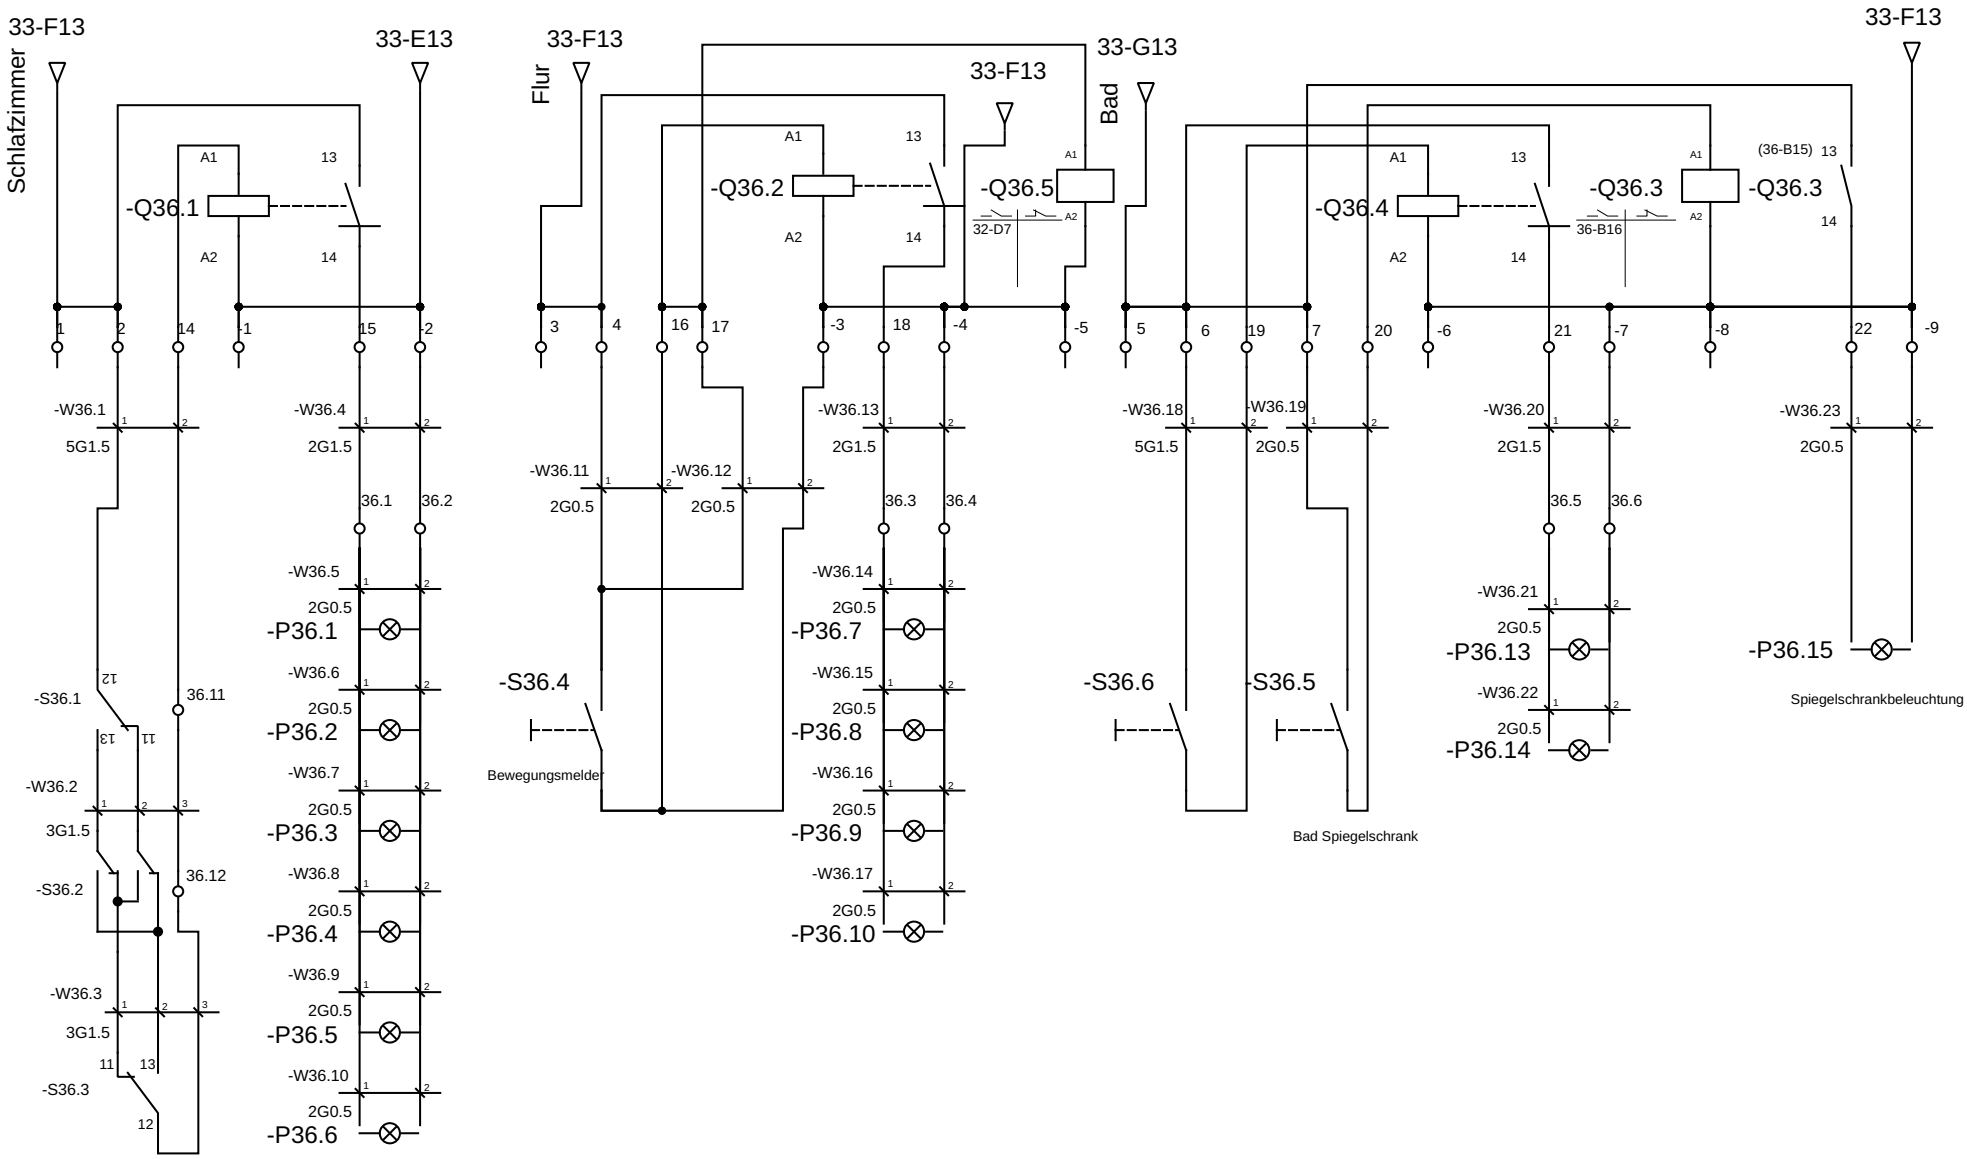



| | | |
|---|---|---|
| Autor: Entrich | Kleinspannung | Datei: |
| Datum: 10/16/26 | | Seite: 36/39 |

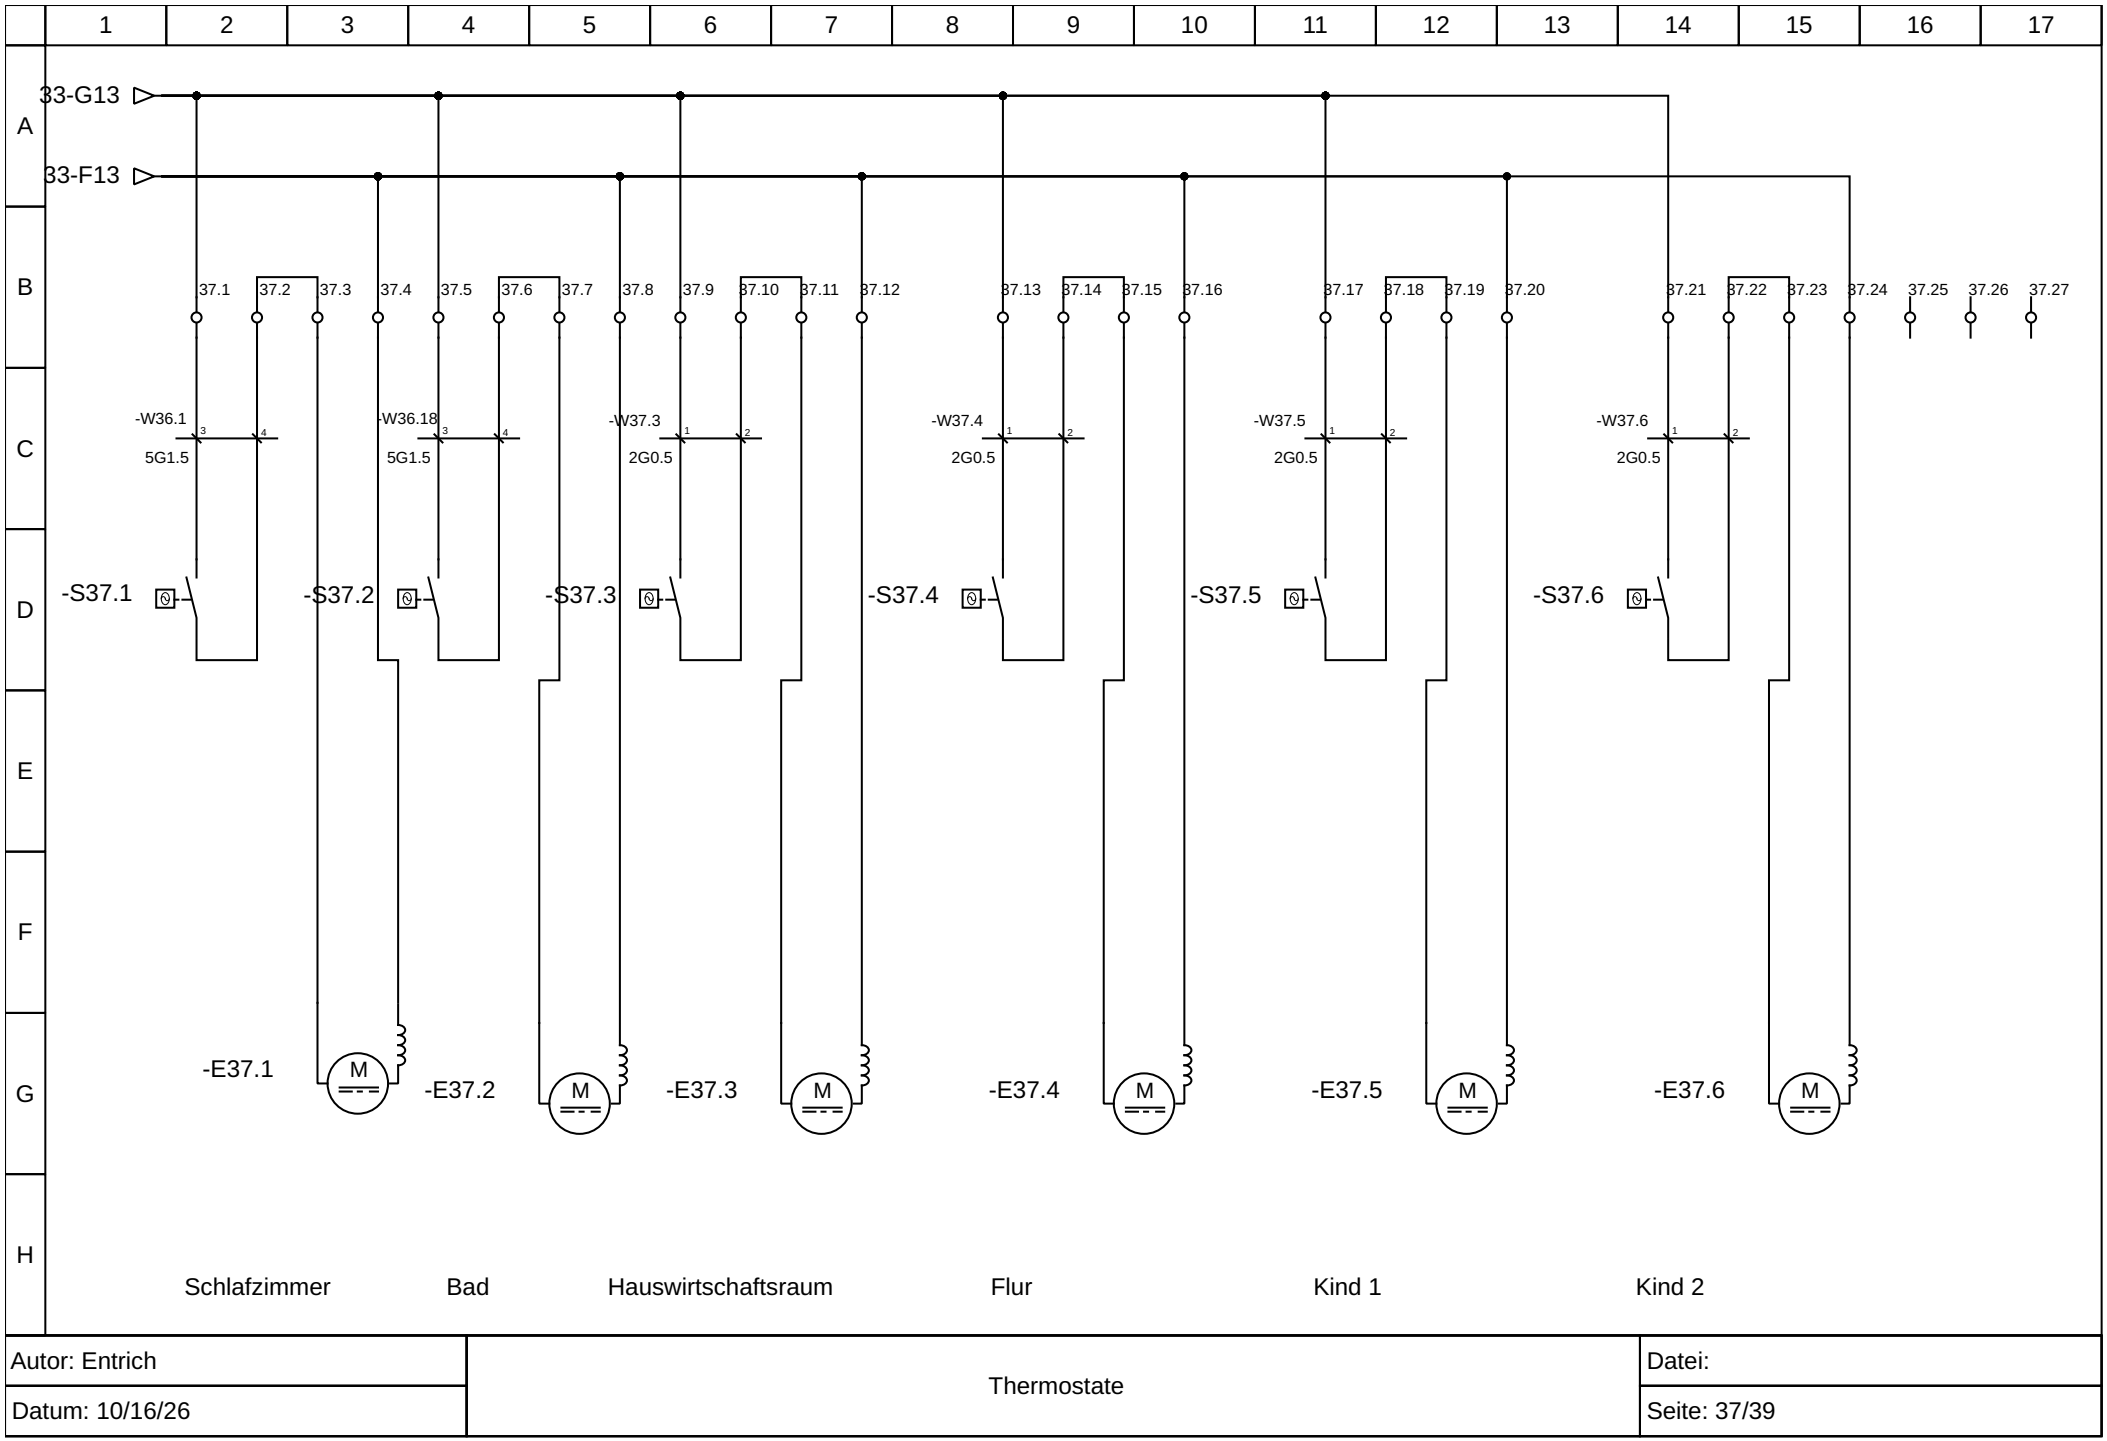


| | | |
|---|---|---|
| Autor: Entrich | Thermostate | Datei: |
| Datum: 10/16/26 | | Seite: 37/39 |

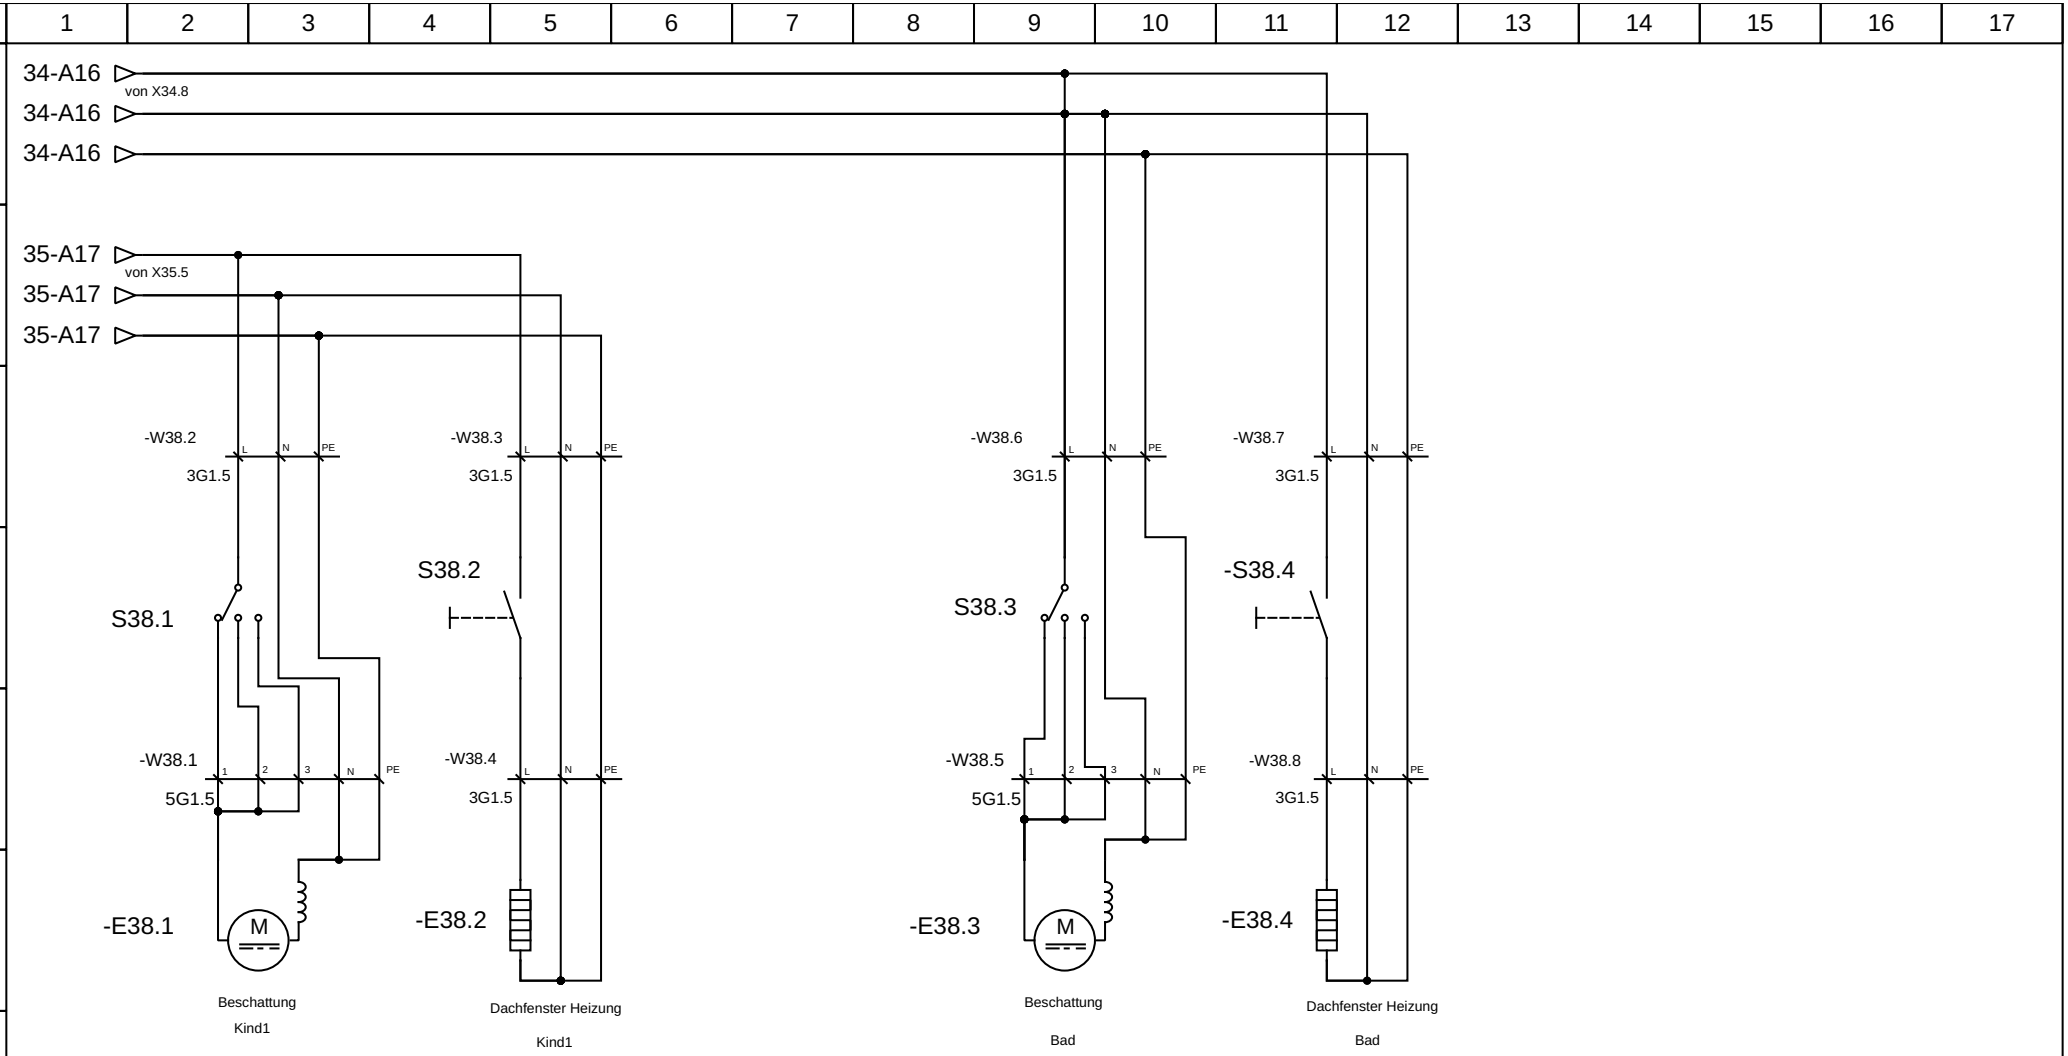


| | | |
|---|---|---|
| Autor: Entrich | Dachfenster | Datei: |
| Datum: 10/16/26 | | Seite: 38/39 |

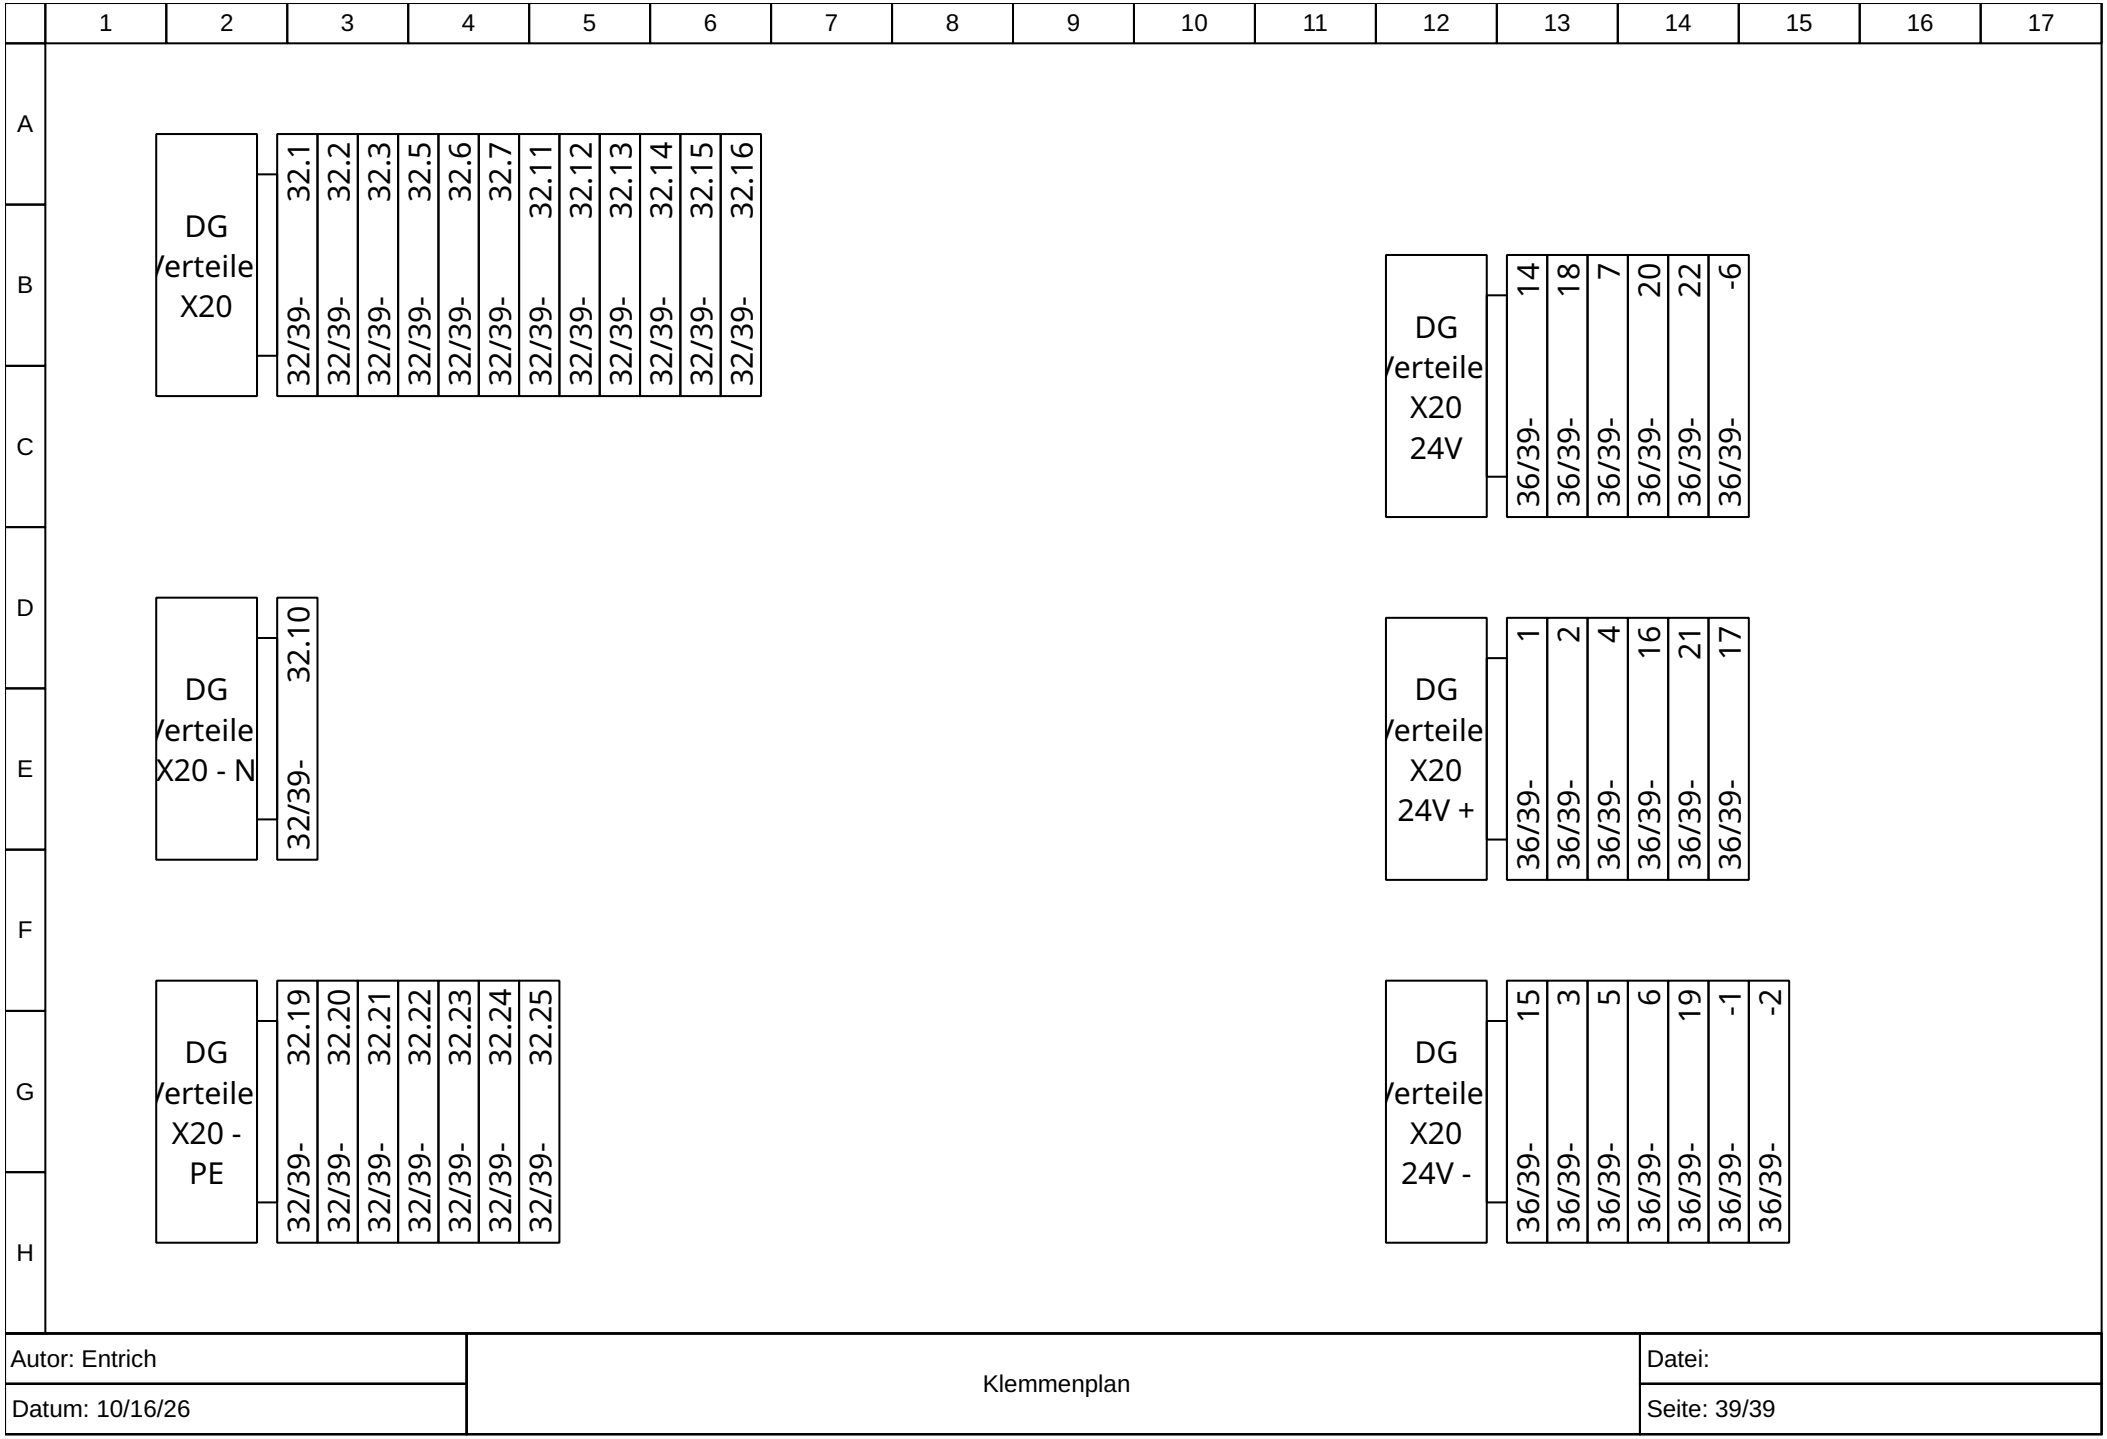


| | | |
|---|---|---|
| Autor: Entrich | Klemmenplan | Datei: |
| Datum: 10/16/26 | | Seite: 39/39 |