






	1	2	3	4	5	6	7	8	9	10	11	12	13	14	15	16	17	18
A																		
	Titel					Anlage (=)		Ort (+)				Foliennummer		Seite		Revisionsindex		
	Inhaltsverzeichnis											1/12		1				
	Hauptversorgung					EG		Technikraum				2/12		2		01		
B	Heizung					EG		Wärmepump				3/12		3		01		
	Sicherung					EG		Verteiler				4/12		4		01		
	Sicherung und Kleinspannungversorgung					EG		Verteiler				5/12		5		01		
C	Hauptstrom Küche					EG		Küche				6/12		6		01		
	Hauptstrom					EG		WC Eingang Flur Bad				7/12		7		01		
	Hauptstrom					EG		Wohnzimmer Schlafzimmer Terasse				8/12		8		01		
	Kleinspannung					EG		Küche Wohnzimmer Schlafzimmer Bad				9/12		9		01		
D	Kleinspannung					EG		Flur WC Eingang				10/12		10		01		
	Daten					EG		Verteiler Wohnzimmer				11/12		11		01		
	Klemmenplan					EG		Verteiler				12/12		12		01		
E																		
F																		
G																		
H																		
Autor: Entrich					Inhaltsverzeichnis										Datei:			
Datum:															Seite: 1/12			

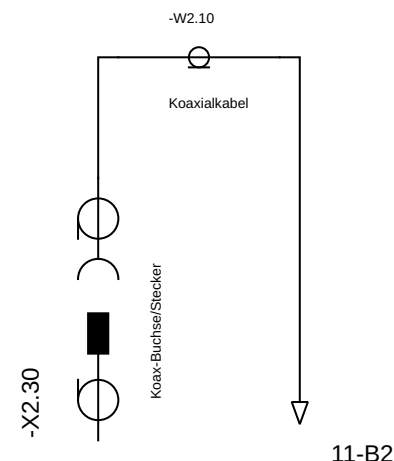


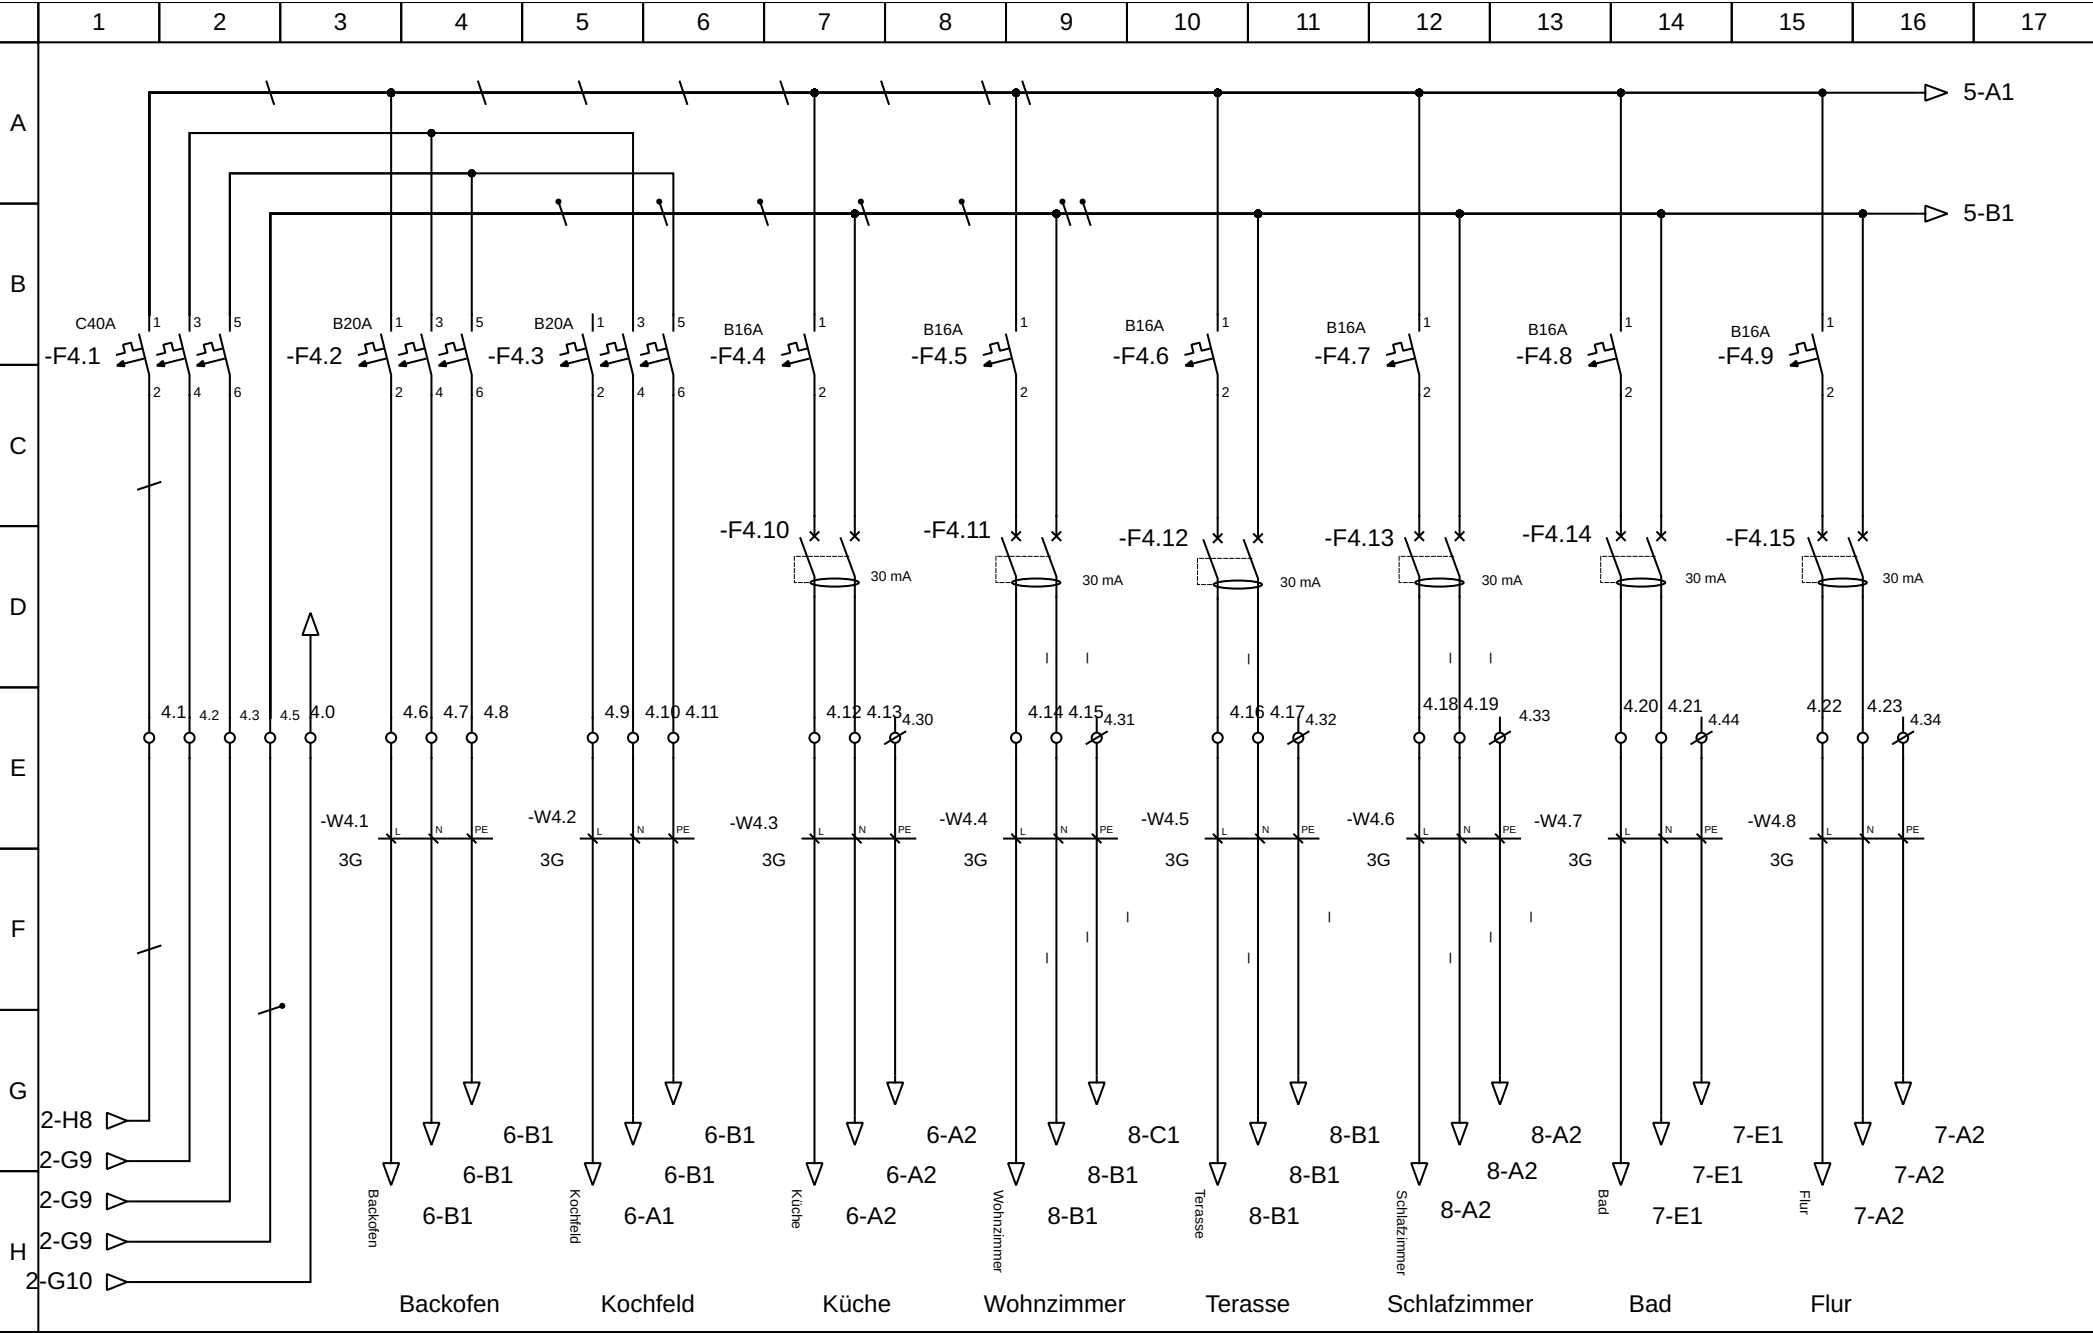


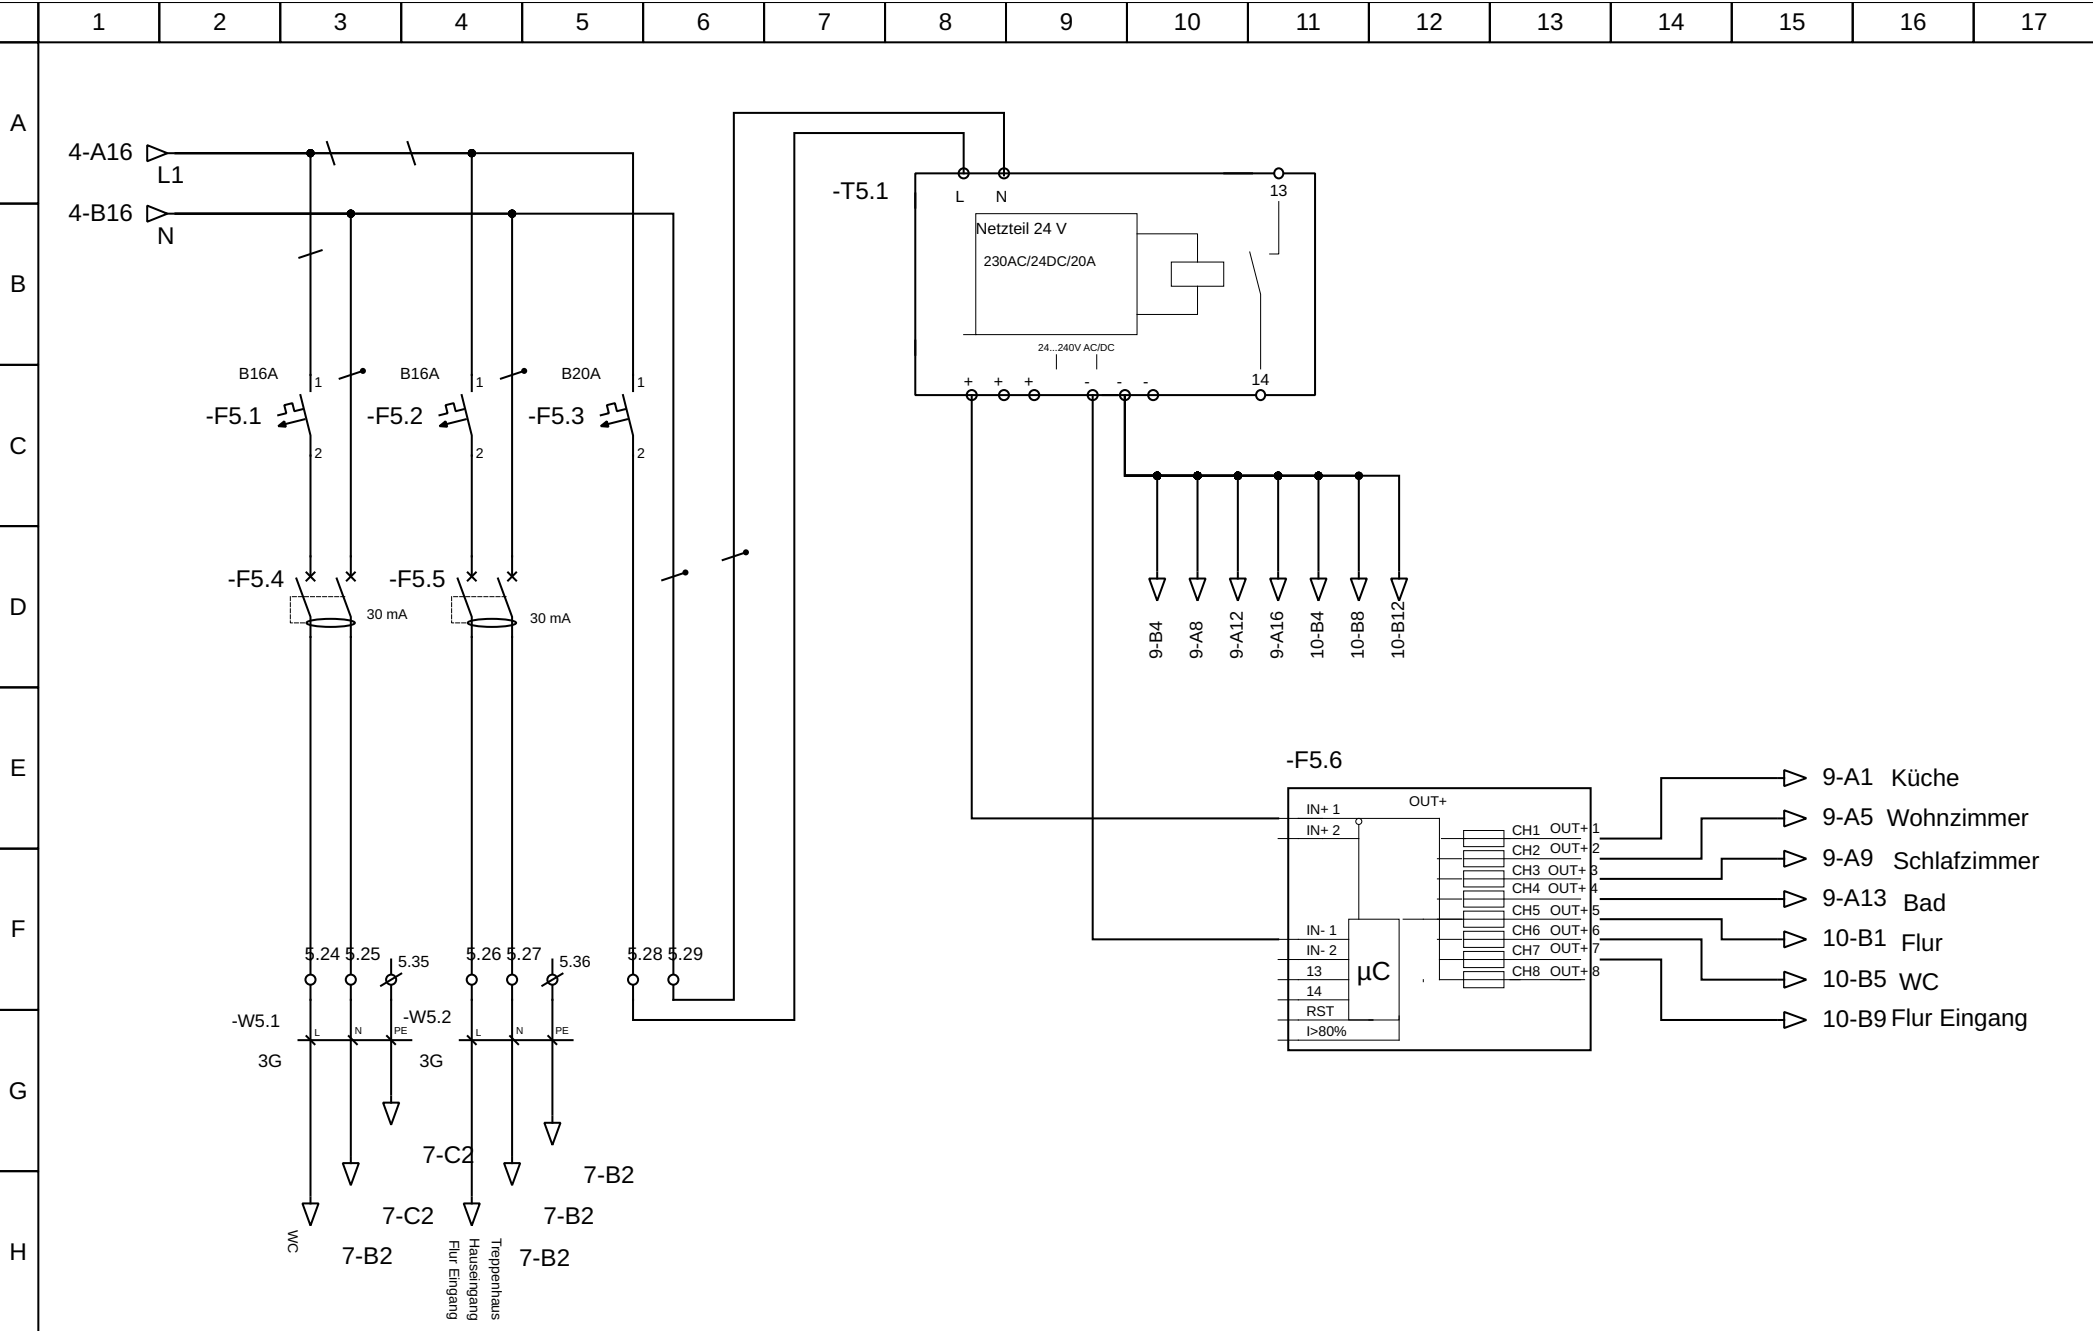

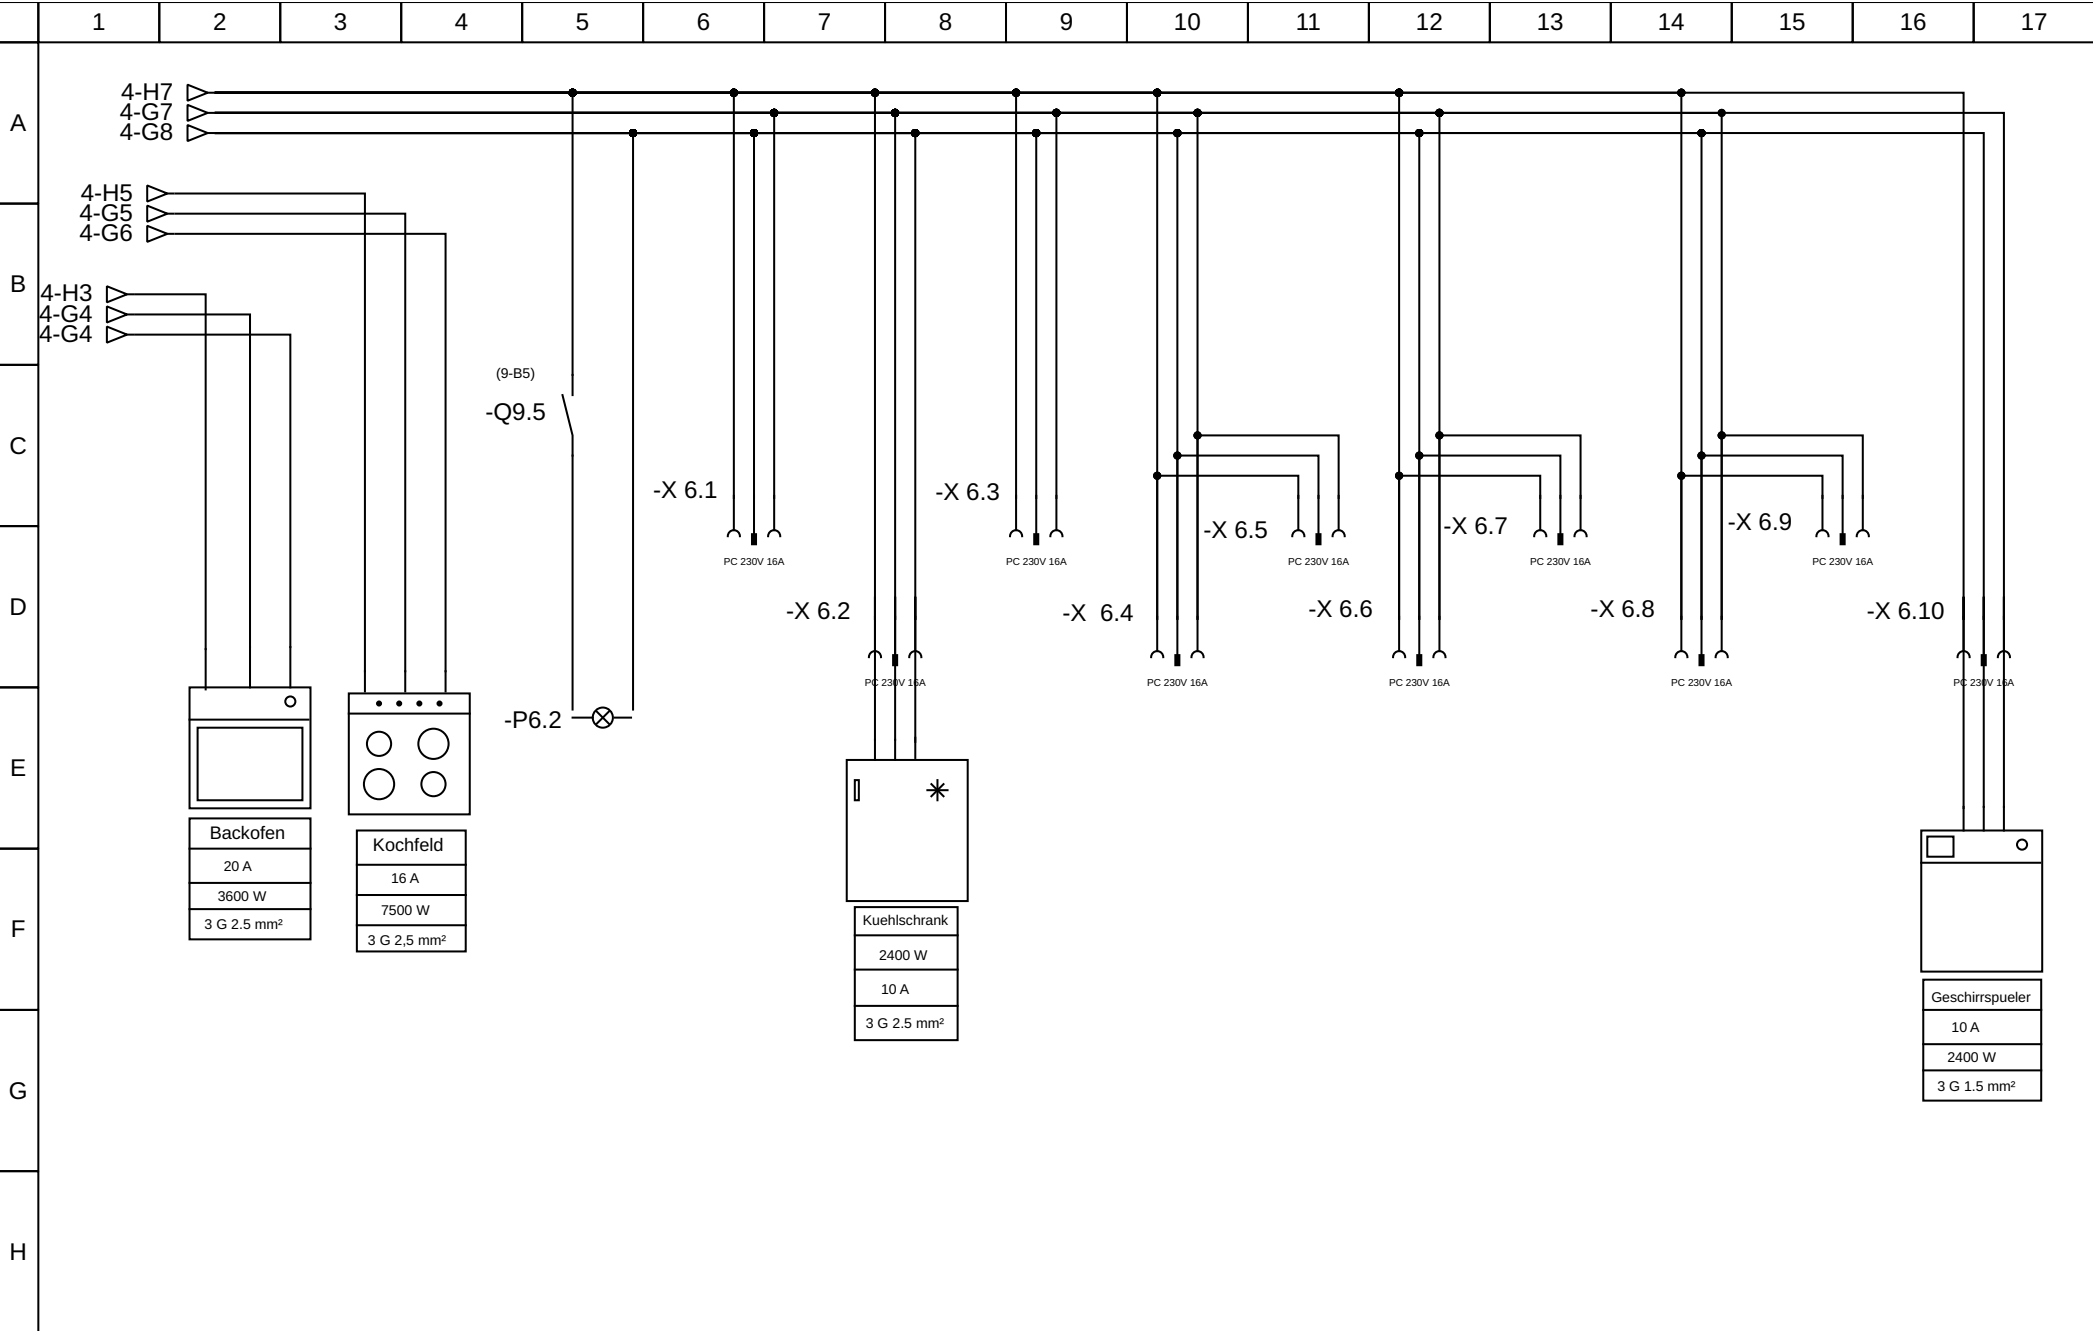

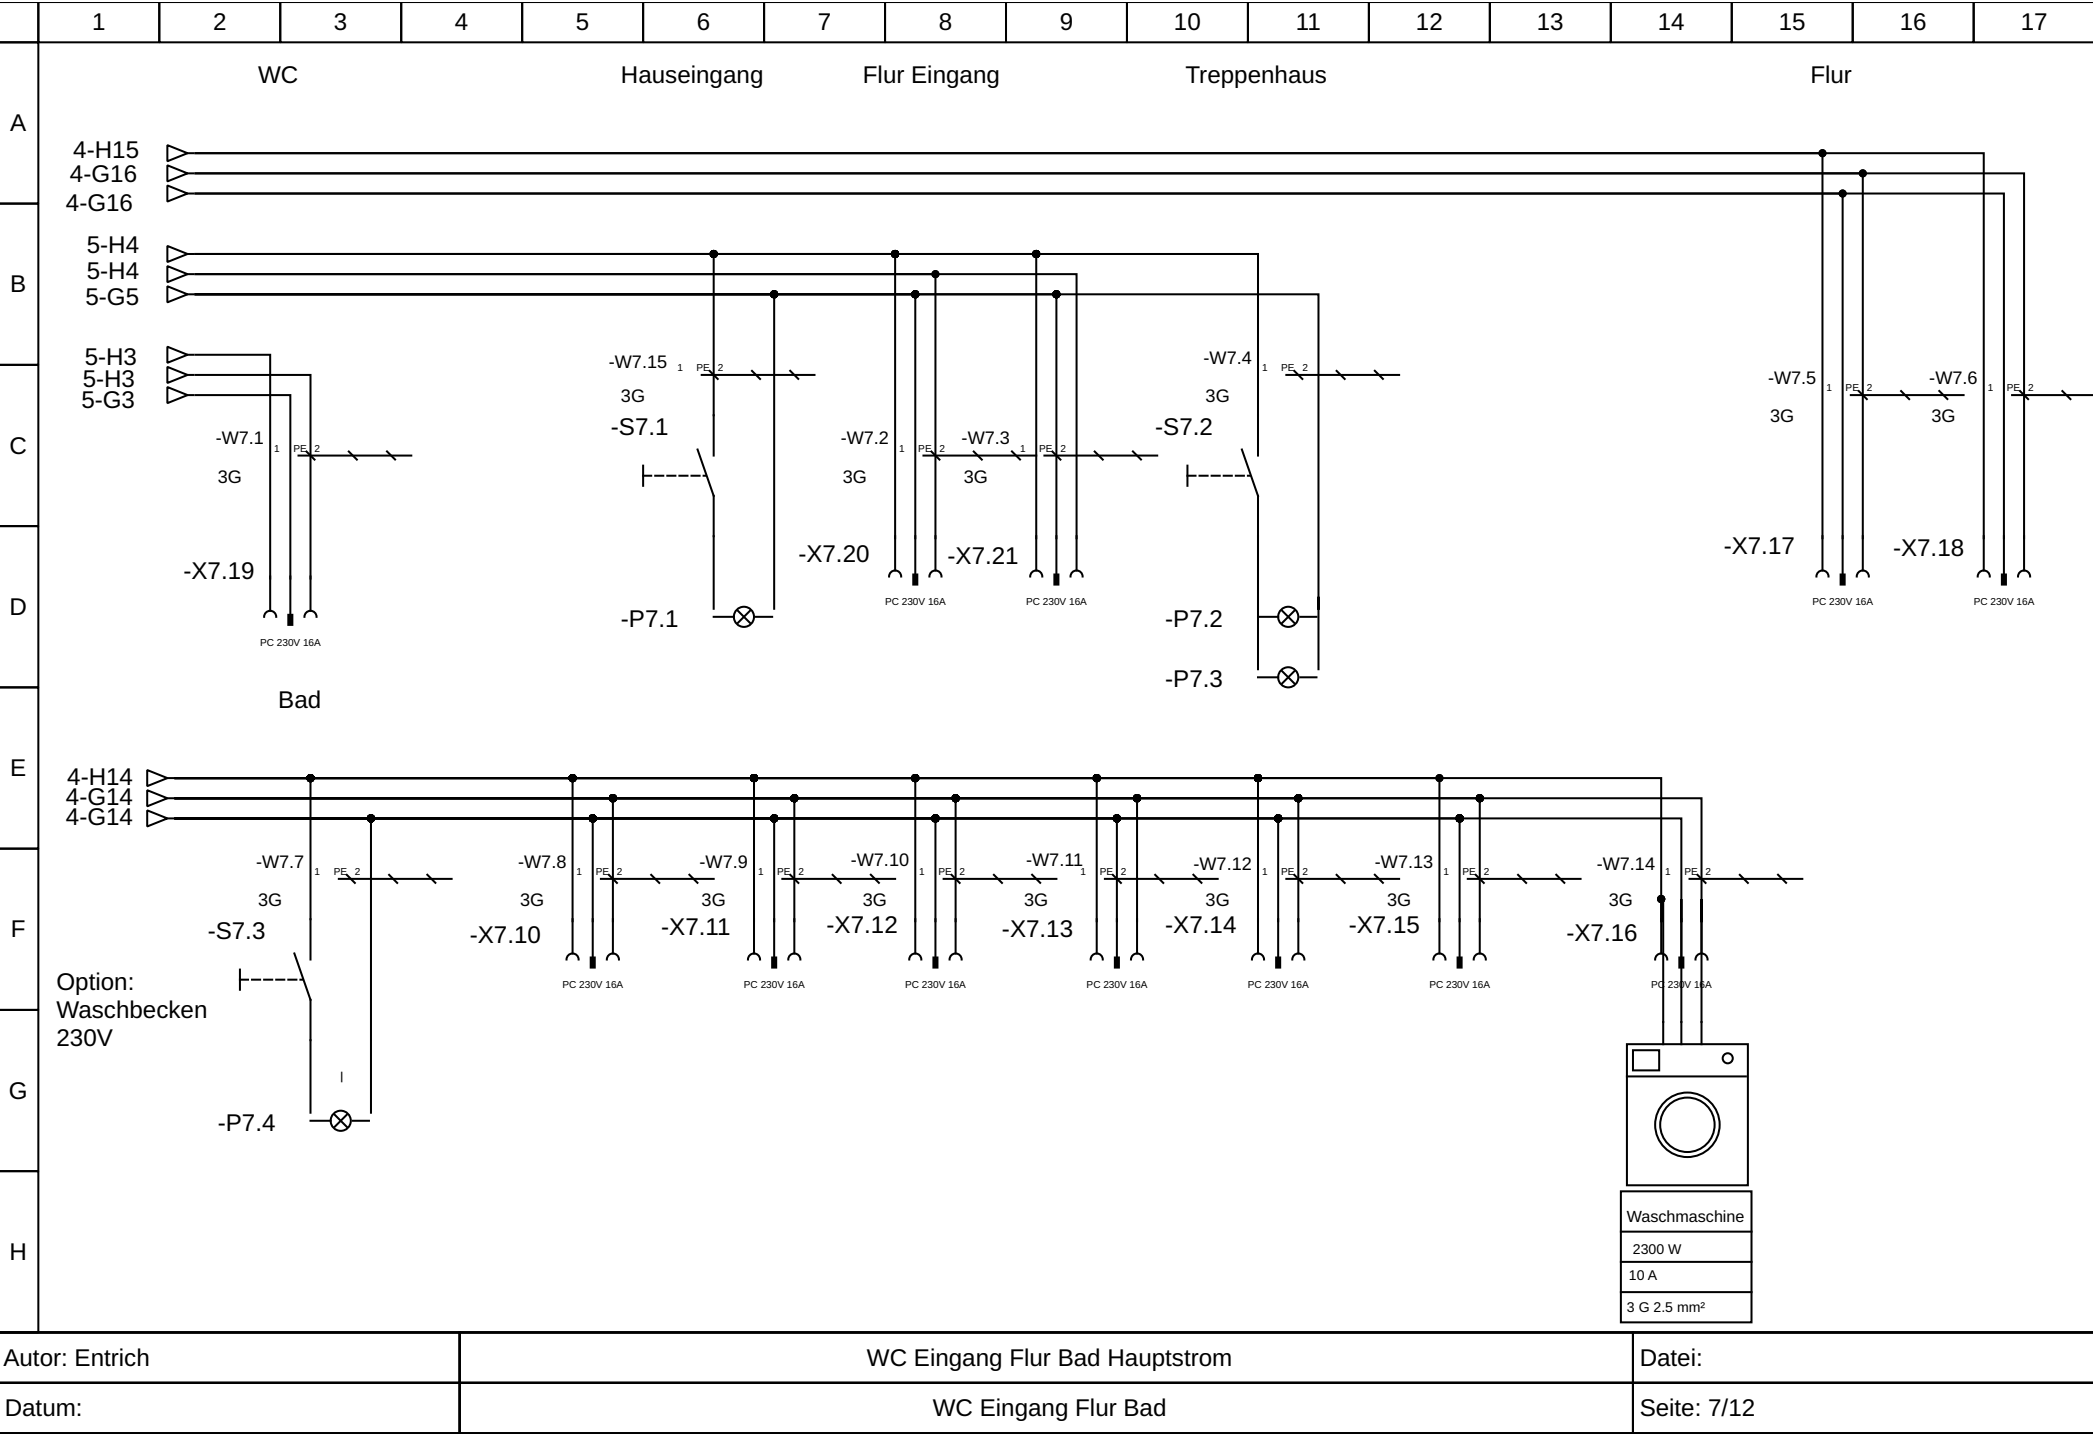

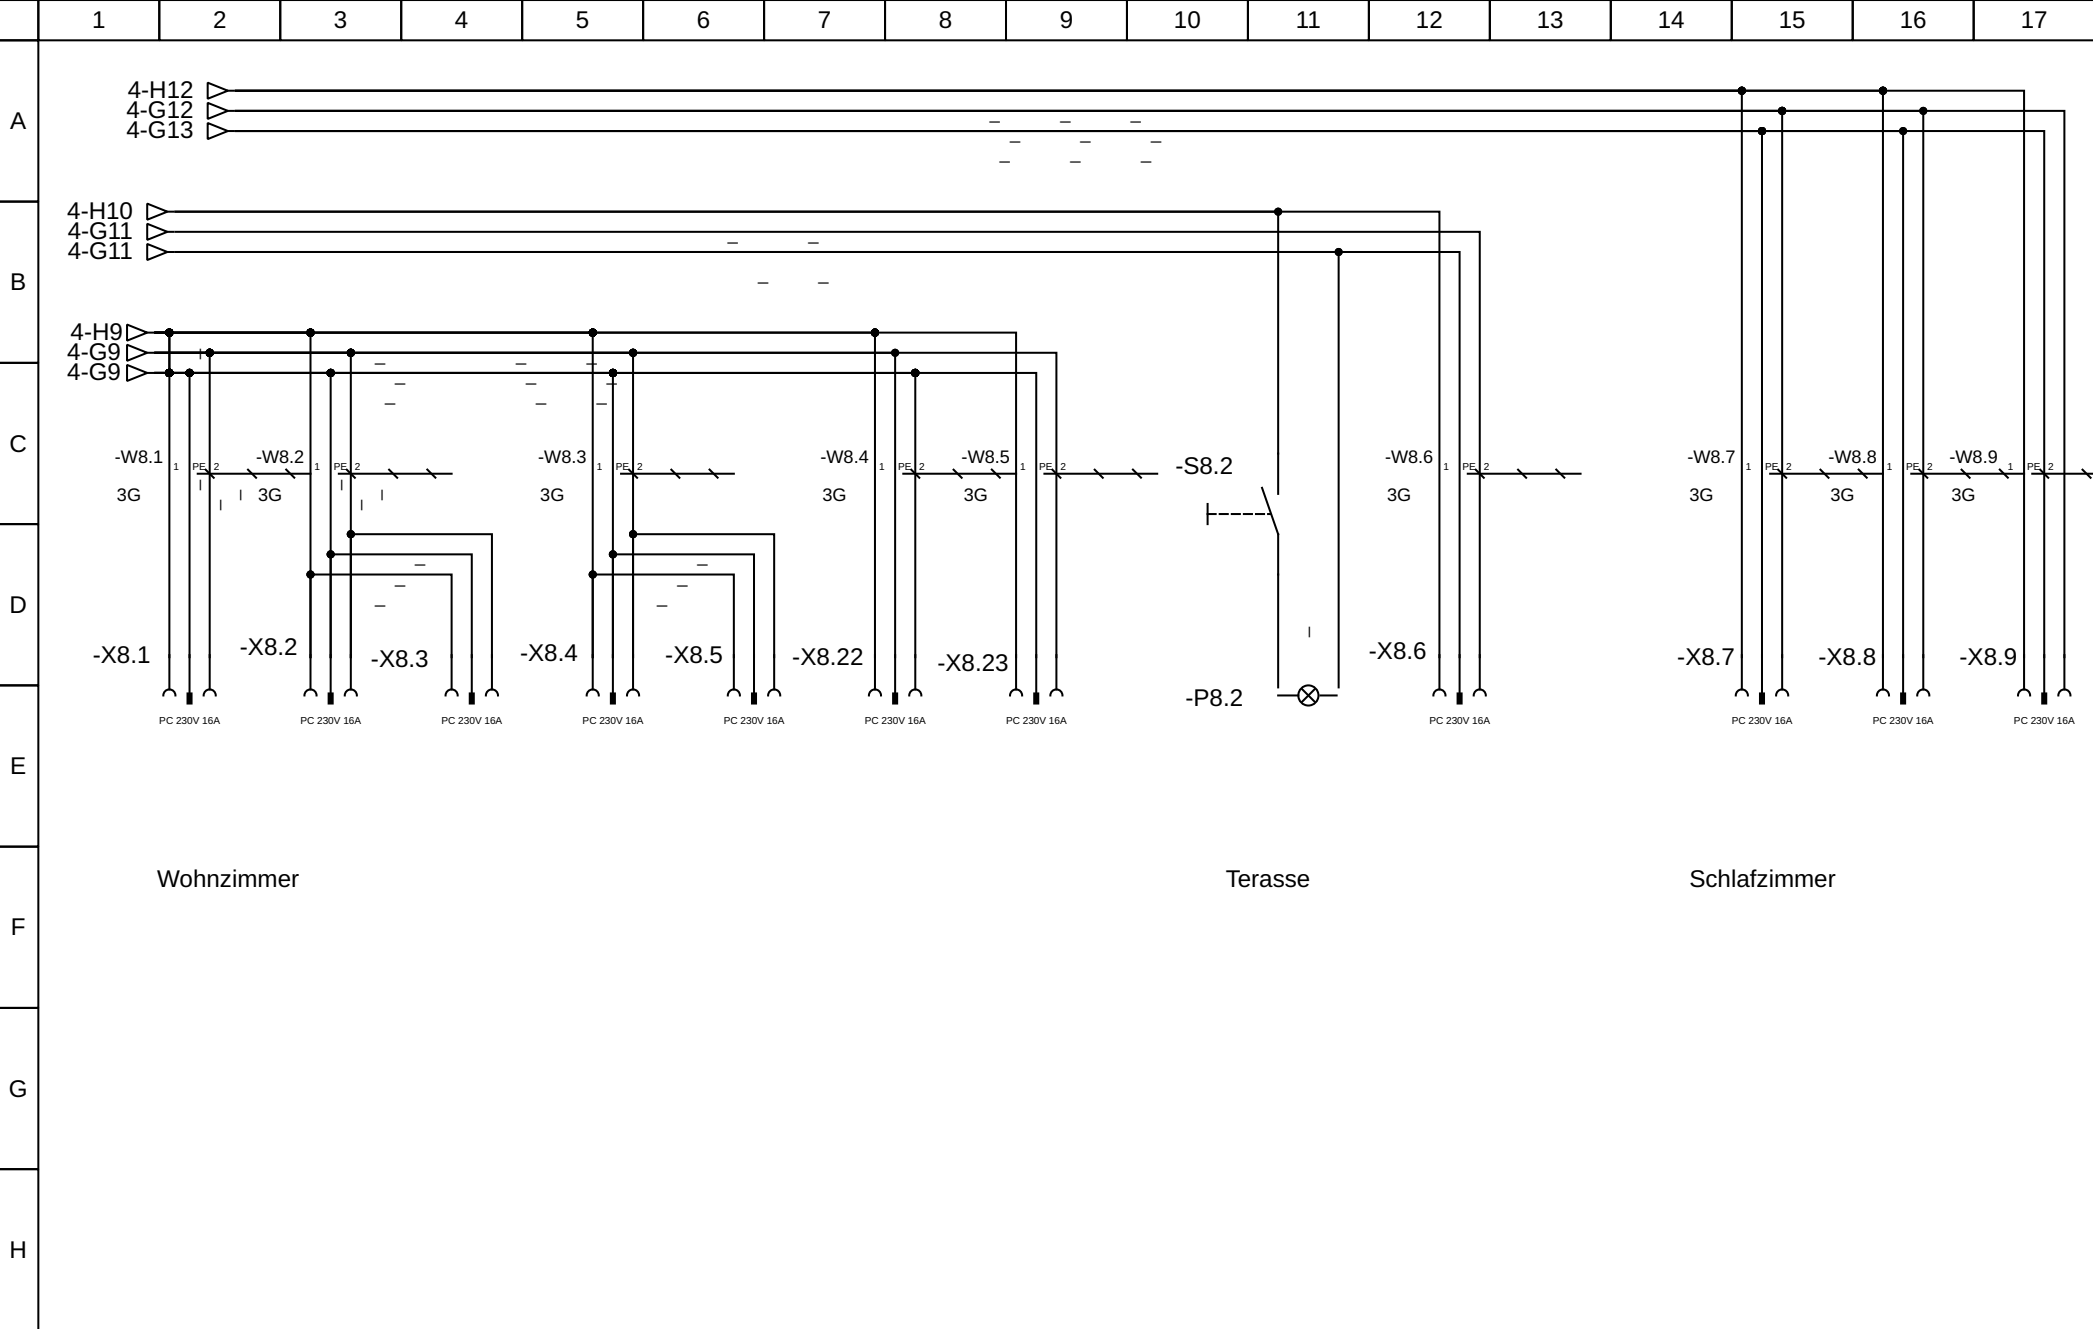

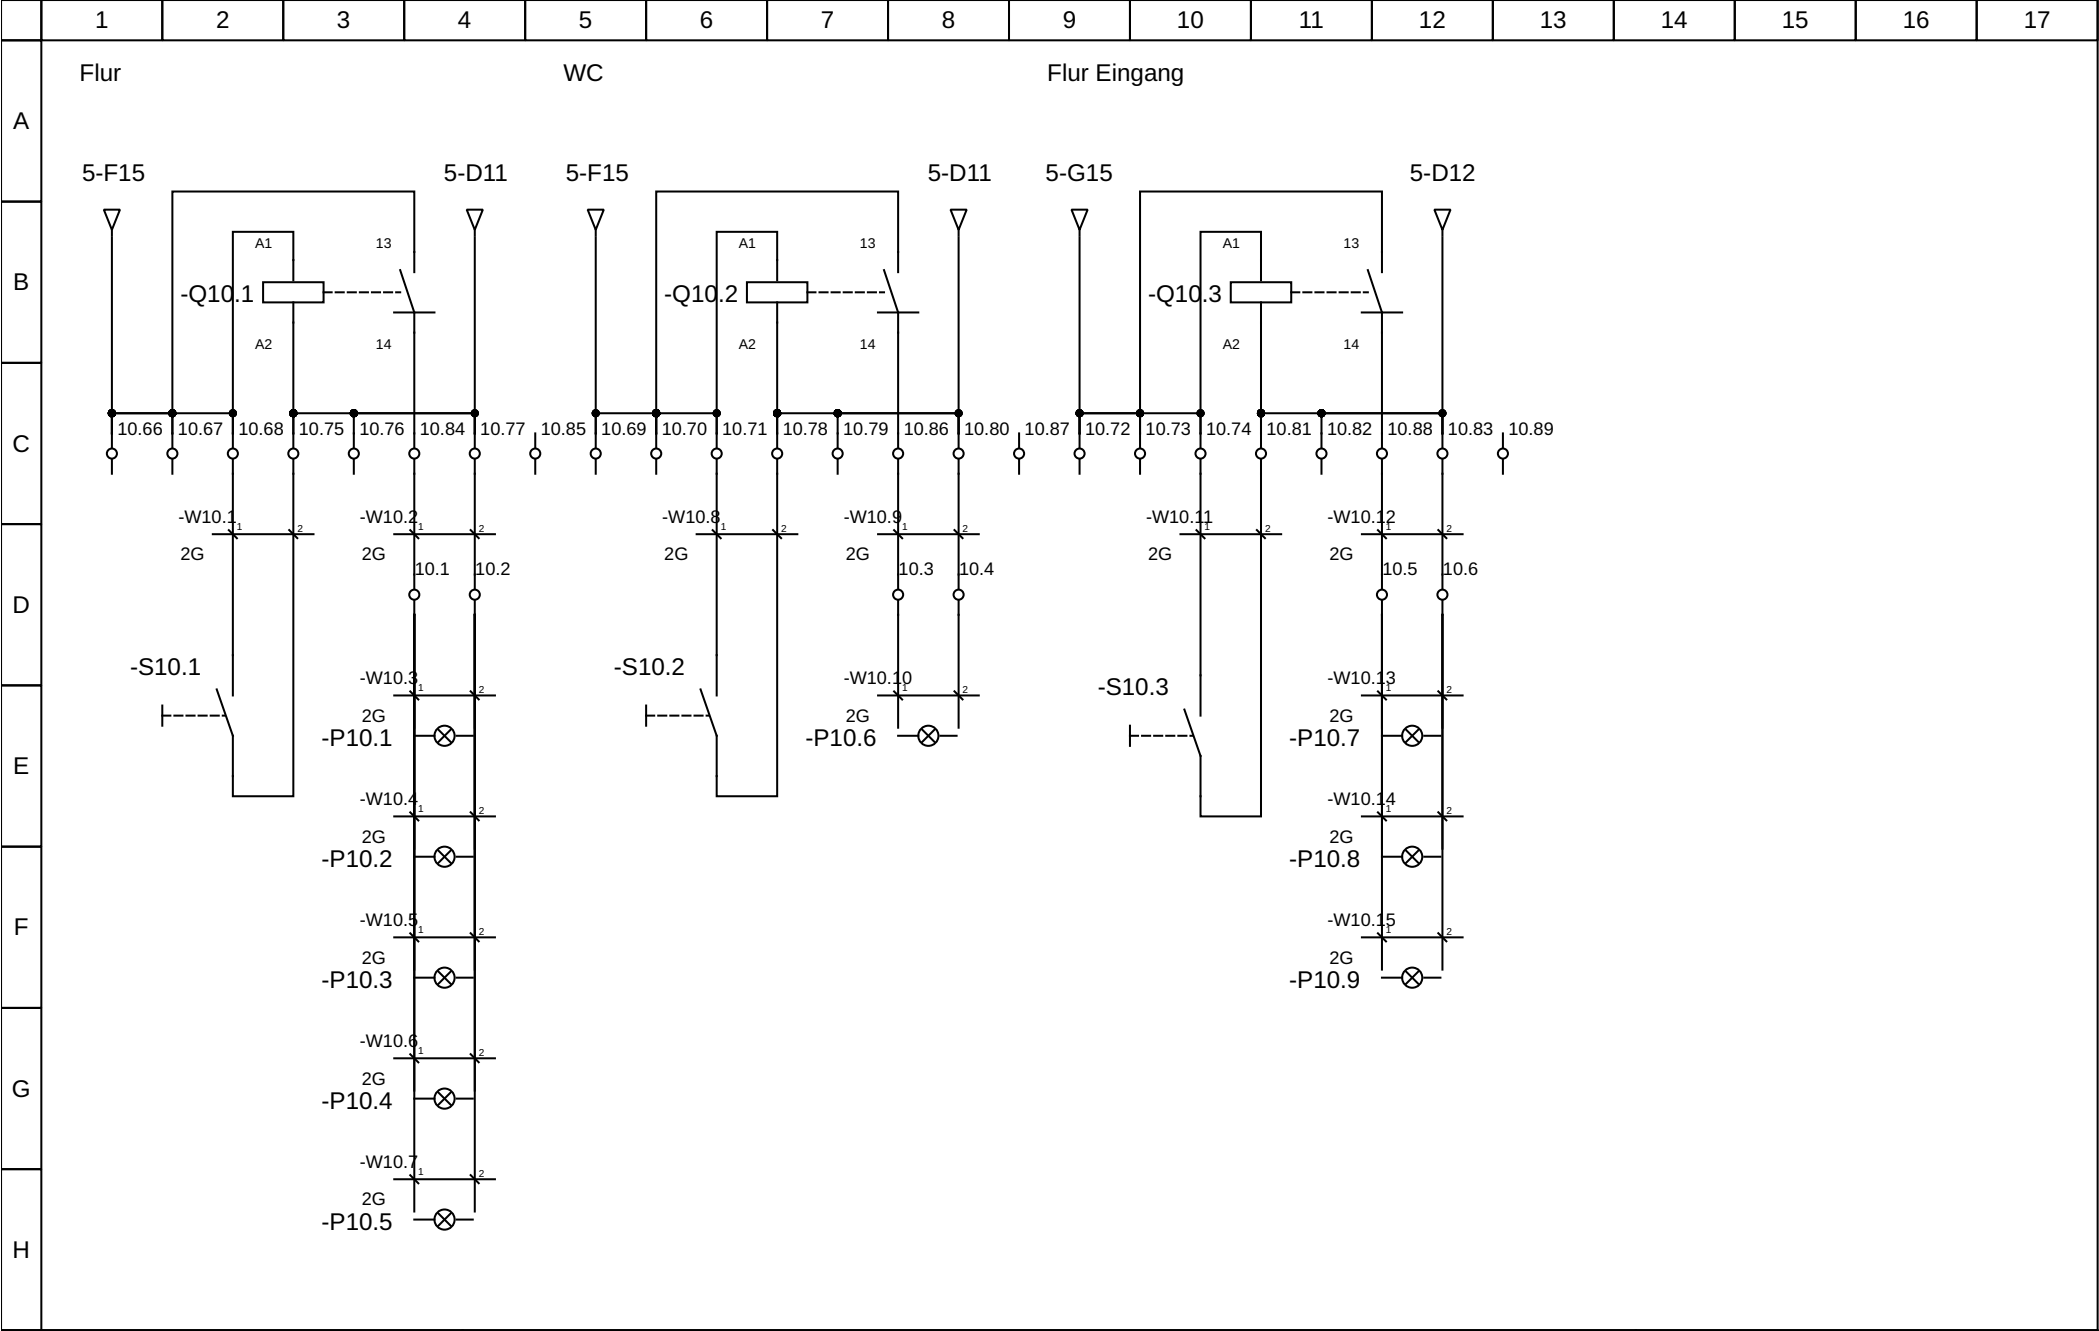

	1	2	3	4	5	6	7	8	9	10	11	12	13	14	15	16	17
A	Wohnzimmer																
B	2-D16 -X11.1																
C																	
D																	
E																	
F	-X11.2																
G																	
H																	
Autor: Entrich				Daten										Datei:			
Datum:														Seite: 11/12			

