

	1	2	3	4	5	6	7	8	9	10	11	12	13	14	15	16	17	18
A																		
	Seite	Titel				Anlage (=)		Ort (+)					Foliennummer		Revisionsindex			
B	1	Inhaltsverzeichnis				EG							1/38					
	4	Hauptversorgung				EG		Technikraum					4/38		01			
	5	Daten				EG		Technikraum					5/38		01			
	6	Heizung				EG		Wärmepump					6/38		01			
C	7	Sicherung				EG		Verteiler					7/38		01			
	8	Sicherung				EG		Verteiler					8/38		01			
	9	Kleinspannungversorgung				EG		Verteiler					9/38		01			
	10	Hauptstrom Küche				EG		Küche					10/38		01			
D	11	Hauptstrom Bad				EG		Bad					11/38		01			
	12	Hauptstrom				EG		Wohnzimmer Schlafzimmer Terasse					12/38		01			
	13	Hauptstrom				EG		WC Eingang Flur Bad					13/38		01			
	14	Kleinspannung				EG		Küche Wohnzimmer Schlafzimmer Bad					14/38		01			
E	15	Kleinspannung				EG		Flur WC Eingang					15/38		01			
	16	Thermostate				EG		Küche Wohnzimmer Bad Schlafzimmer Flur					16/38		01			
	17	Daten				EG		Verteiler Wohnzimmer					17/38		01			
	18	Klemmenplan				EG		Verteiler					18/38		01			
F																		
G																		
H																		
Autor: Entrich					Inhaltsverzeichnis										Datei:			
Datum:															Seite: 1/38			



	1	2	3	4	5	6	7	8	9	10	11	12	13	14	15	16	17	
A	<table><tr><th>Seite</th><th>Titel</th><th>Anlage (=)</th><th>Ort (+)</th><th>Foliennummer</th><th>Revisionsindex</th></tr><tr><td>2</td><td>Inhaltsverzeichnis</td><td>OG</td><td></td><td>2/38</td><td>01</td></tr><tr><td>19</td><td>Sicherung</td><td>OG</td><td>Verteiler</td><td>19/38</td><td>01</td></tr><tr><td>20</td><td>Sicherung</td><td>OG</td><td>Verteiler</td><td>20/38</td><td>01</td></tr><tr><td>21</td><td>Sicherung</td><td>OG</td><td>Küche</td><td>21/38</td><td>01</td></tr><tr><td>22</td><td>Kleinspannungsversorgung</td><td>OG</td><td>Verteiler</td><td>22/38</td><td>01</td></tr><tr><td>23</td><td>Hauptstrom Küche</td><td>OG</td><td>Küche</td><td>23/38</td><td>01</td></tr><tr><td>24</td><td>Hauptstrom Küche Esstisch</td><td>OG</td><td>Küche Esstisch Balkon</td><td>24/38</td><td>01</td></tr><tr><td>25</td><td>Hauptstrom</td><td>OG</td><td>Wohnzimmer Büro</td><td>25/38</td><td>01</td></tr><tr><td>26</td><td>Hauptstrom</td><td>OG</td><td>Mehrzweckraum Flur WC Balkon</td><td>26/38</td><td>01</td></tr><tr><td>27</td><td>Kleinspannung</td><td>OG</td><td>Küche Wohnzimmer</td><td>27/38</td><td>01</td></tr><tr><td>28</td><td>Kleinspannung</td><td>OG</td><td>WC Flur Mehrzweckraum Büro</td><td>28/38</td><td>01</td></tr><tr><td>29</td><td>Thermostate</td><td>OG</td><td>Verteiler</td><td>29/38</td><td>01</td></tr><tr><td>30</td><td>Daten</td><td>OG</td><td>Verteiler</td><td>30/38</td><td>01</td></tr><tr><td>31</td><td>Klemmenplan</td><td>OG</td><td>Verteiler</td><td>31/38</td><td>01</td></tr></table>																	Seite	Titel	Anlage (=)	Ort (+)	Foliennummer	Revisionsindex	2	Inhaltsverzeichnis	OG		2/38	01	19	Sicherung	OG	Verteiler	19/38	01	20	Sicherung	OG	Verteiler	20/38	01	21	Sicherung	OG	Küche	21/38	01	22	Kleinspannungsversorgung	OG	Verteiler	22/38	01	23	Hauptstrom Küche	OG	Küche	23/38	01	24	Hauptstrom Küche Esstisch	OG	Küche Esstisch Balkon	24/38	01	25	Hauptstrom	OG	Wohnzimmer Büro	25/38	01	26	Hauptstrom	OG	Mehrzweckraum Flur WC Balkon	26/38	01	27	Kleinspannung	OG	Küche Wohnzimmer	27/38	01	28	Kleinspannung	OG	WC Flur Mehrzweckraum Büro	28/38	01	29	Thermostate	OG	Verteiler	29/38	01	30	Daten	OG	Verteiler	30/38	01	31	Klemmenplan	OG	Verteiler	31/38	01
Seite																		Titel	Anlage (=)	Ort (+)	Foliennummer	Revisionsindex	
2																		Inhaltsverzeichnis	OG		2/38	01	
19																		Sicherung	OG	Verteiler	19/38	01	
20																		Sicherung	OG	Verteiler	20/38	01	
21																		Sicherung	OG	Küche	21/38	01	
22																		Kleinspannungsversorgung	OG	Verteiler	22/38	01	
23																		Hauptstrom Küche	OG	Küche	23/38	01	
24																		Hauptstrom Küche Esstisch	OG	Küche Esstisch Balkon	24/38	01	
25																		Hauptstrom	OG	Wohnzimmer Büro	25/38	01	
26																		Hauptstrom	OG	Mehrzweckraum Flur WC Balkon	26/38	01	
27																		Kleinspannung	OG	Küche Wohnzimmer	27/38	01	
28																		Kleinspannung	OG	WC Flur Mehrzweckraum Büro	28/38	01	
29																		Thermostate	OG	Verteiler	29/38	01	
30																		Daten	OG	Verteiler	30/38	01	
31																		Klemmenplan	OG	Verteiler	31/38	01	
B	
B	
B	
B	
B	
C	
C	
C	
C	
D	
D	
D	
D	
E	
E	
F	
G	
H	


Autor: Entrich				Inhaltsverzeichnis								Datei:				
Datum:												Seite: 2/38				


	1	2	3	4	5	6	7	8	9	10	11	12	13	14	15	16	17	
A	<table><tr><th>Seite</th><th>Titel</th><th>Anlage (=)</th><th>Ort (+)</th><th>Foliennummer</th><th>Revisionsindex</th></tr><tr><td>3</td><td>Inhaltsverzeichnis</td><td>DG</td><td></td><td>3/38</td><td>01</td></tr><tr><td>32</td><td>Sicherung</td><td>DG</td><td>Verteiler</td><td>32/38</td><td>01</td></tr><tr><td>33</td><td>Kleinspannungsversorgung</td><td>DG</td><td>Verteiler</td><td>33/38</td><td>01</td></tr><tr><td>34</td><td>Hauptstrom</td><td>DG</td><td>HW Bad</td><td>34/38</td><td>01</td></tr><tr><td>35</td><td>Hauptstrom</td><td>DG</td><td>Schlafzimmer Flur Kind1 Kind2</td><td>35/38</td><td></td></tr><tr><td>36</td><td>Kleinspannung</td><td>DG</td><td>Schlafzimmer Flur Bad</td><td>36/38</td><td></td></tr><tr><td>37</td><td>Thermostate</td><td>DG</td><td>Verteiler</td><td>37/38</td><td>01</td></tr><tr><td>38</td><td>Klemmenplan</td><td>DG</td><td>Verteiler</td><td>38/38</td><td>01</td></tr></table>																	Seite	Titel	Anlage (=)	Ort (+)	Foliennummer	Revisionsindex	3	Inhaltsverzeichnis	DG		3/38	01	32	Sicherung	DG	Verteiler	32/38	01	33	Kleinspannungsversorgung	DG	Verteiler	33/38	01	34	Hauptstrom	DG	HW Bad	34/38	01	35	Hauptstrom	DG	Schlafzimmer Flur Kind1 Kind2	35/38		36	Kleinspannung	DG	Schlafzimmer Flur Bad	36/38		37	Thermostate	DG	Verteiler	37/38	01	38	Klemmenplan	DG	Verteiler	38/38	01
Seite																		Titel	Anlage (=)	Ort (+)	Foliennummer	Revisionsindex	
3																		Inhaltsverzeichnis	DG		3/38	01	
32																		Sicherung	DG	Verteiler	32/38	01	
33																		Kleinspannungsversorgung	DG	Verteiler	33/38	01	
34																		Hauptstrom	DG	HW Bad	34/38	01	
35																		Hauptstrom	DG	Schlafzimmer Flur Kind1 Kind2	35/38	
36																		Kleinspannung	DG	Schlafzimmer Flur Bad	36/38	
37																		Thermostate	DG	Verteiler	37/38	01	
38	Klemmenplan	DG	Verteiler	38/38	01	
B	
C	
D	
E	
F	
G	
H	
Autor: Entrich				Inhaltsverzeichnis										Datei:	
Datum:														Seite: 3/38	


	1	2	3	4	5	6	7	8	9	10	11	12	13	14	15	16	17
A	Bus - Heizung? Koaxialkabel Koax-Buchse/Stecker 17-B2 5.1 6-A1																
B																	
C																	
D																	
E																	
F																	
G																	
H																	
Autor: Entrich				Daten										Datei:			
Datum:														Seite: 5/38			


Bus - Heizung?

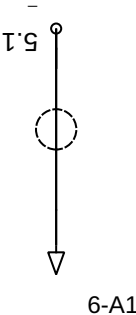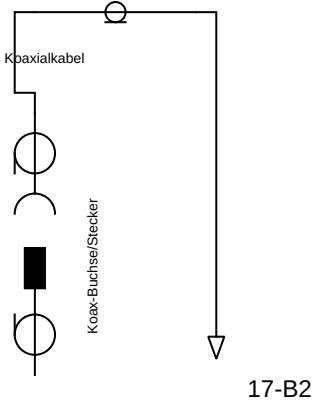


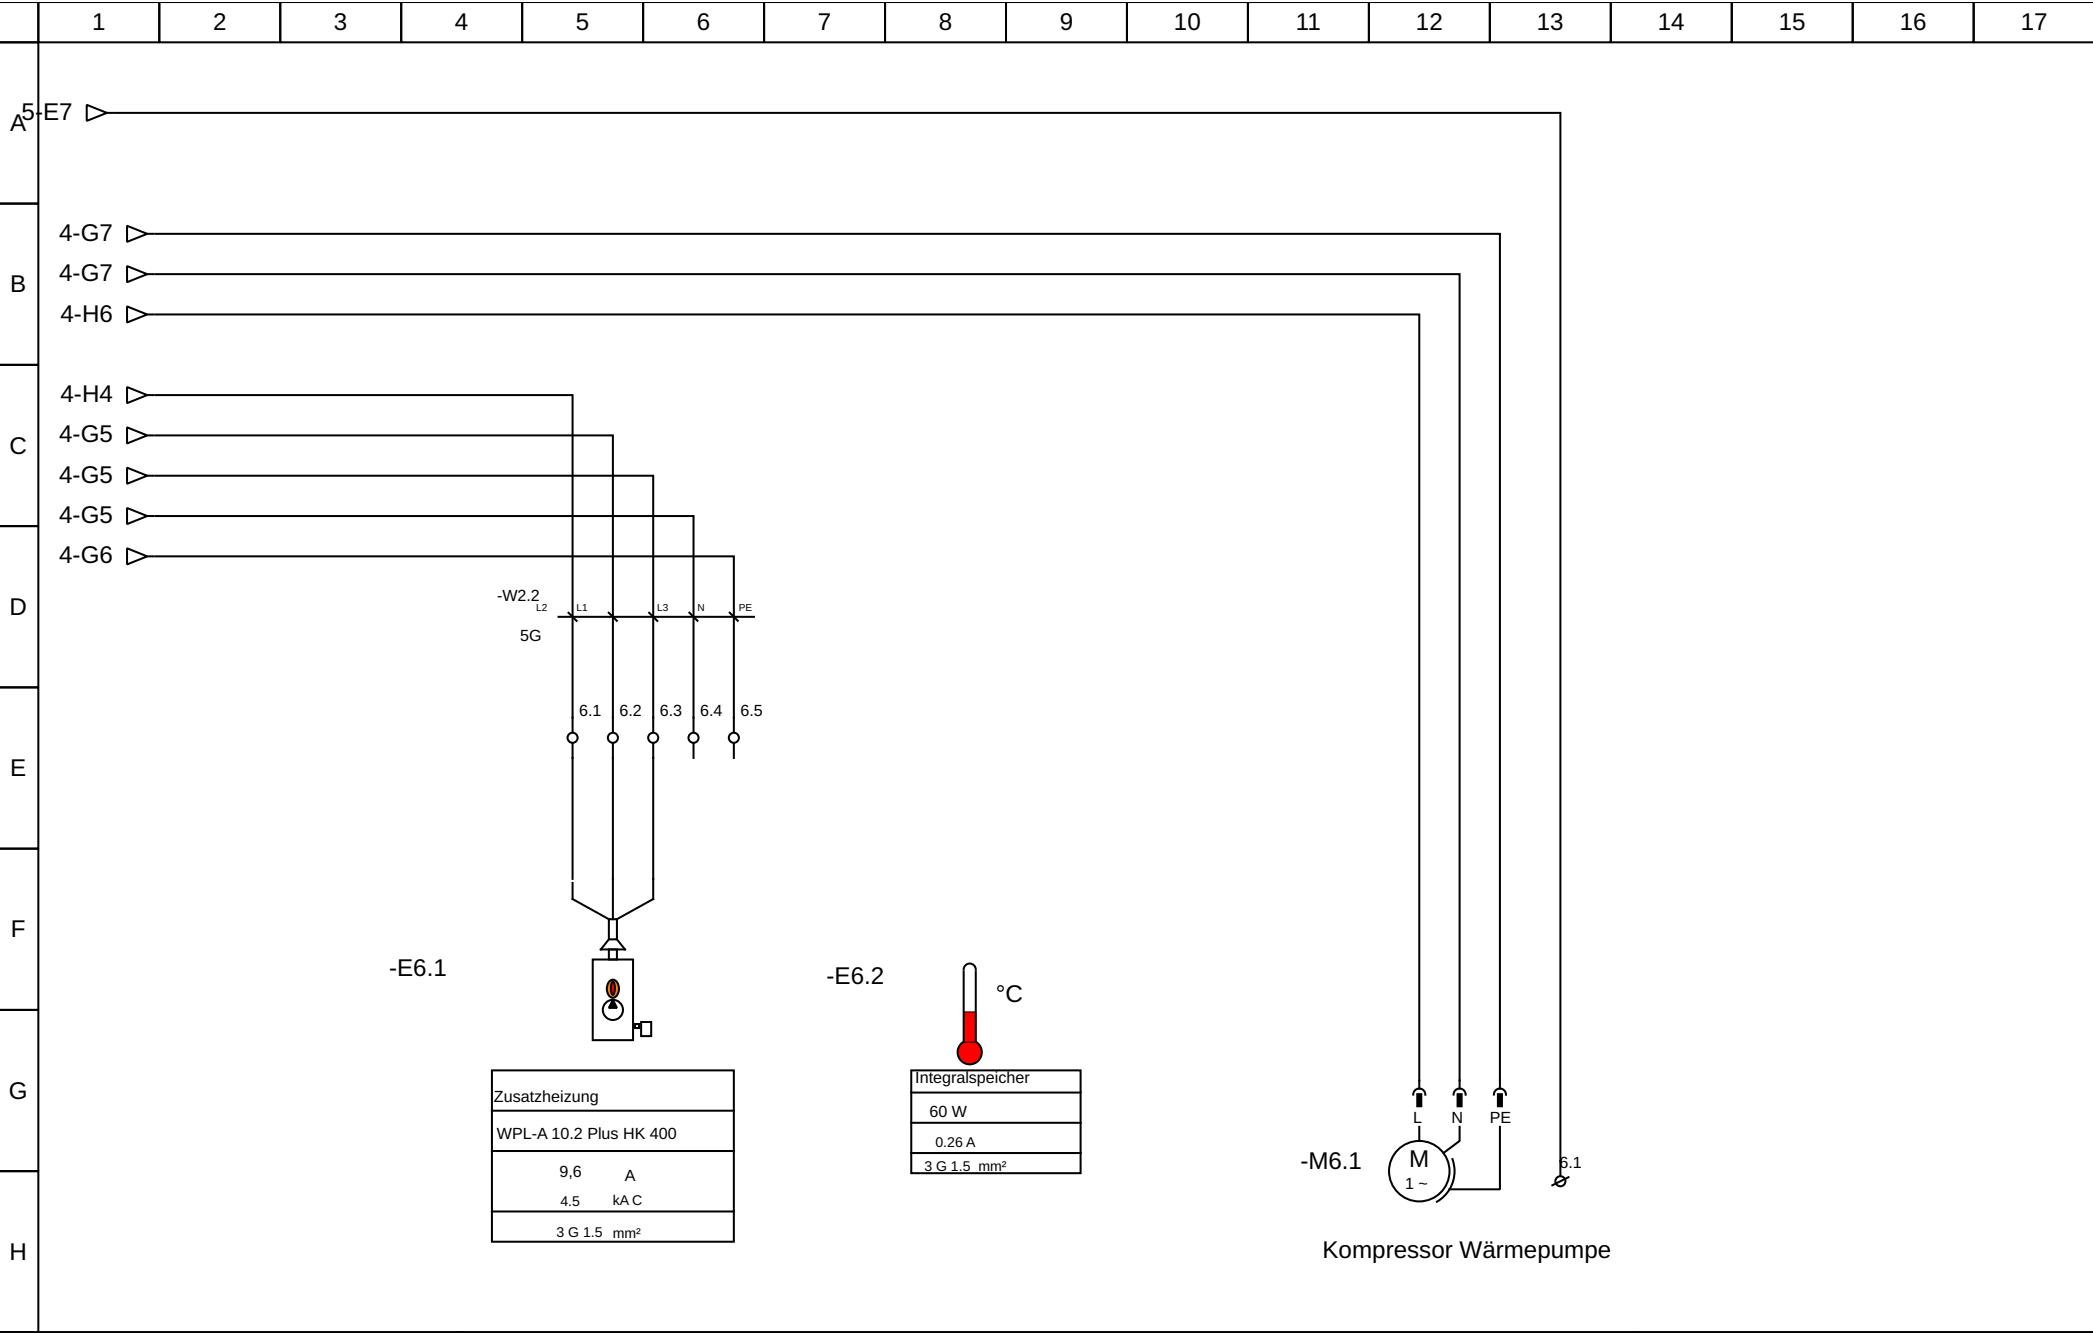


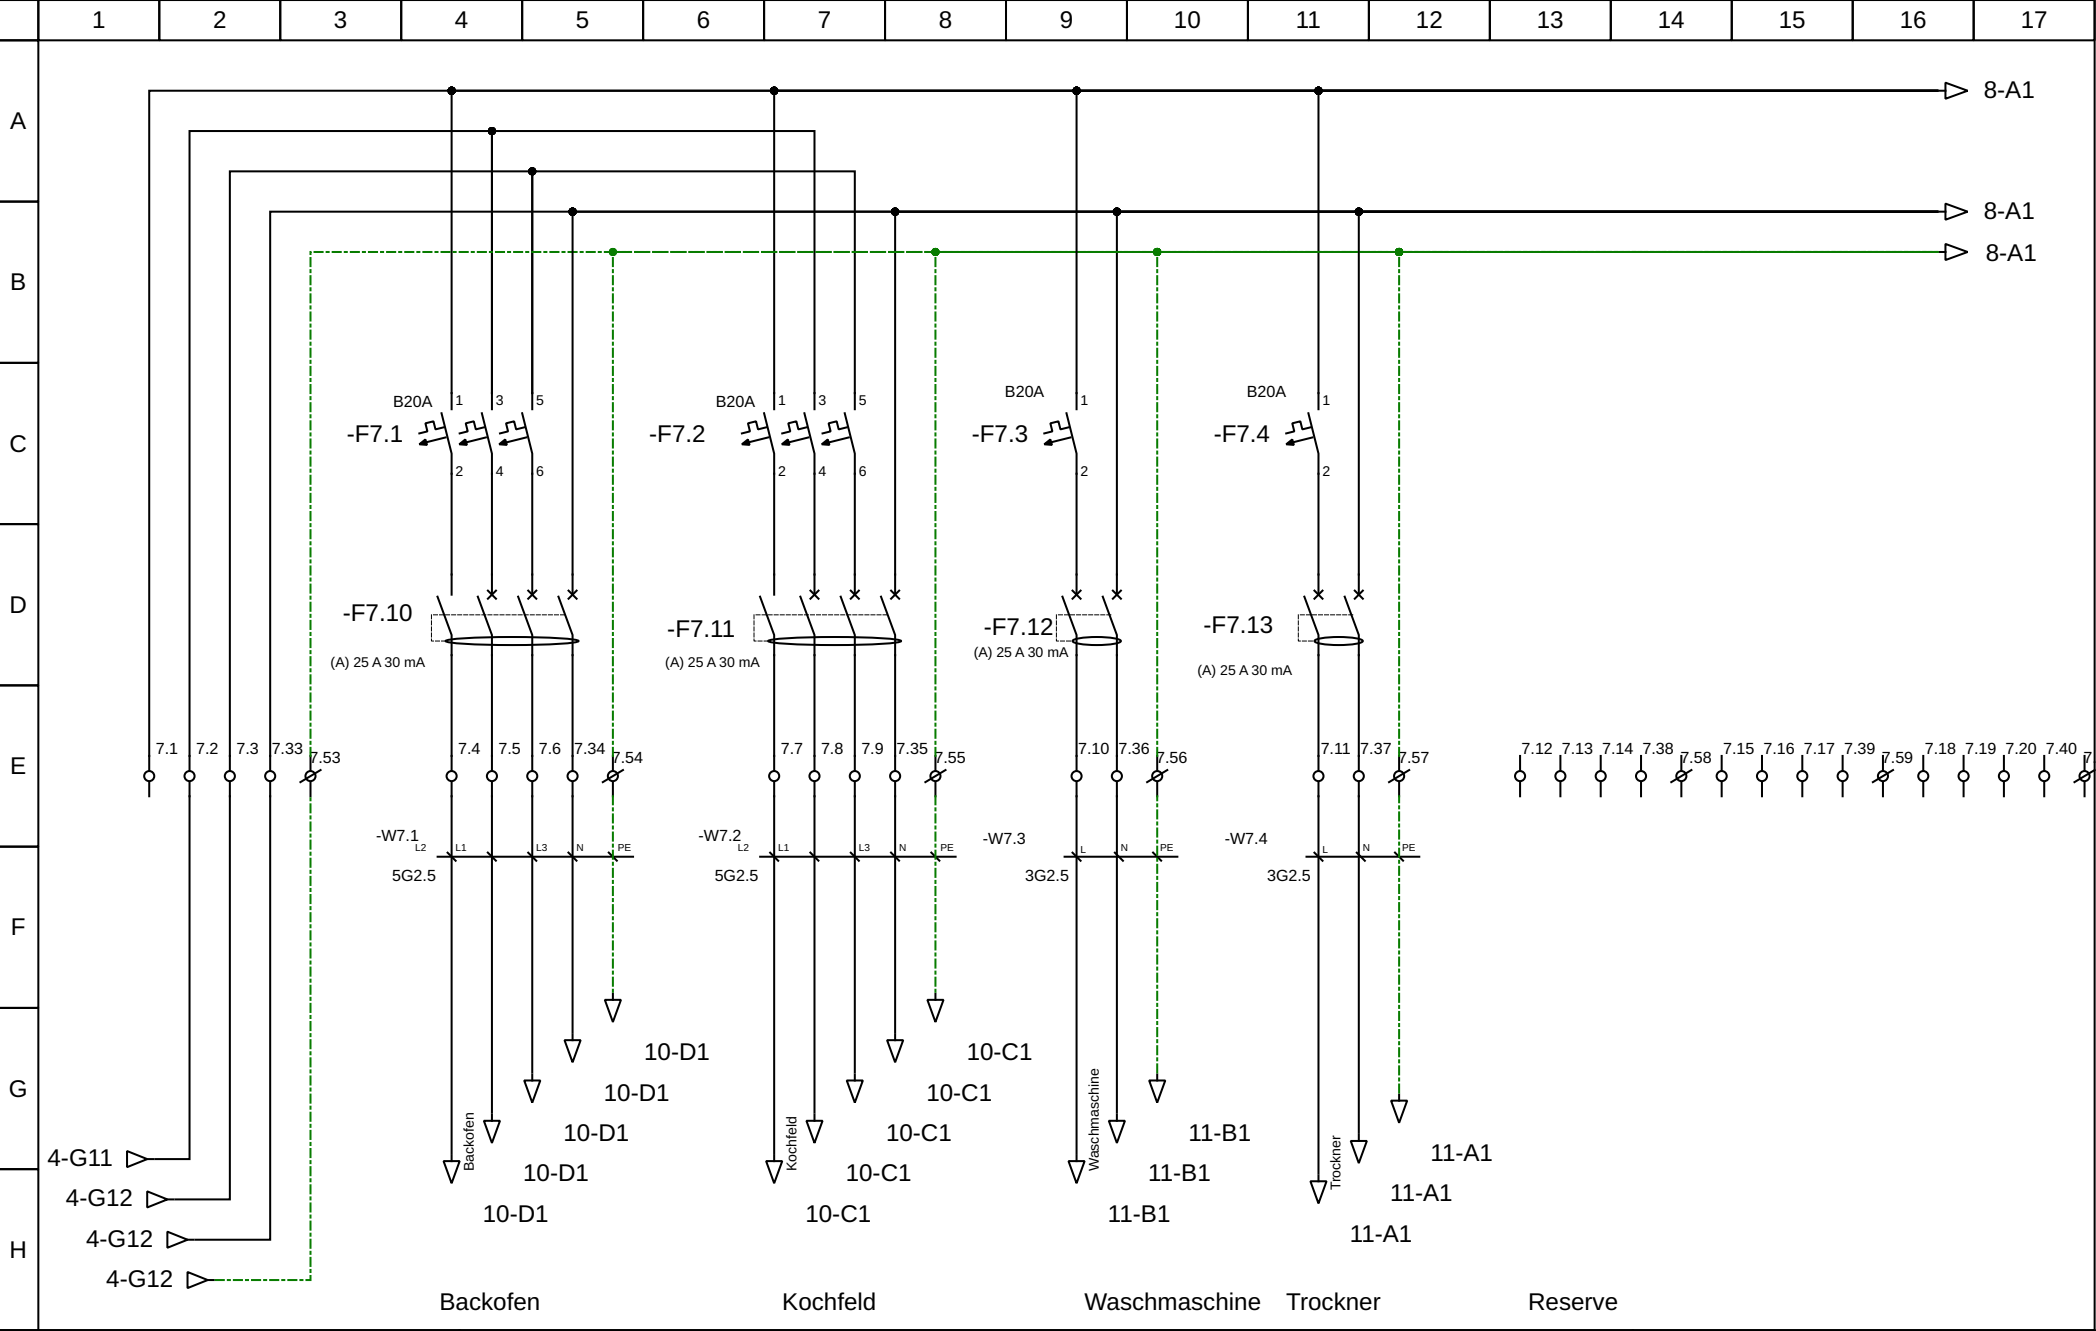


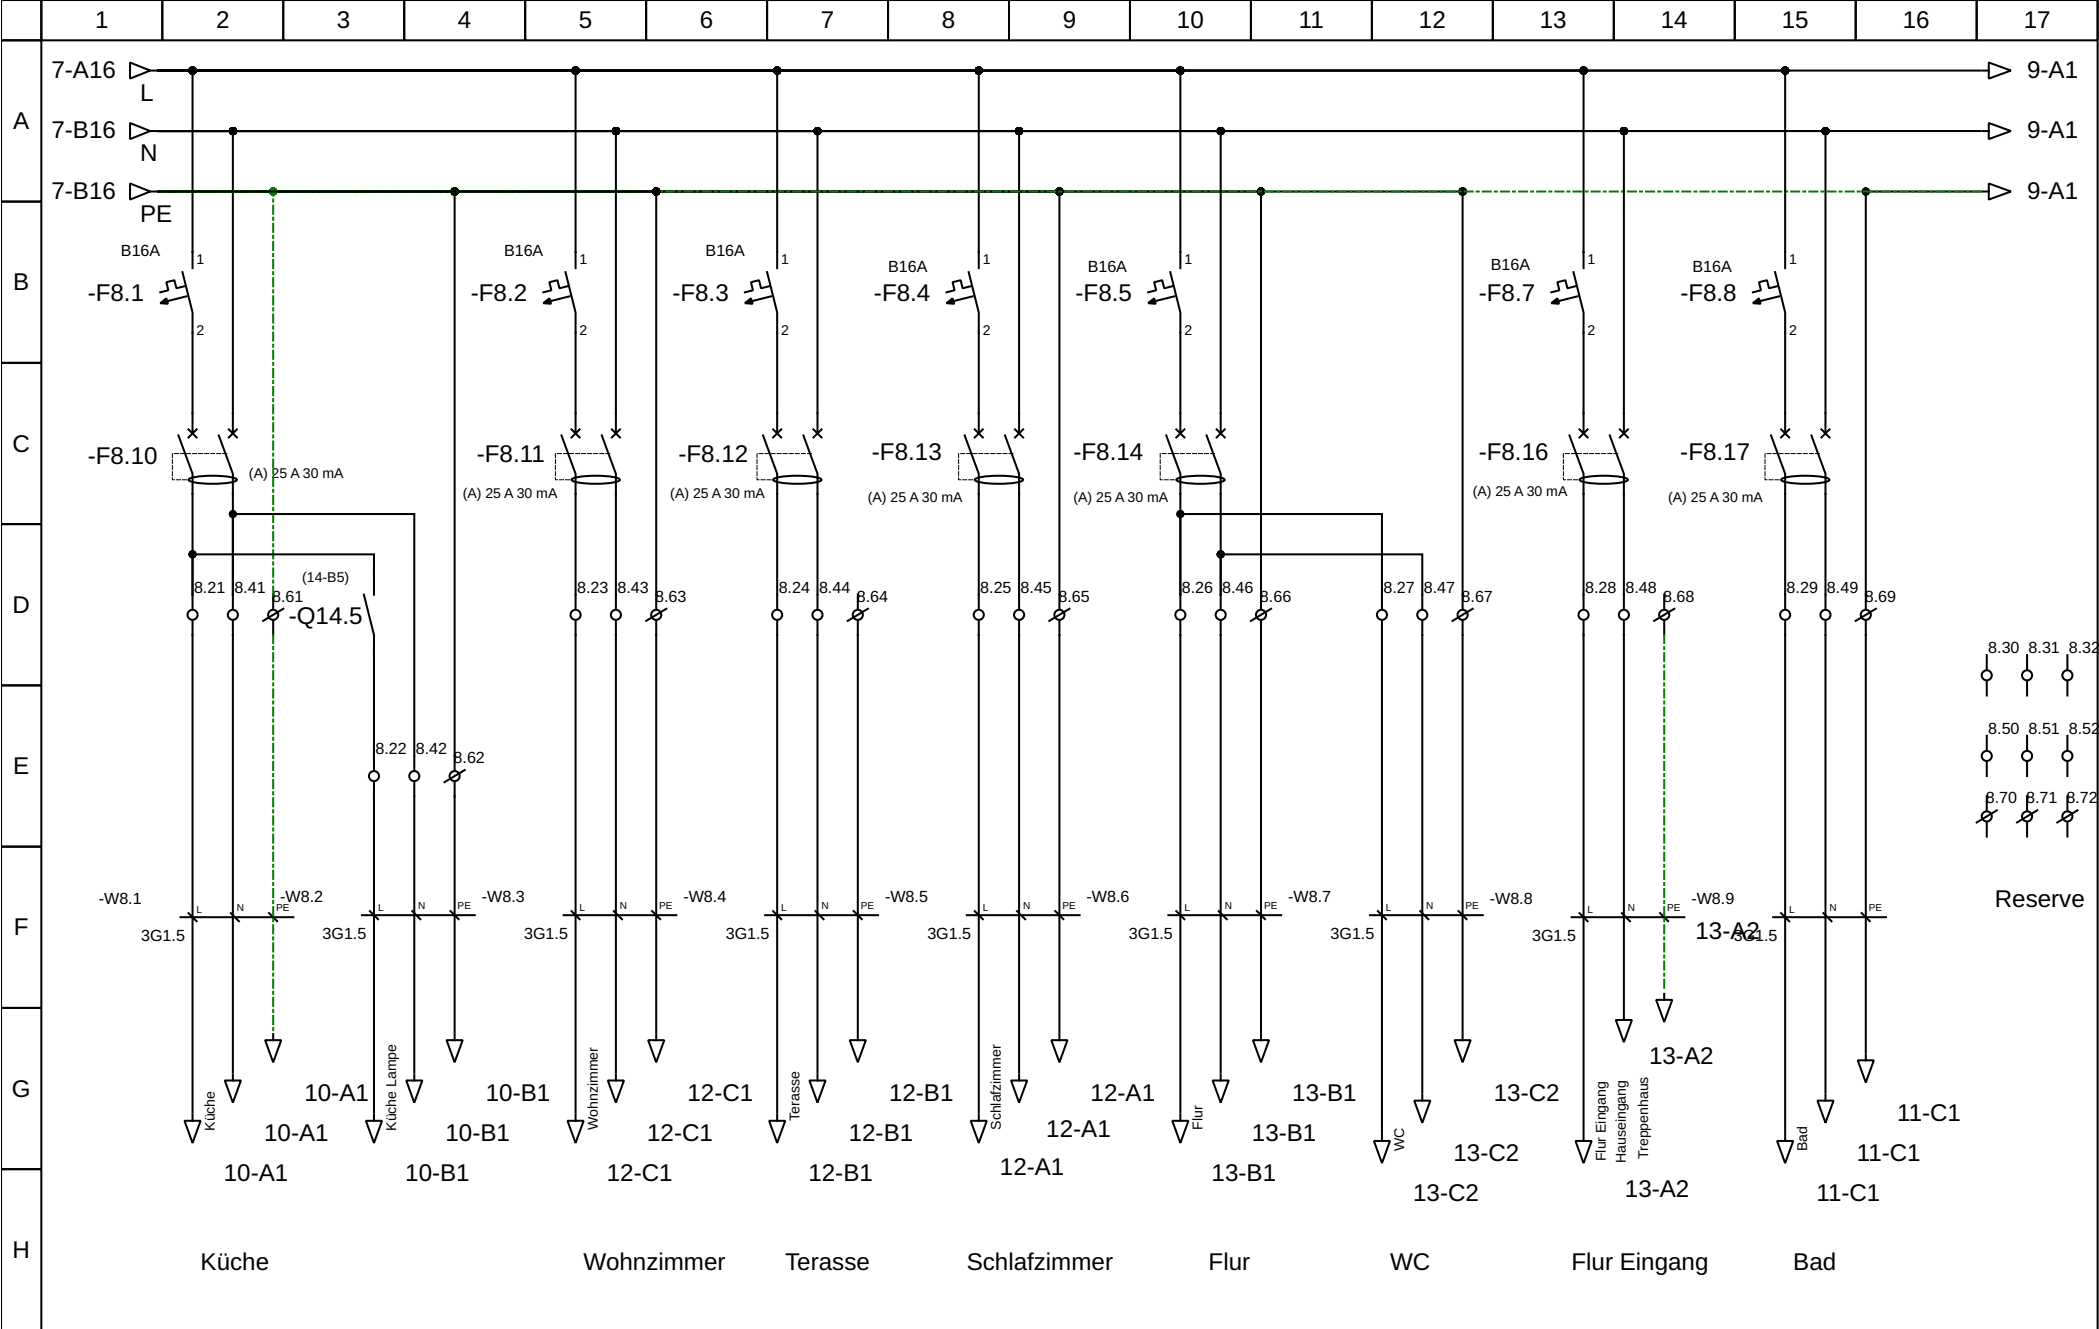


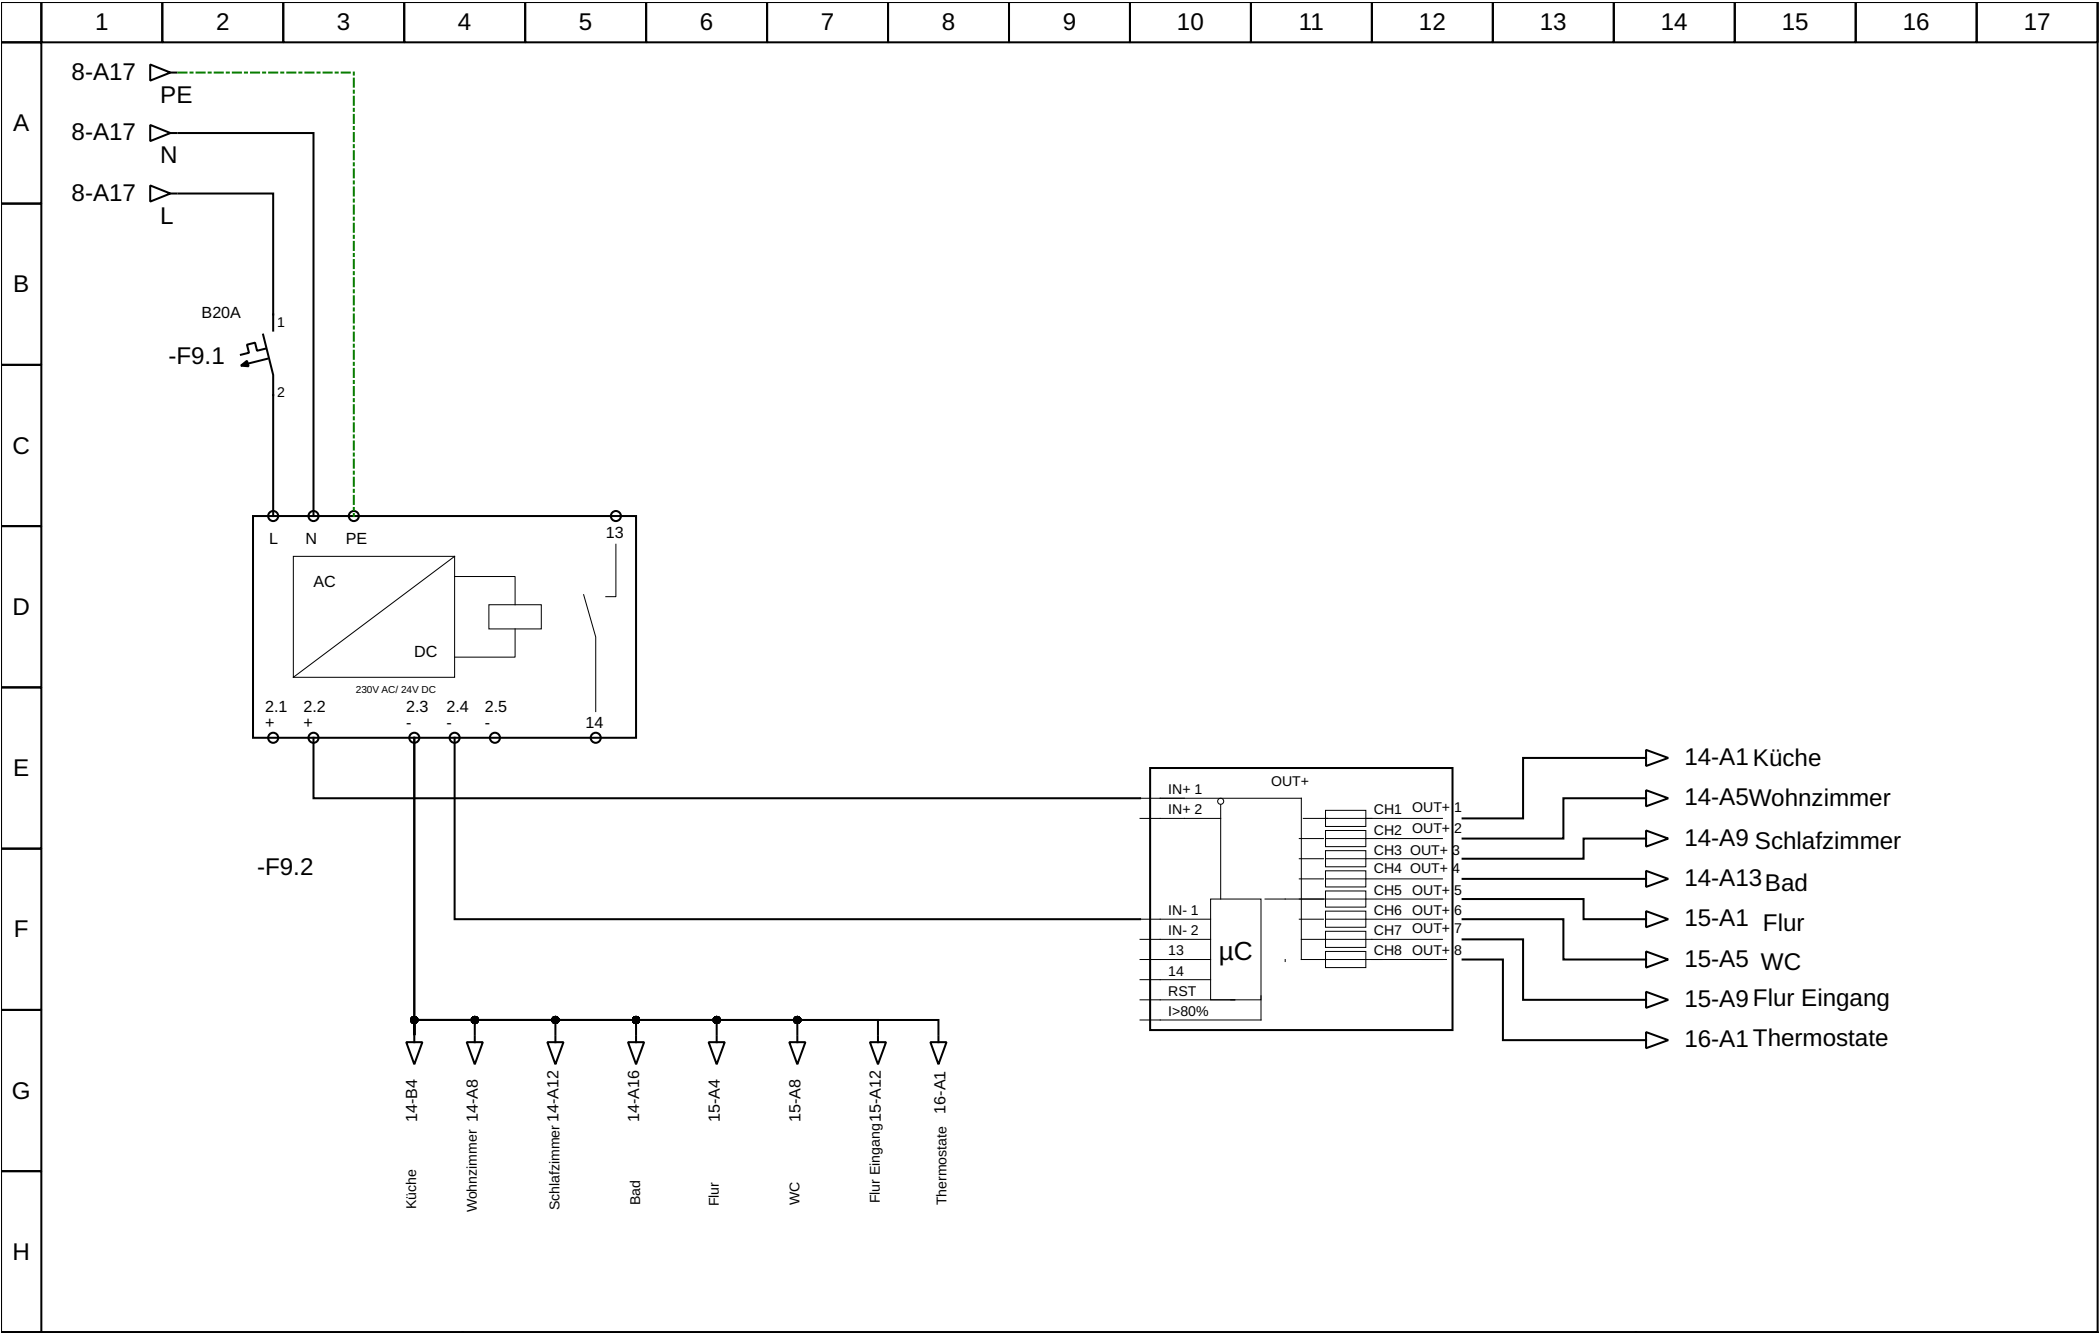


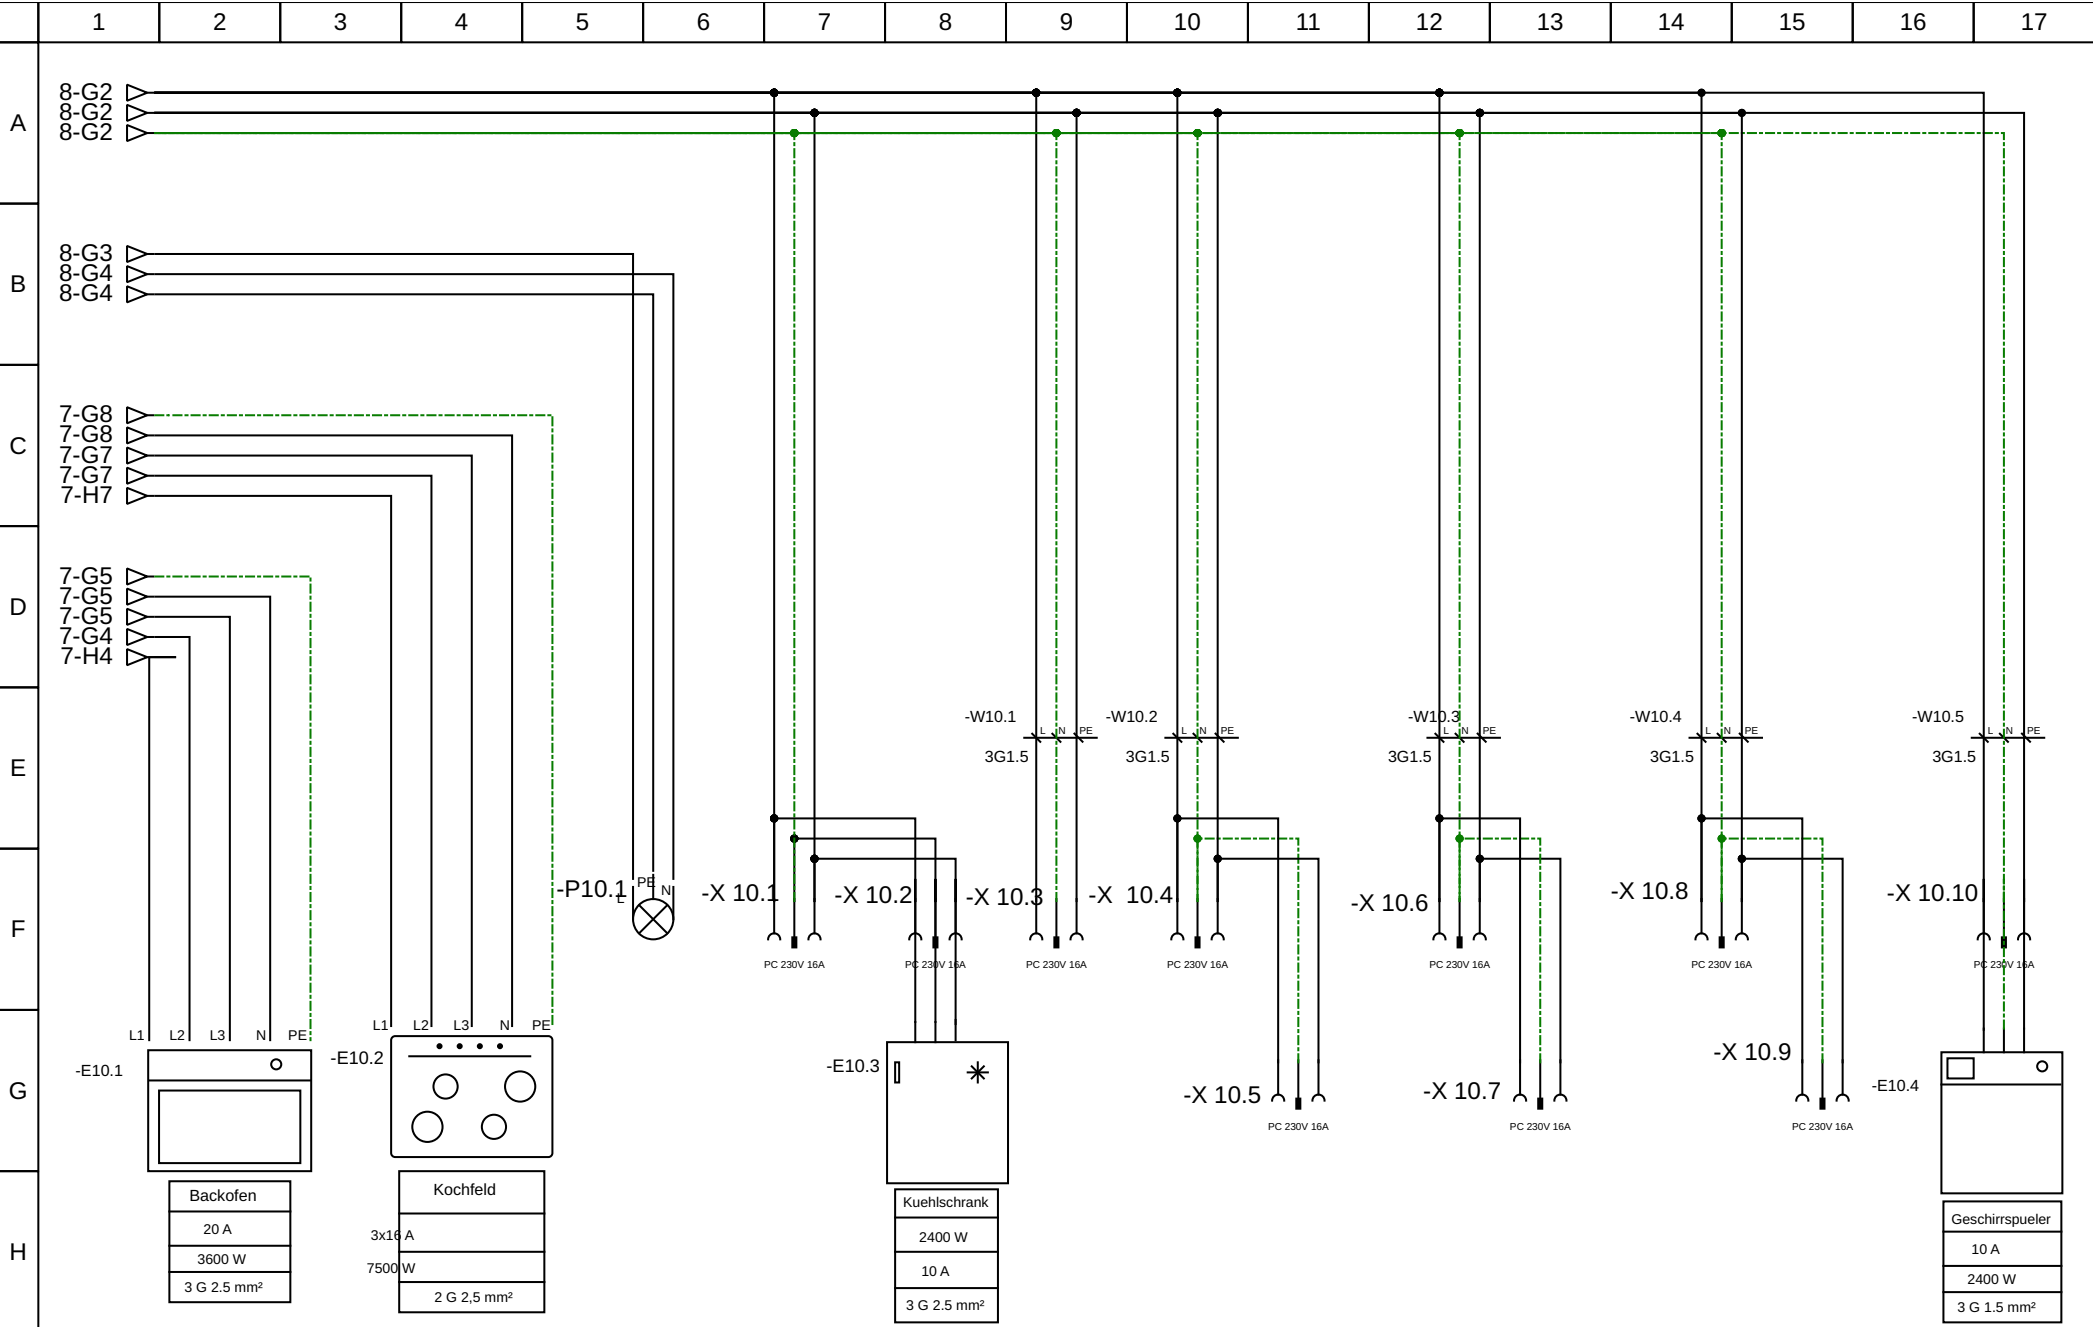


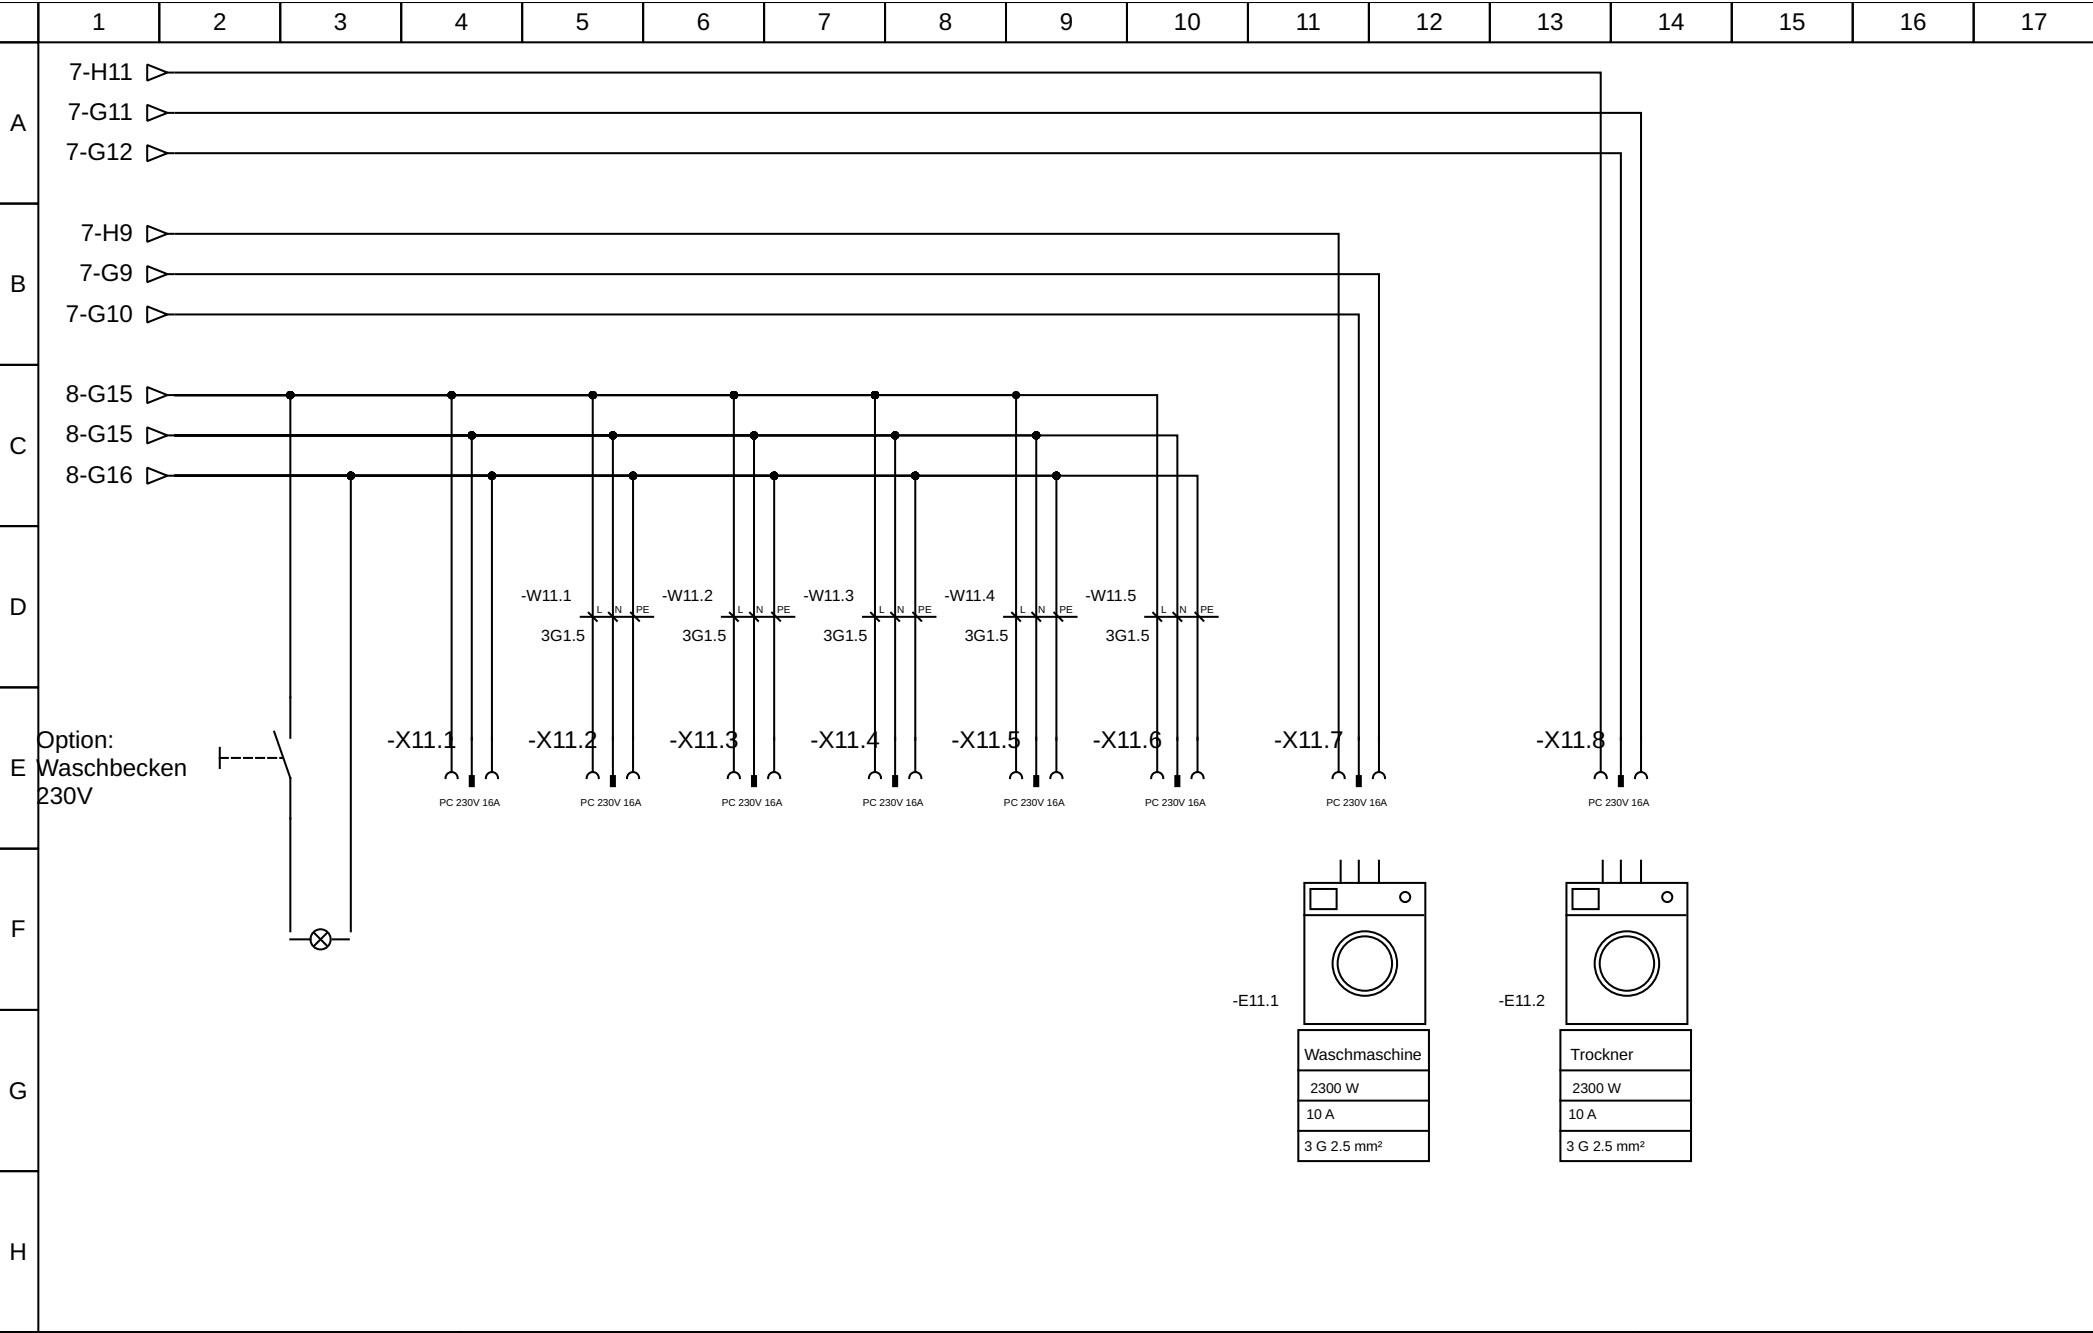


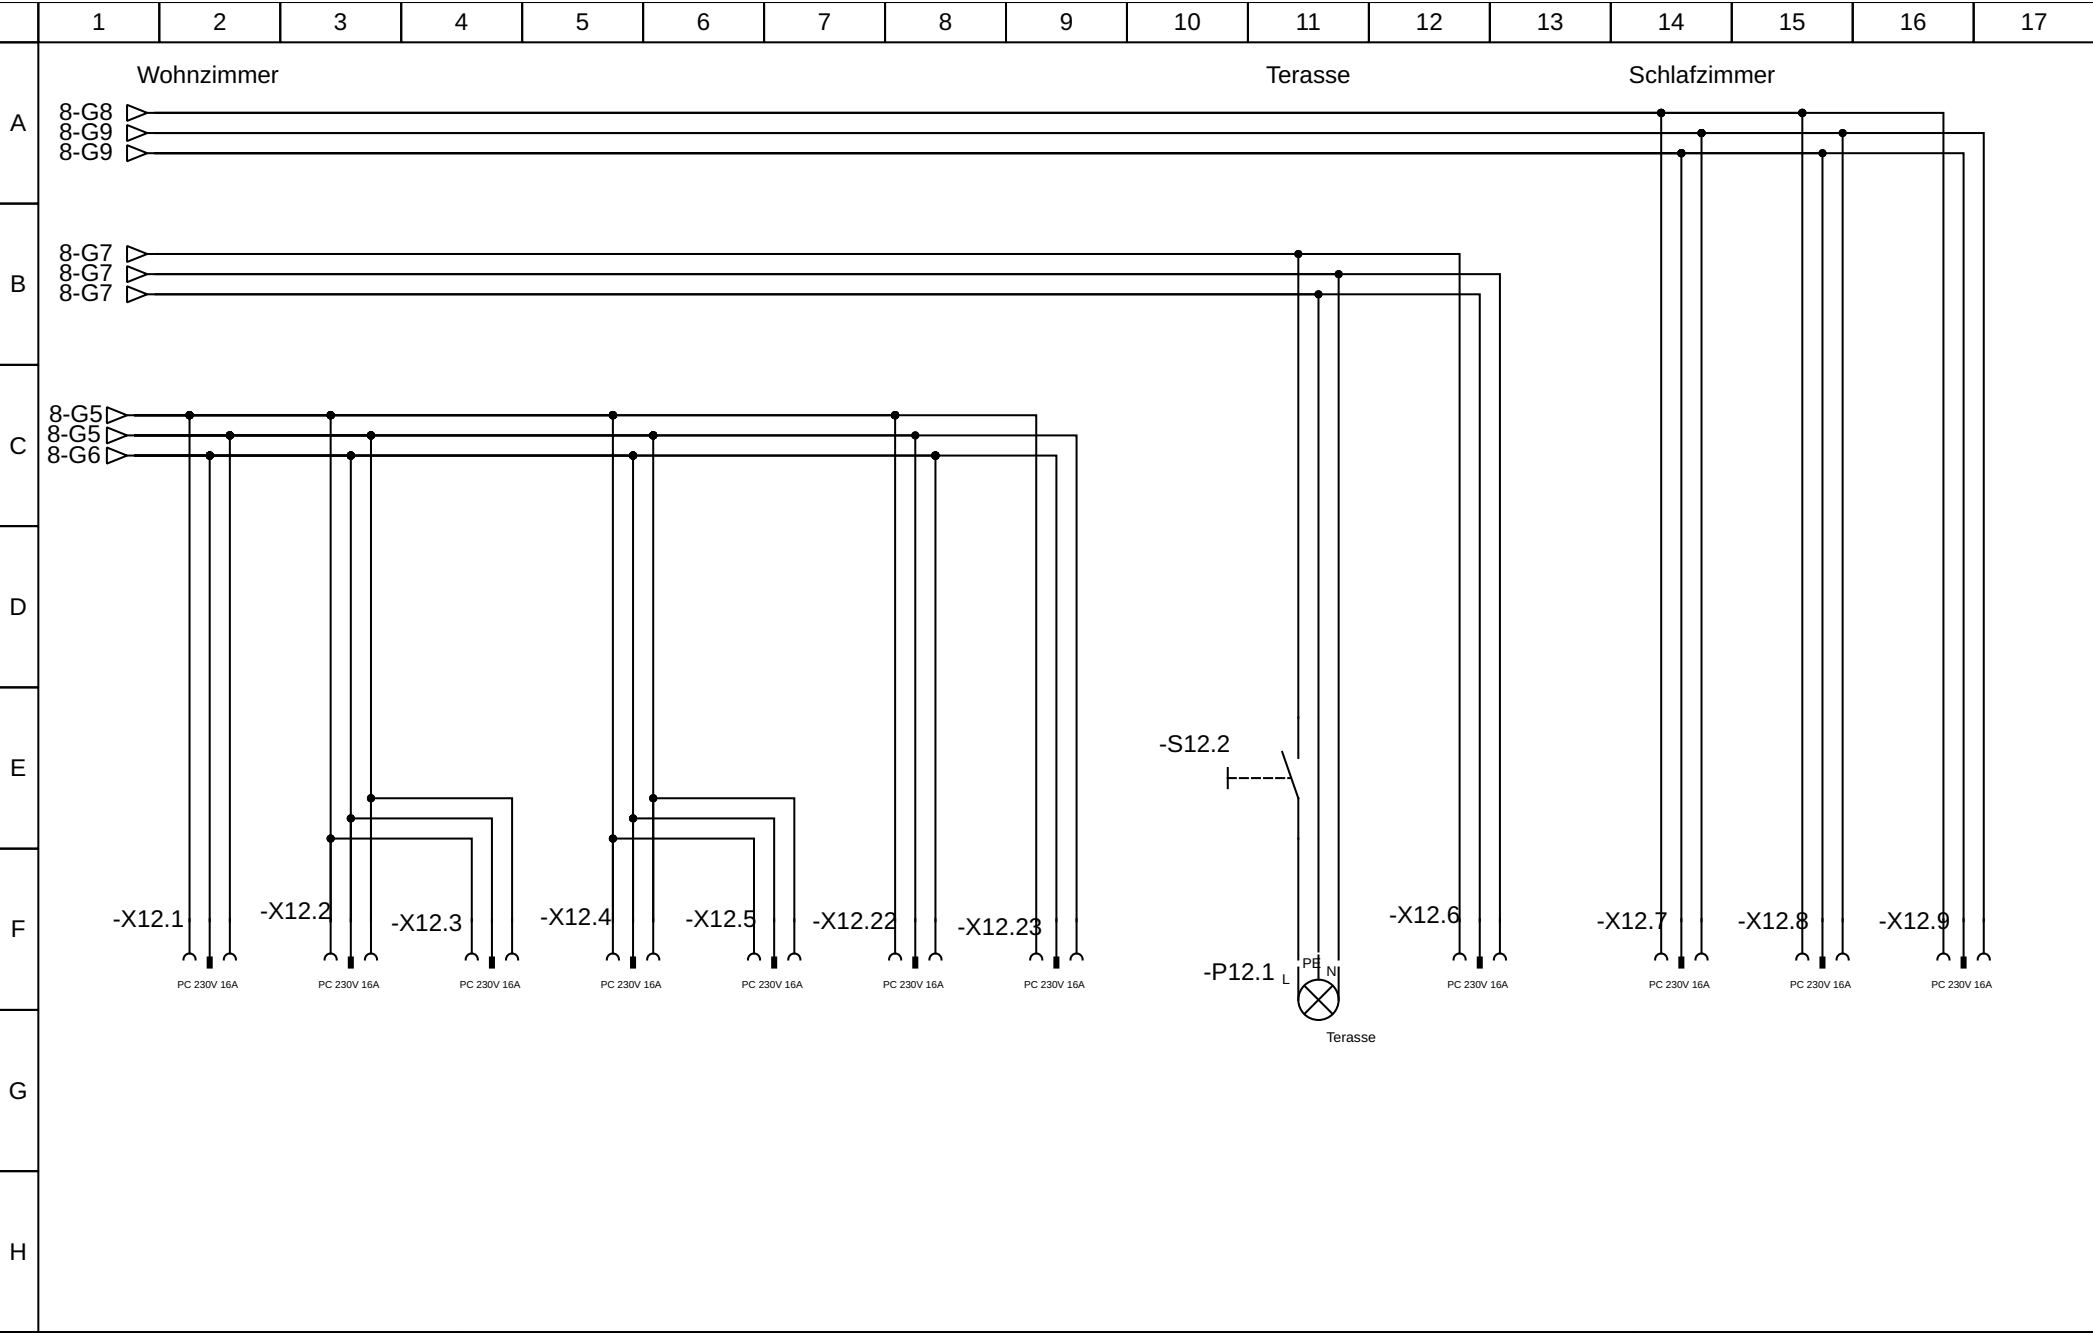

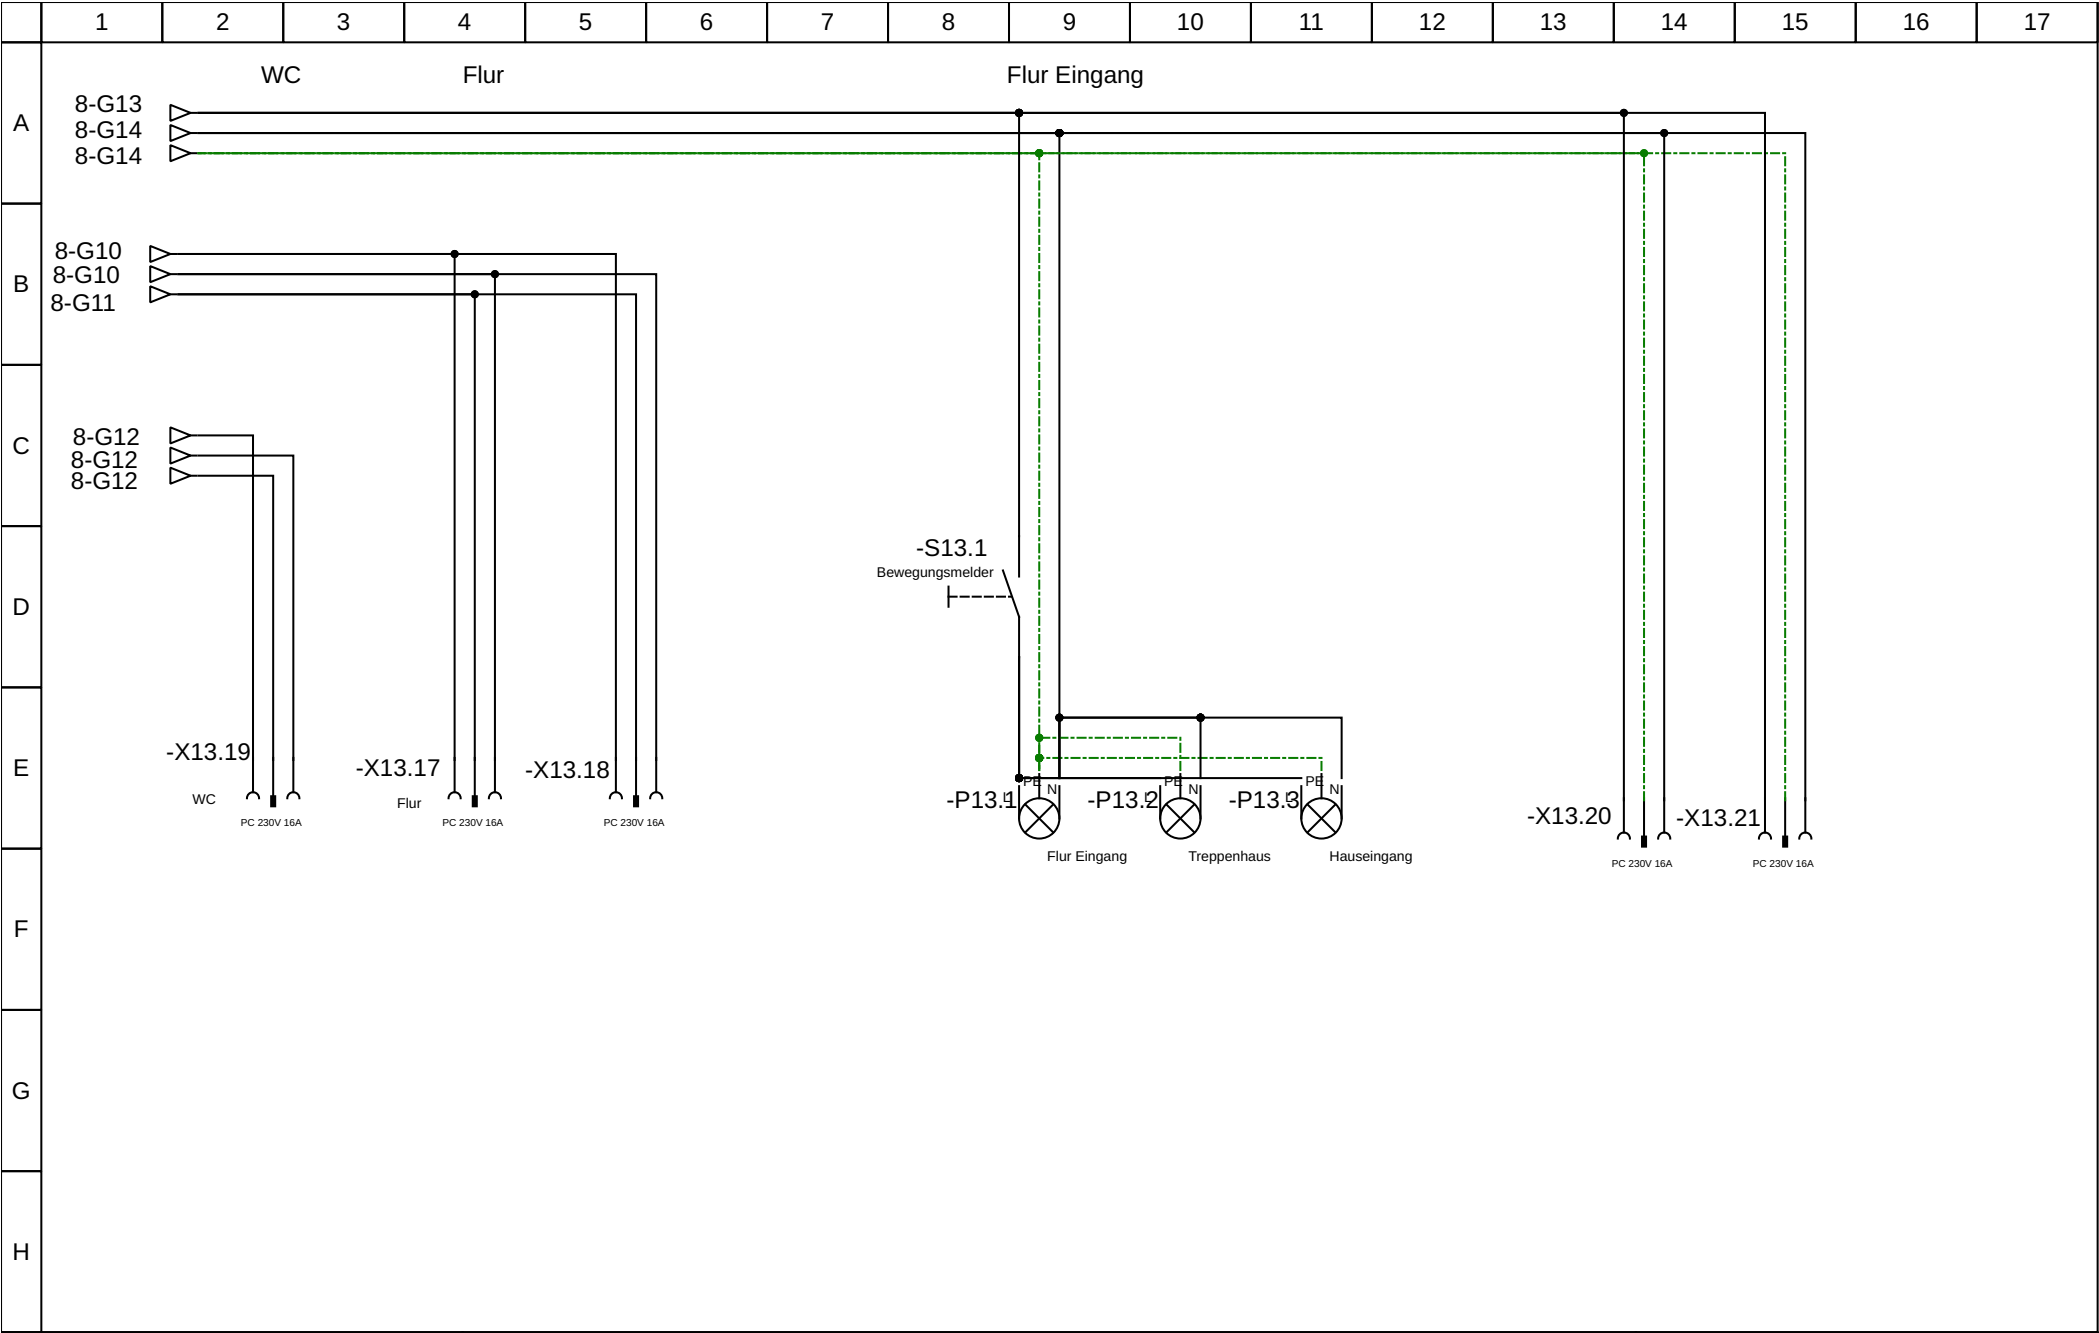


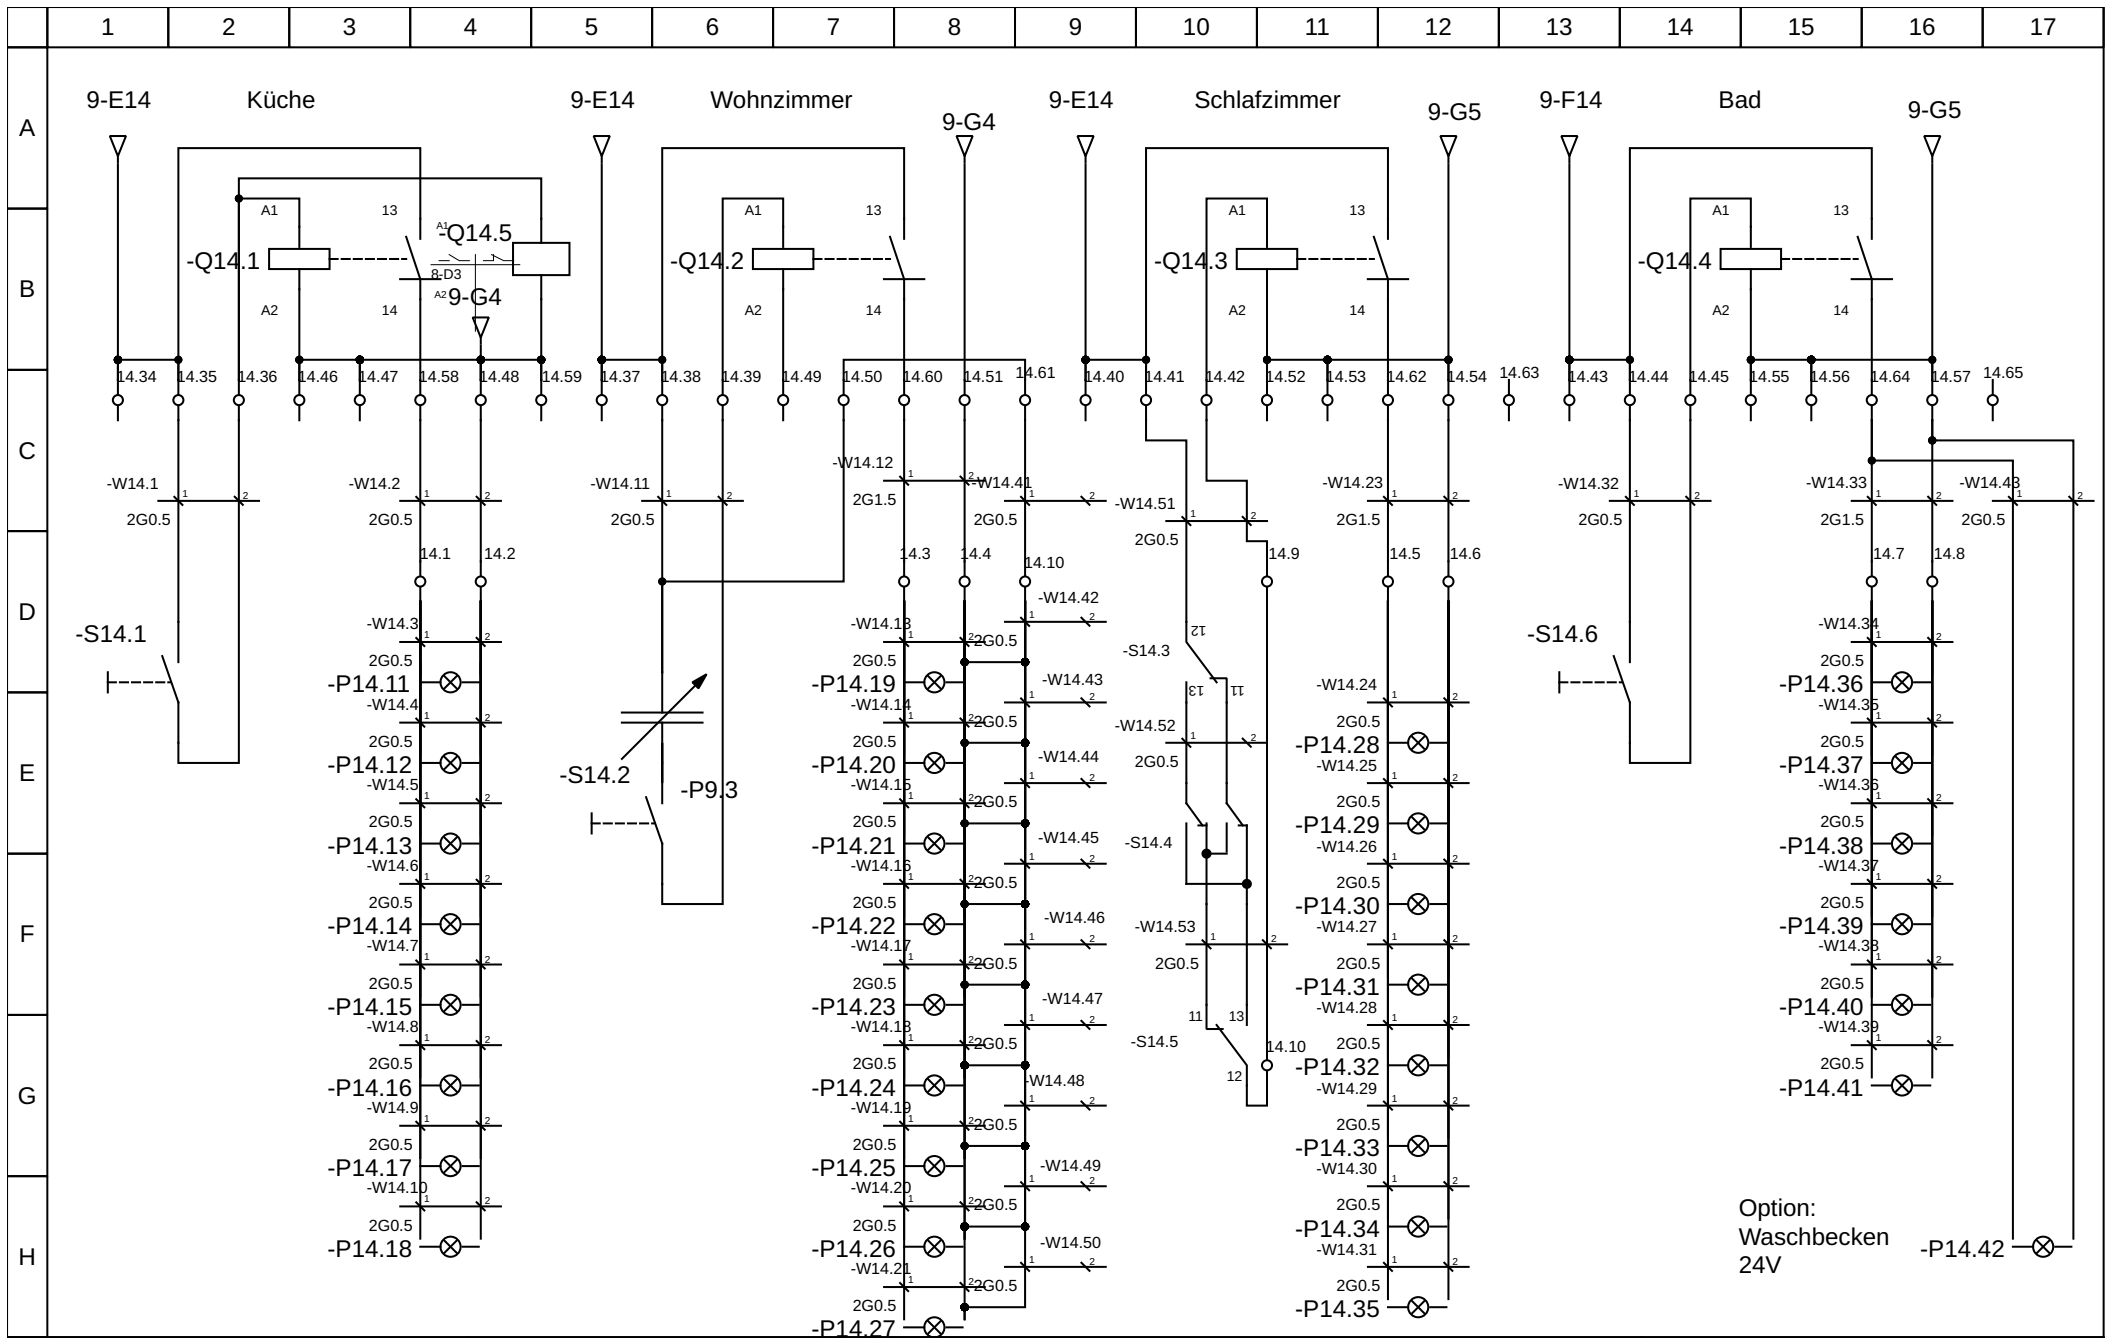


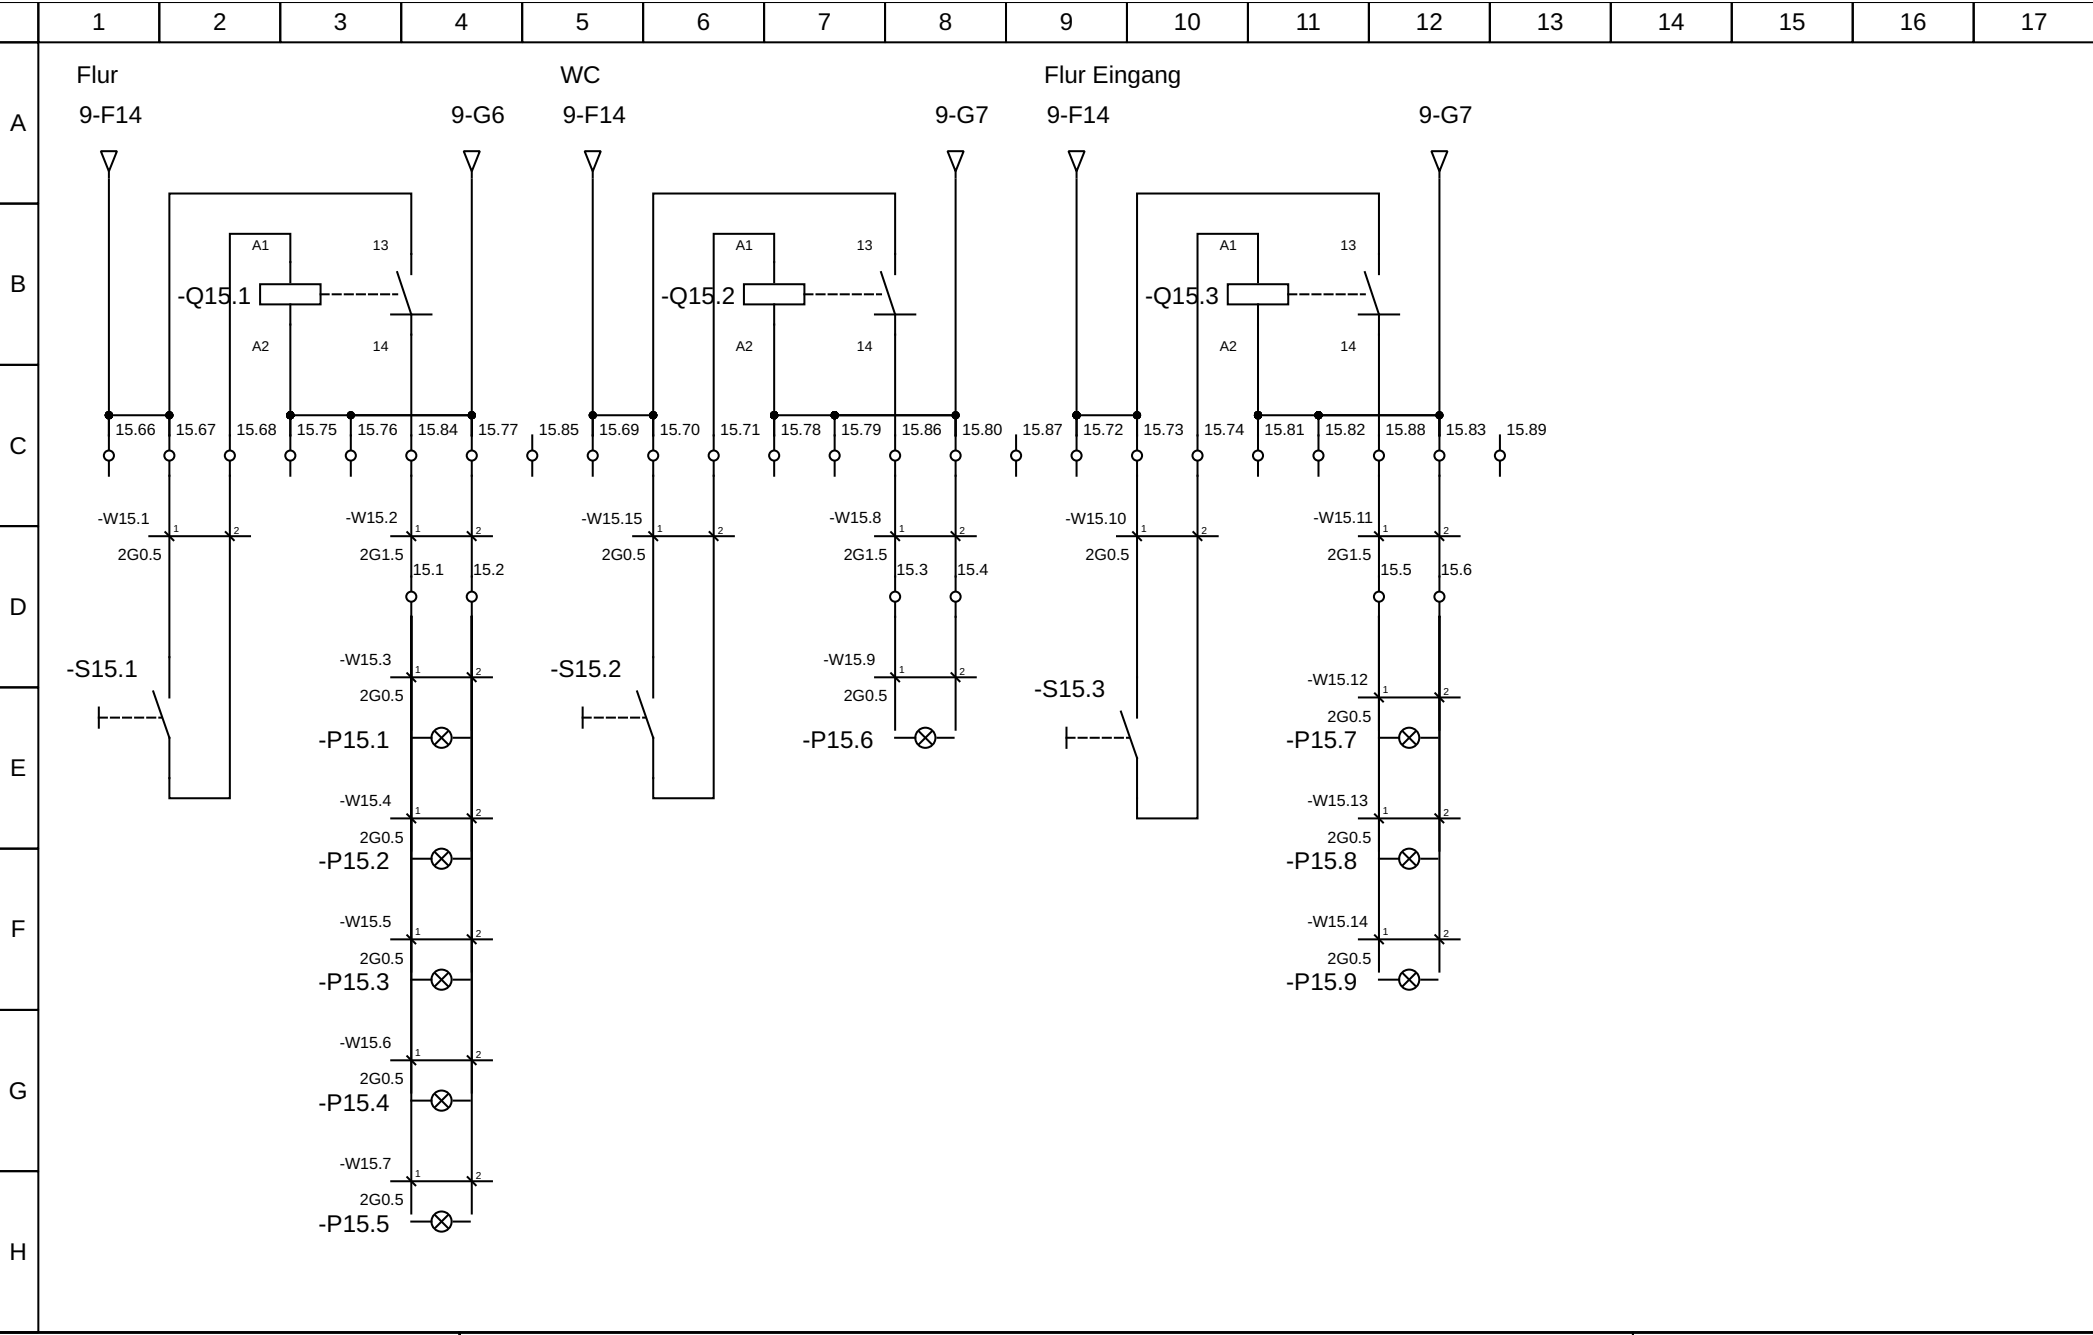


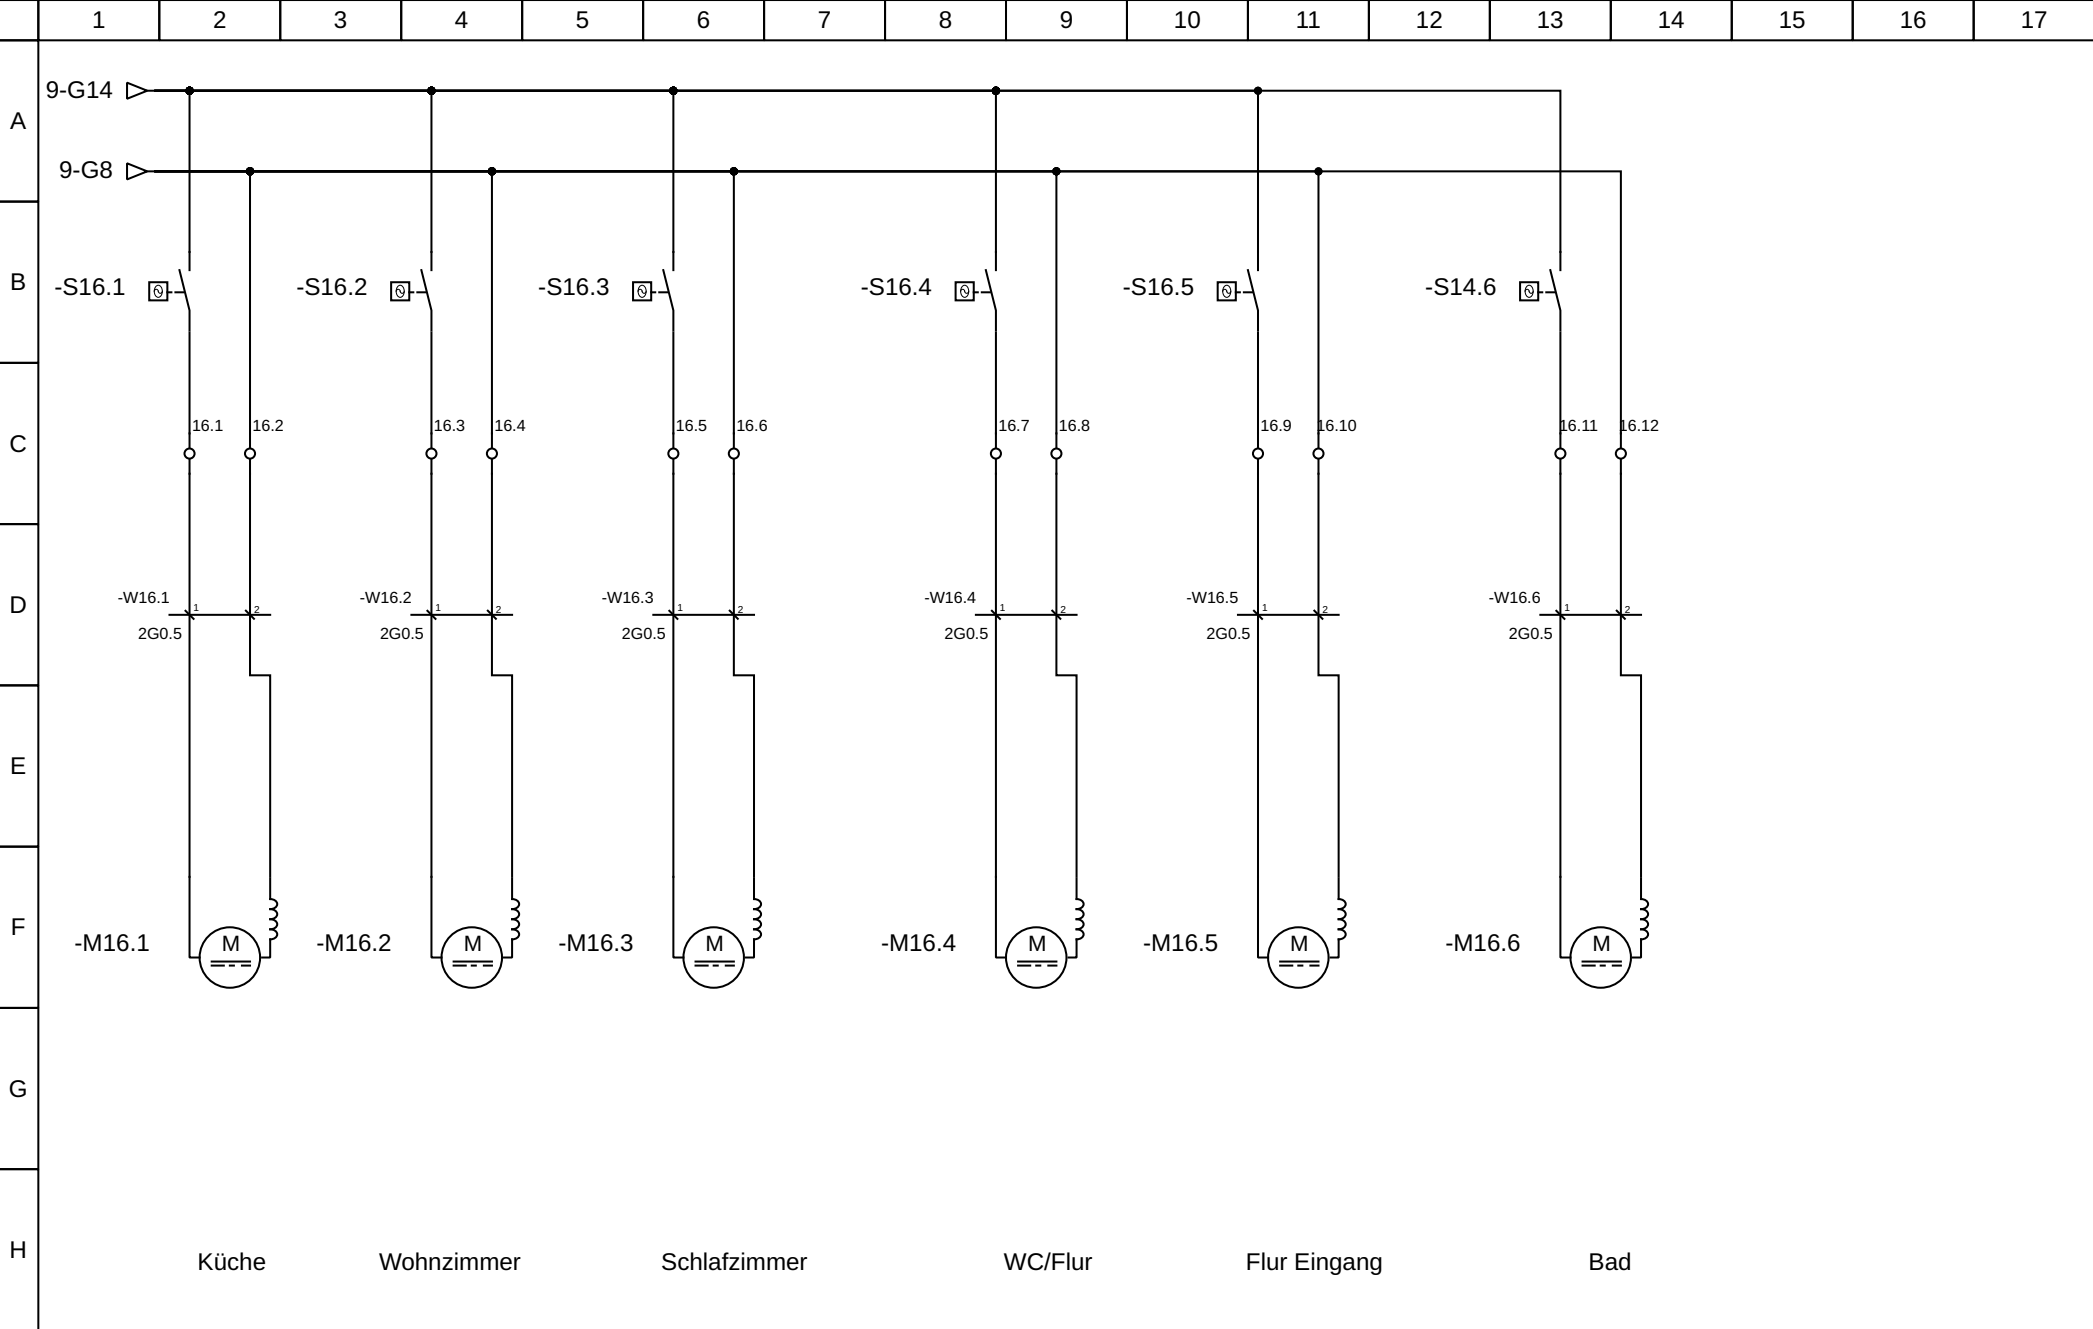



		1	2	3	4	5	6	7	8	9	10	11	12	13	14	15	16	17	
A	B	
EG Verteile X1	
	7/38-E1	7.1	7/38-E9	7.10	7/38-	7.11	7/38-	7.12	7/38-	7.13	7/38-	7.14	7/38-	7.15	7/38-	7.16	7/38-	7.17	7/38-	7.18	7/38-	7.19	7/38-E2	7.2	7/38-	7.20	8/38-	8.31	8/38-	8.32	8/38-D2	8.21	8/38-E3	8.22	8/38-D5	8.23	8/38-D7	8.24	8/38-D8	8.25	8/38-	8.26	8/38-	8.27	8/38-	8.28	8/38-	8.29	8/38-	8.30	7/38-E2	7.3	7/38-E4	7.4	7/38-E4	7.5	7/38-E5	7.6	7/38-E7	7.7	7/38-E7	7.8	7/38-E7	7.9	19/38-	19.1	19/38-	19.10	19/38-	19.11	19/38-	19.12	19/38-	19.13	19/38-	19.14	19/38-	19.15	19/38-	19.16	19/38-	19.17	19/38-	19.18	19/38-	19.19	19/38-	19.2	19/38-	19.3	19/38-	19.4	19/38-	19.5	19/38-	19.6
C	D	E	F	G	H	
EG Verteile X2 - 24V+	
	14/38-	14.34	14/38-	14.35	14/38-	14.36	14/38-	14.37	14/38-	14.38	14/38-	14.39	14/38-	14.40	14/38-	14.41	14/38-	14.42	14/38-	14.43	14/38-	14.44	14/38-	14.45	15/38-	15.66	15/38-	15.67	15/38-	15.68	15/38-	15.69	15/38-	15.70	15/38-	15.71	15/38-	15.72	15/38-	15.73	15/38-	15.74	
EG Verteile X2 - 24V-	
	14/38-	14.46	14/38-	14.47	14/38-	14.48	14/38-	14.49	14/38-	14.50	14/38-	14.51	14/38-	14.52	14/38-	14.53	14/38-	14.54	14/38-	14.55	14/38-	14.56	14/38-	14.57	15/38-	15.75	15/38-	15.76	15/38-	15.77	15/38-	15.78	15/38-	15.79	15/38-	15.80	15/38-	15.81	15/38-	15.82	15/38-	15.83	
EG Verteile X2 - 24V	
	14/38-	14.58	14/38-	14.59	14/38-	14.60	14/38-	14.61	14/38-	14.62	14/38-	14.63	14/38-	14.64	14/38-	14.65	15/38-	15.84	15/38-	15.85	15/38-	15.86	15/38-	15.87	15/38-	15.88	15/38-	15.89	
Autor: Enrich					Klemmenplan												Datei:	
Datum:																	Seite: 18/38	

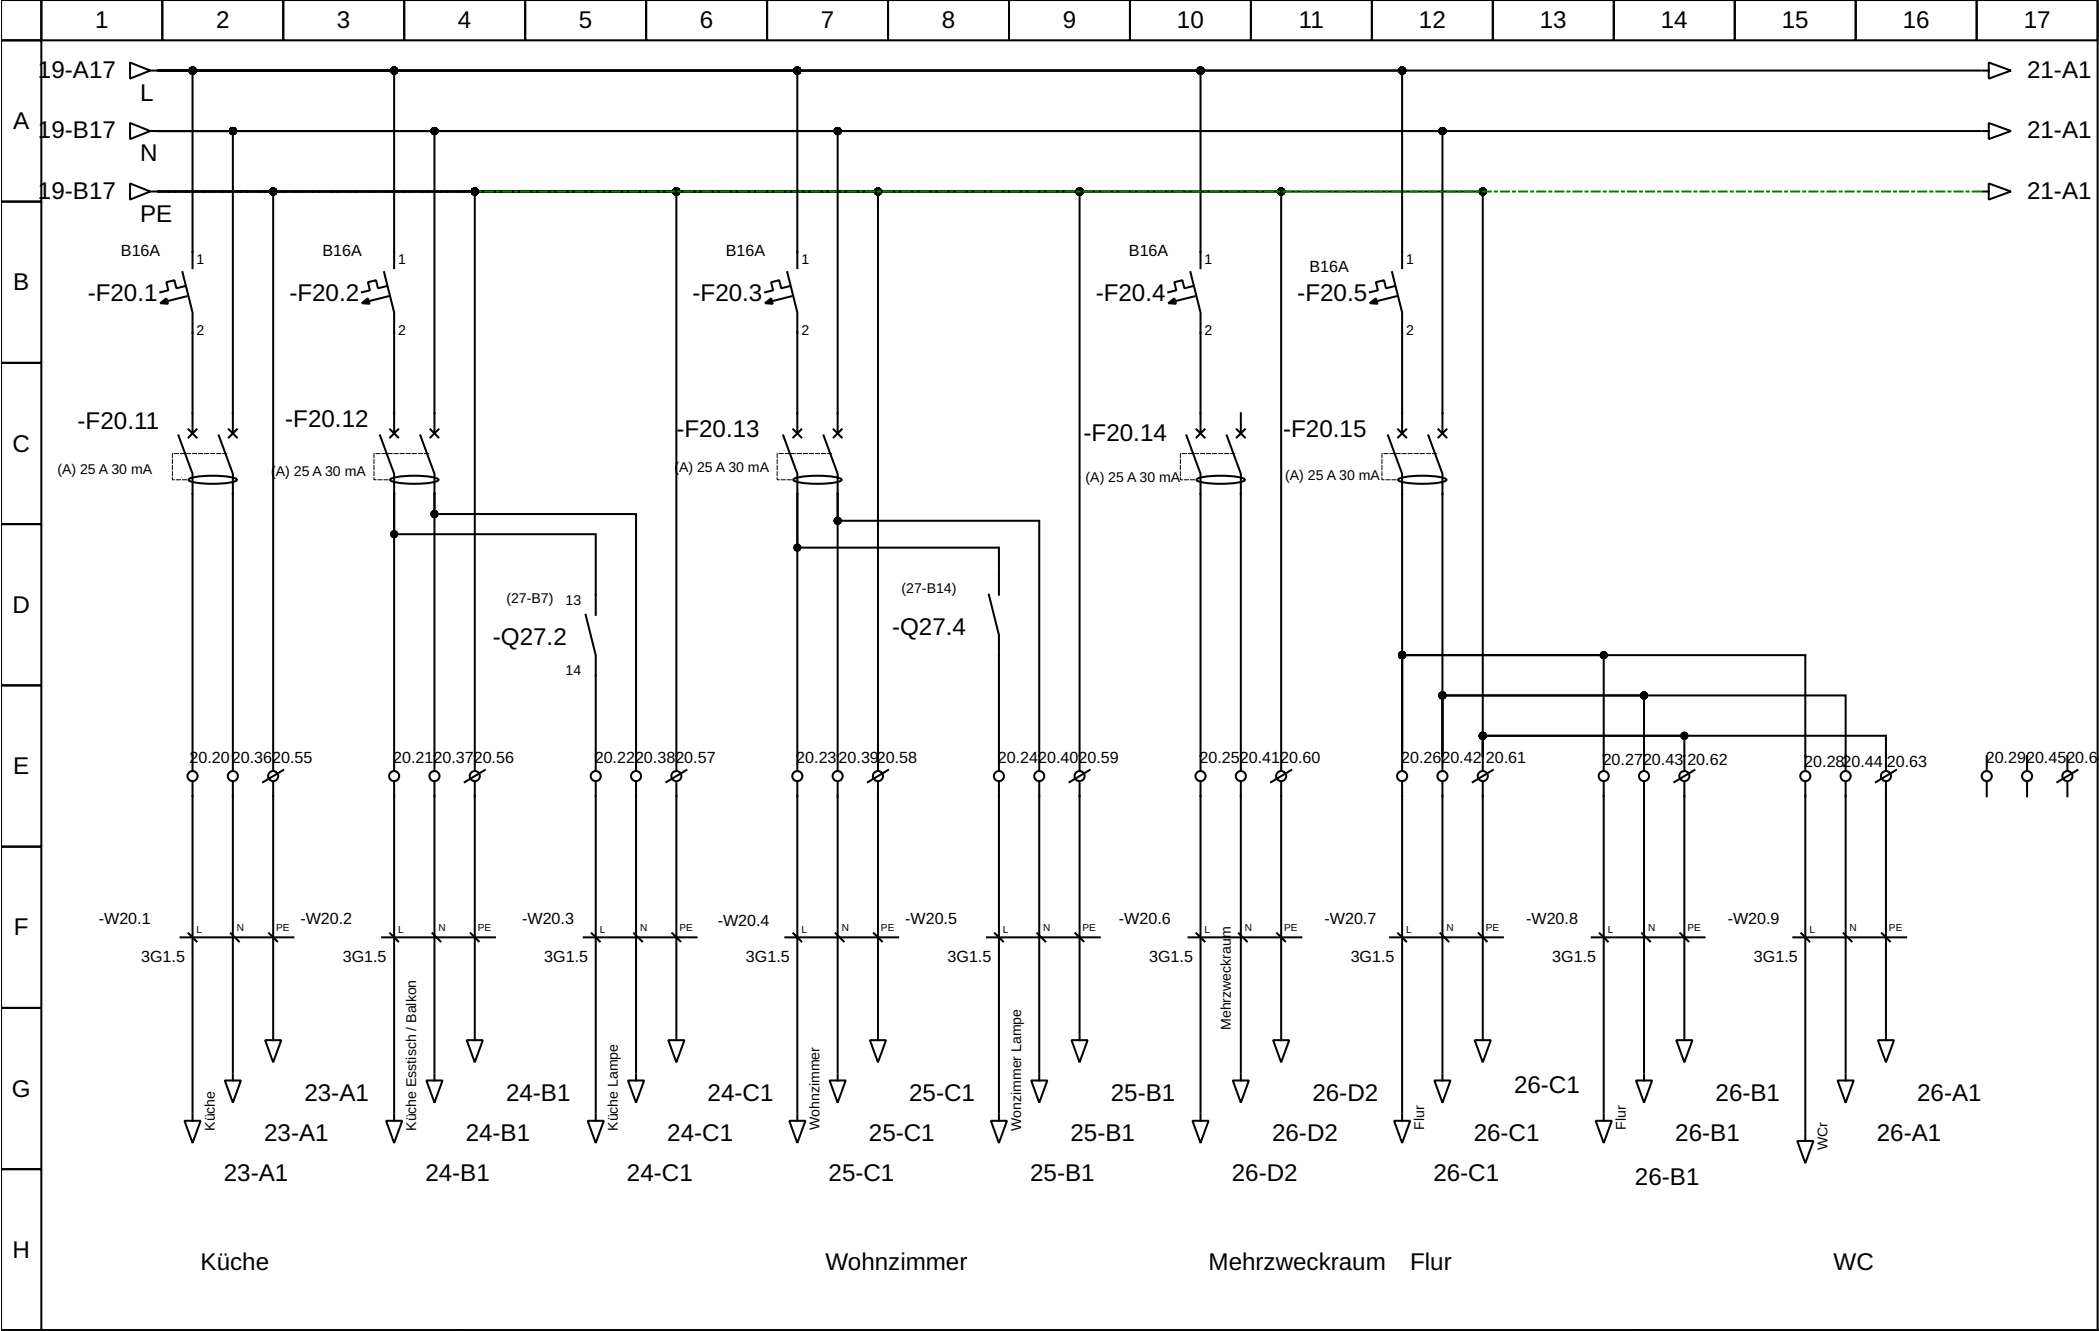


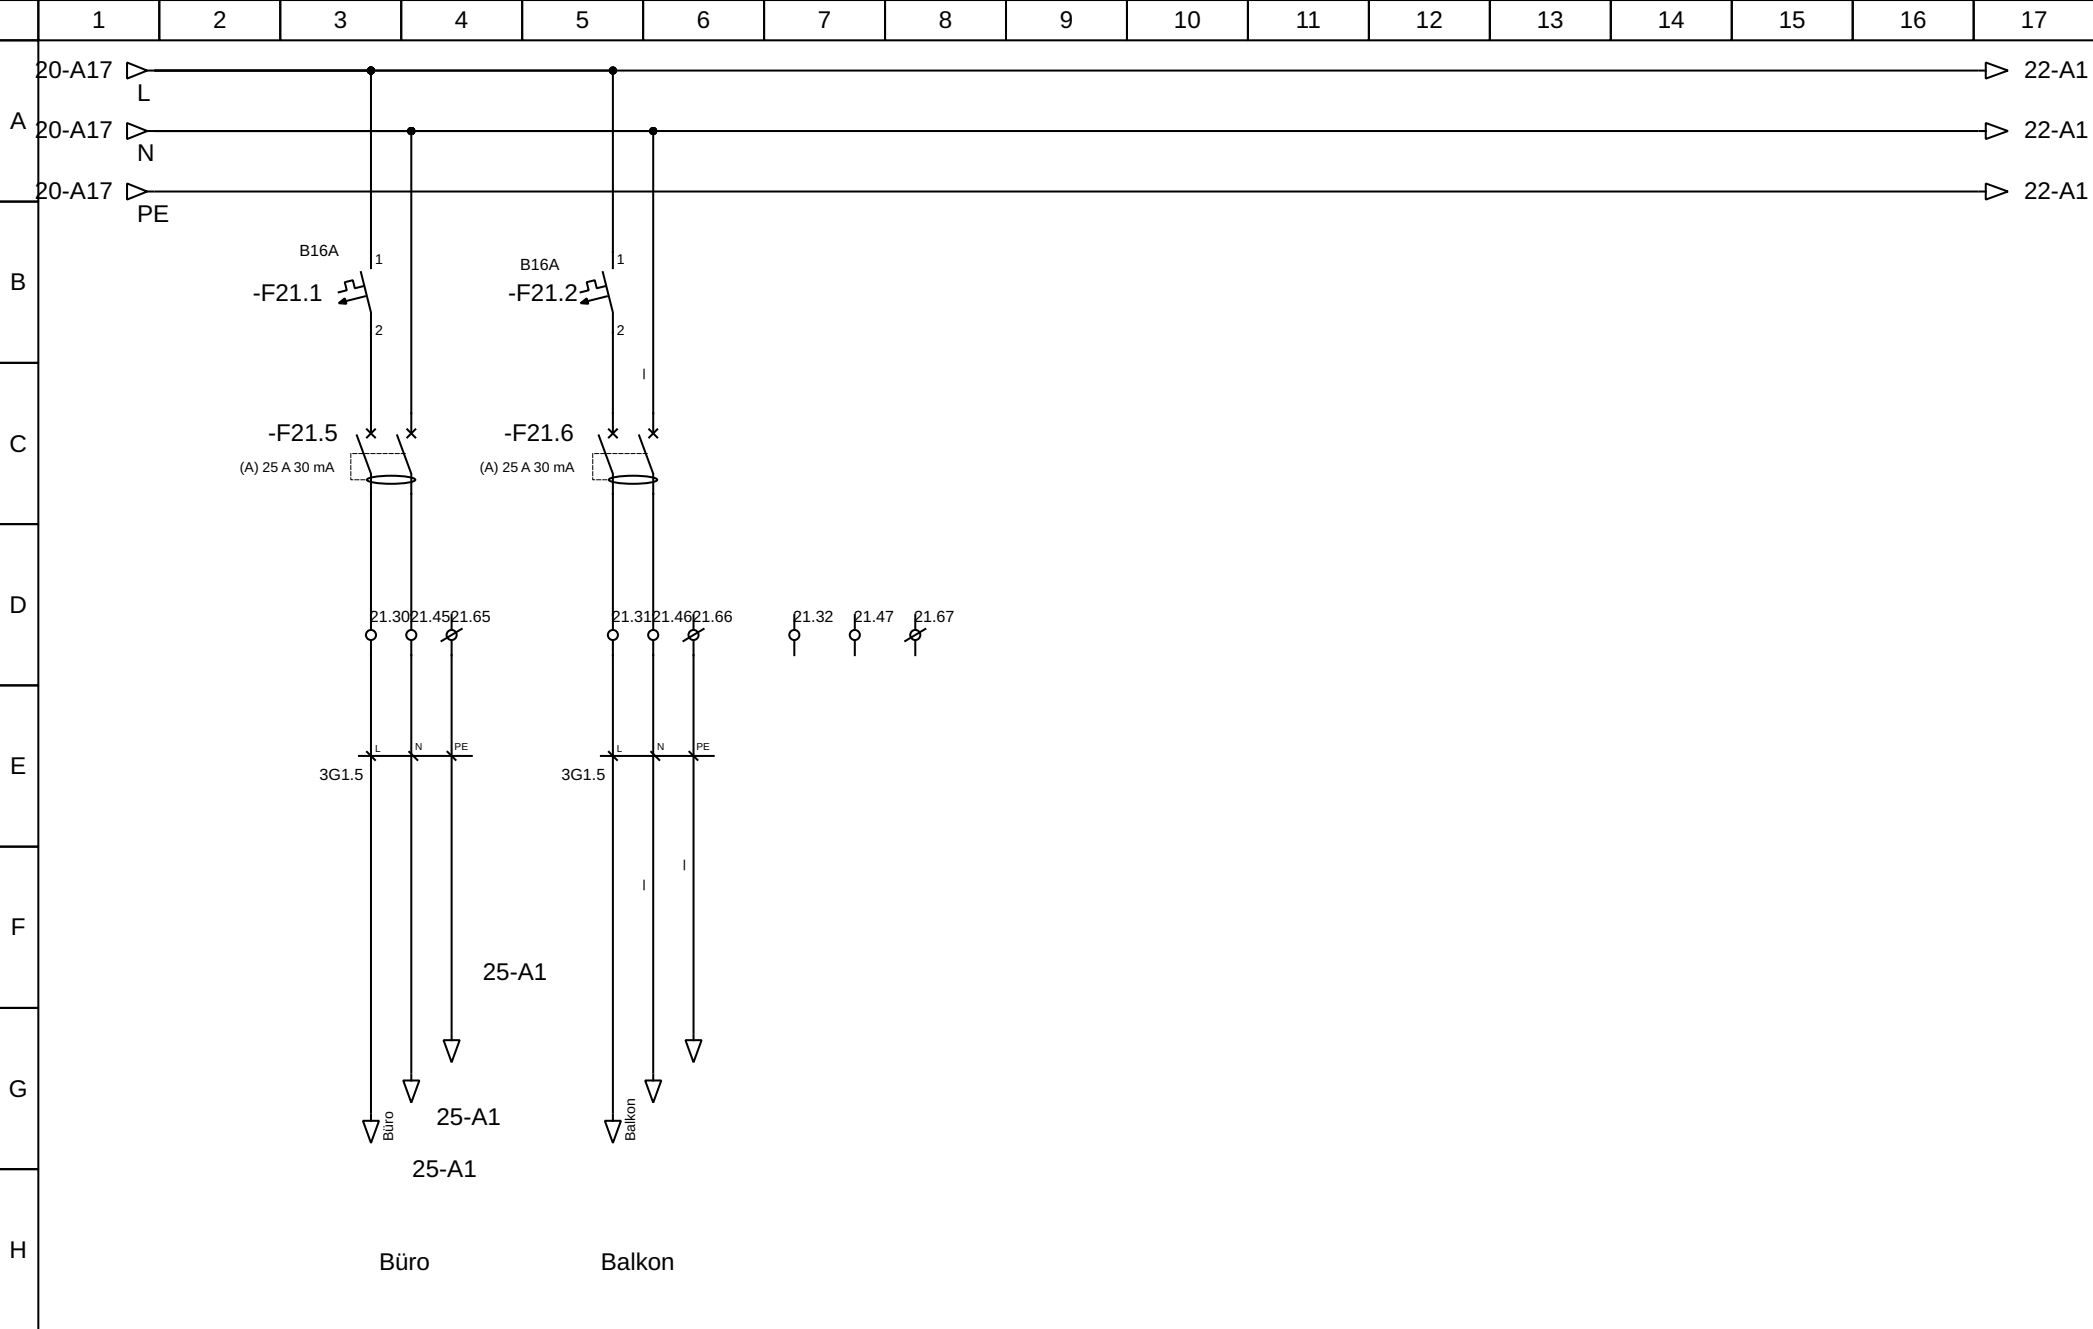


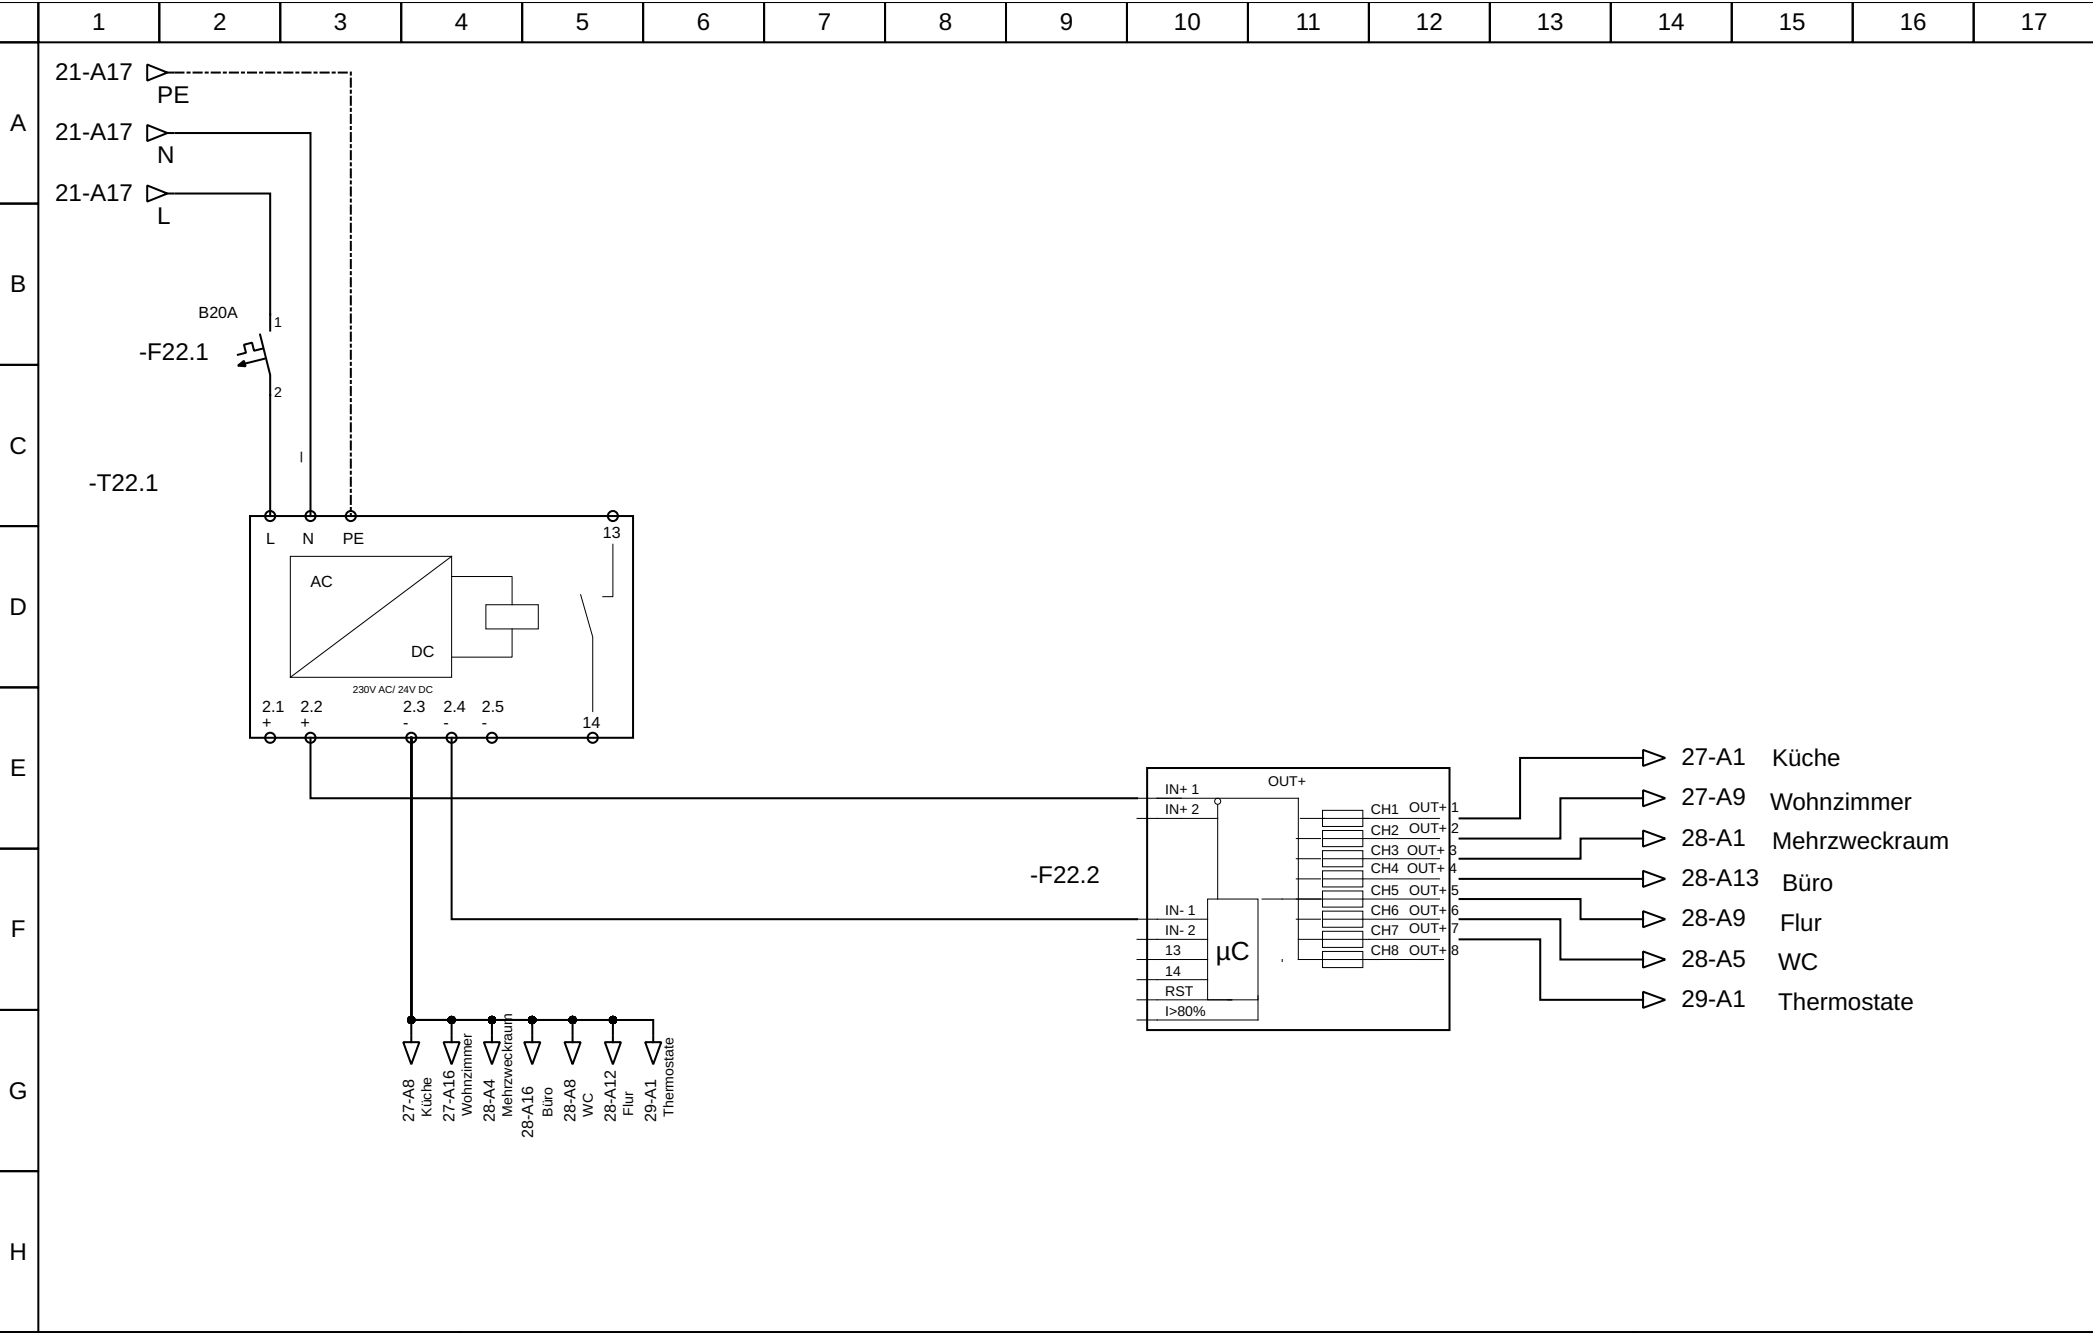


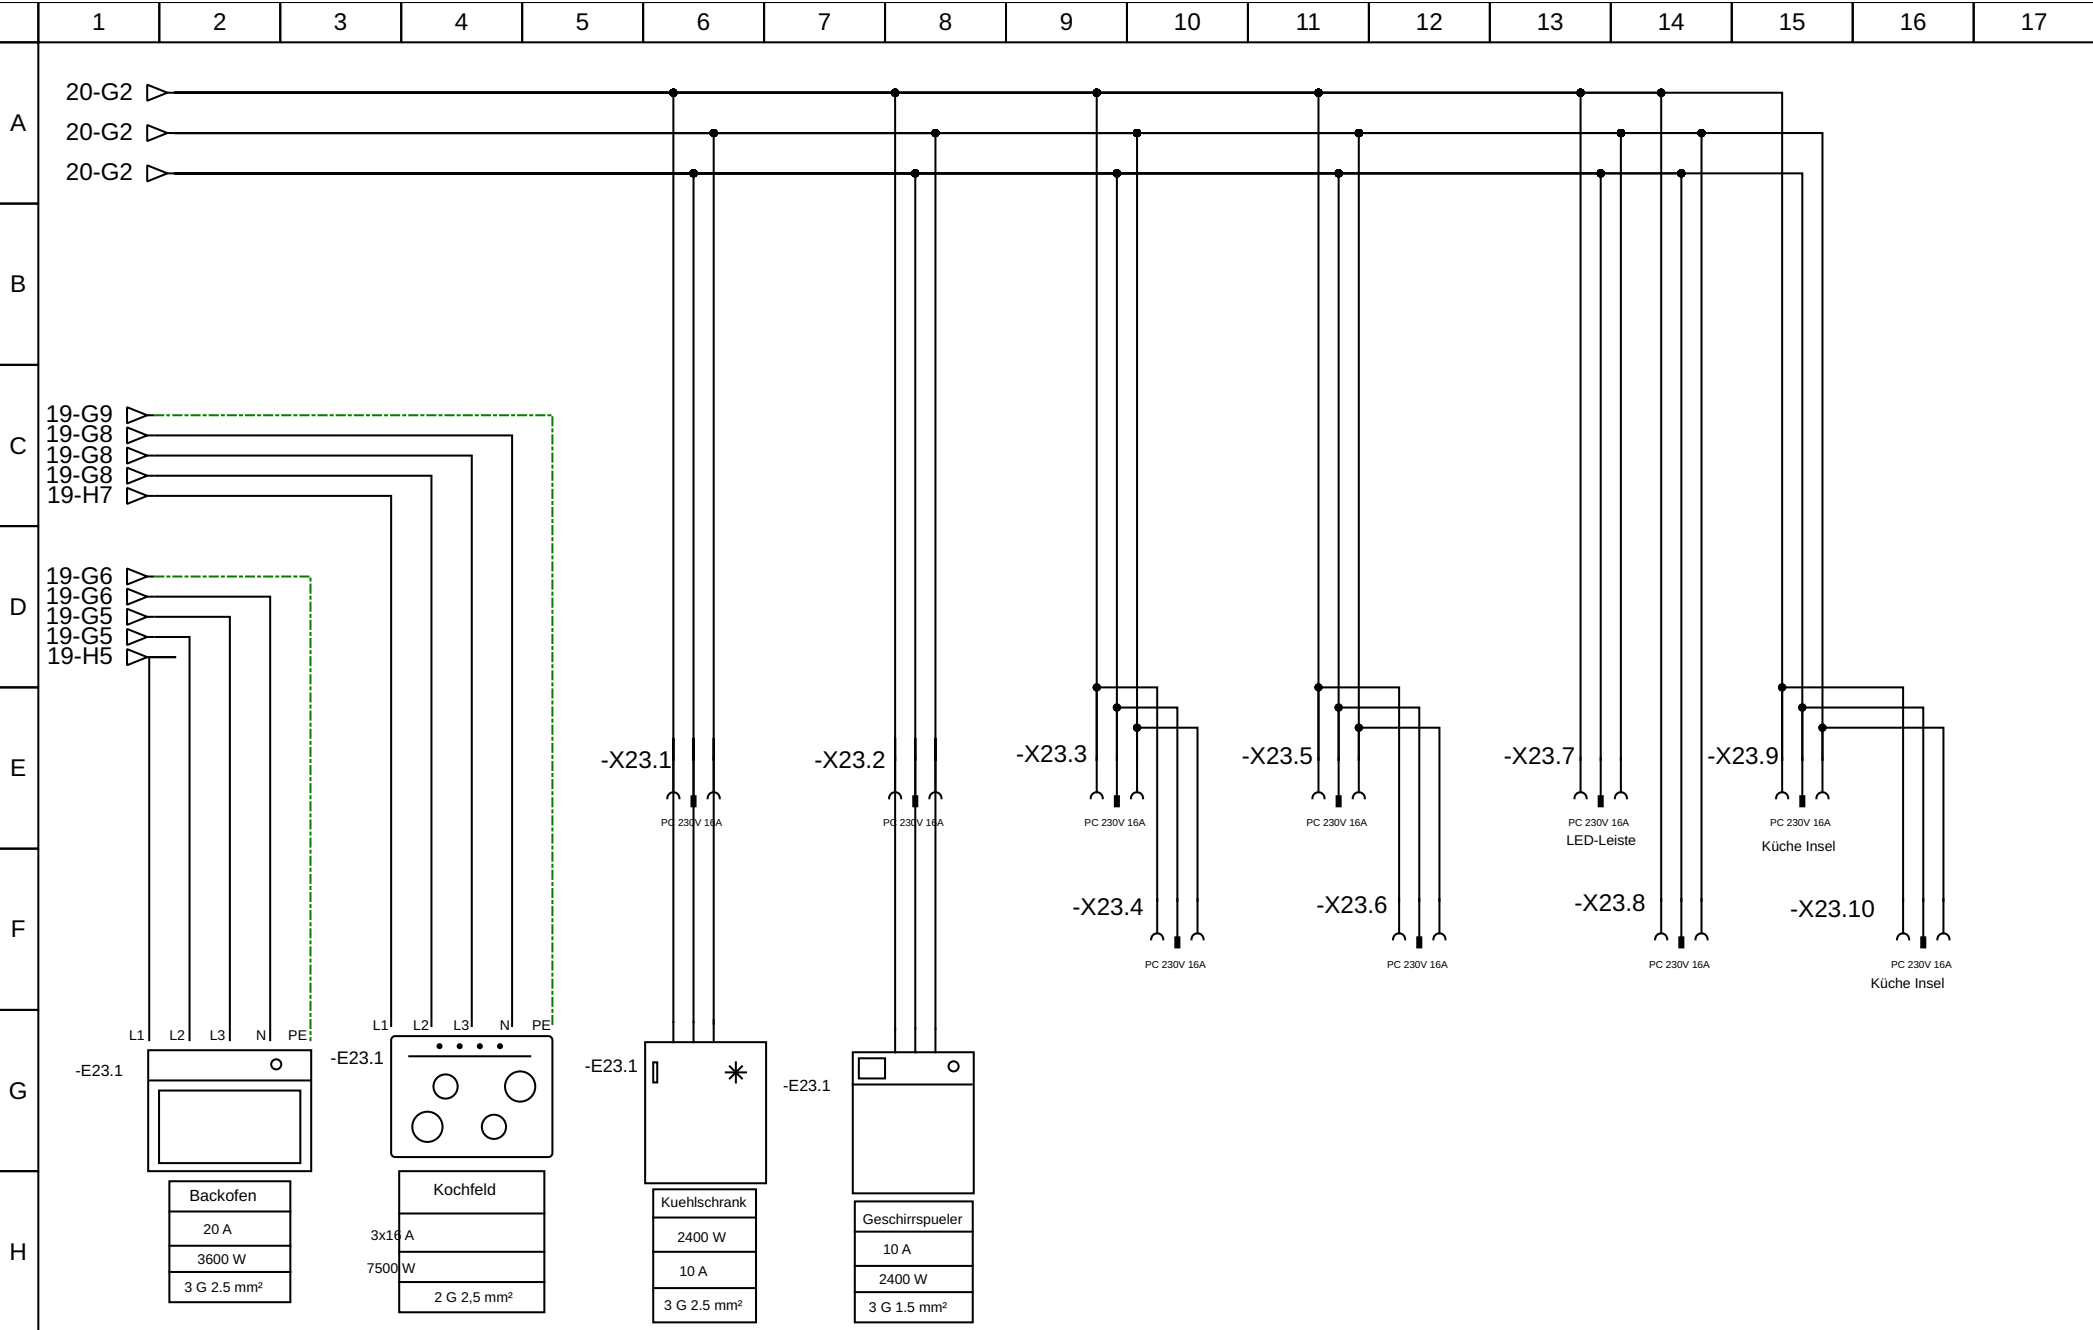


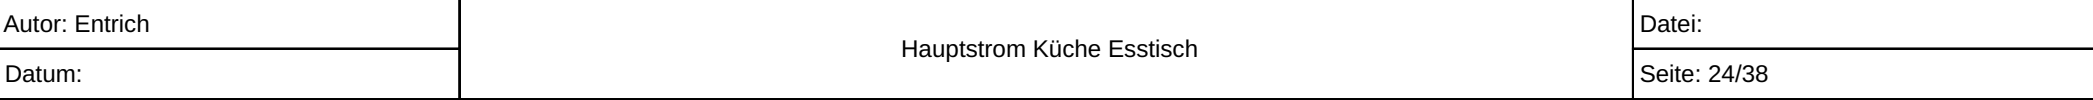


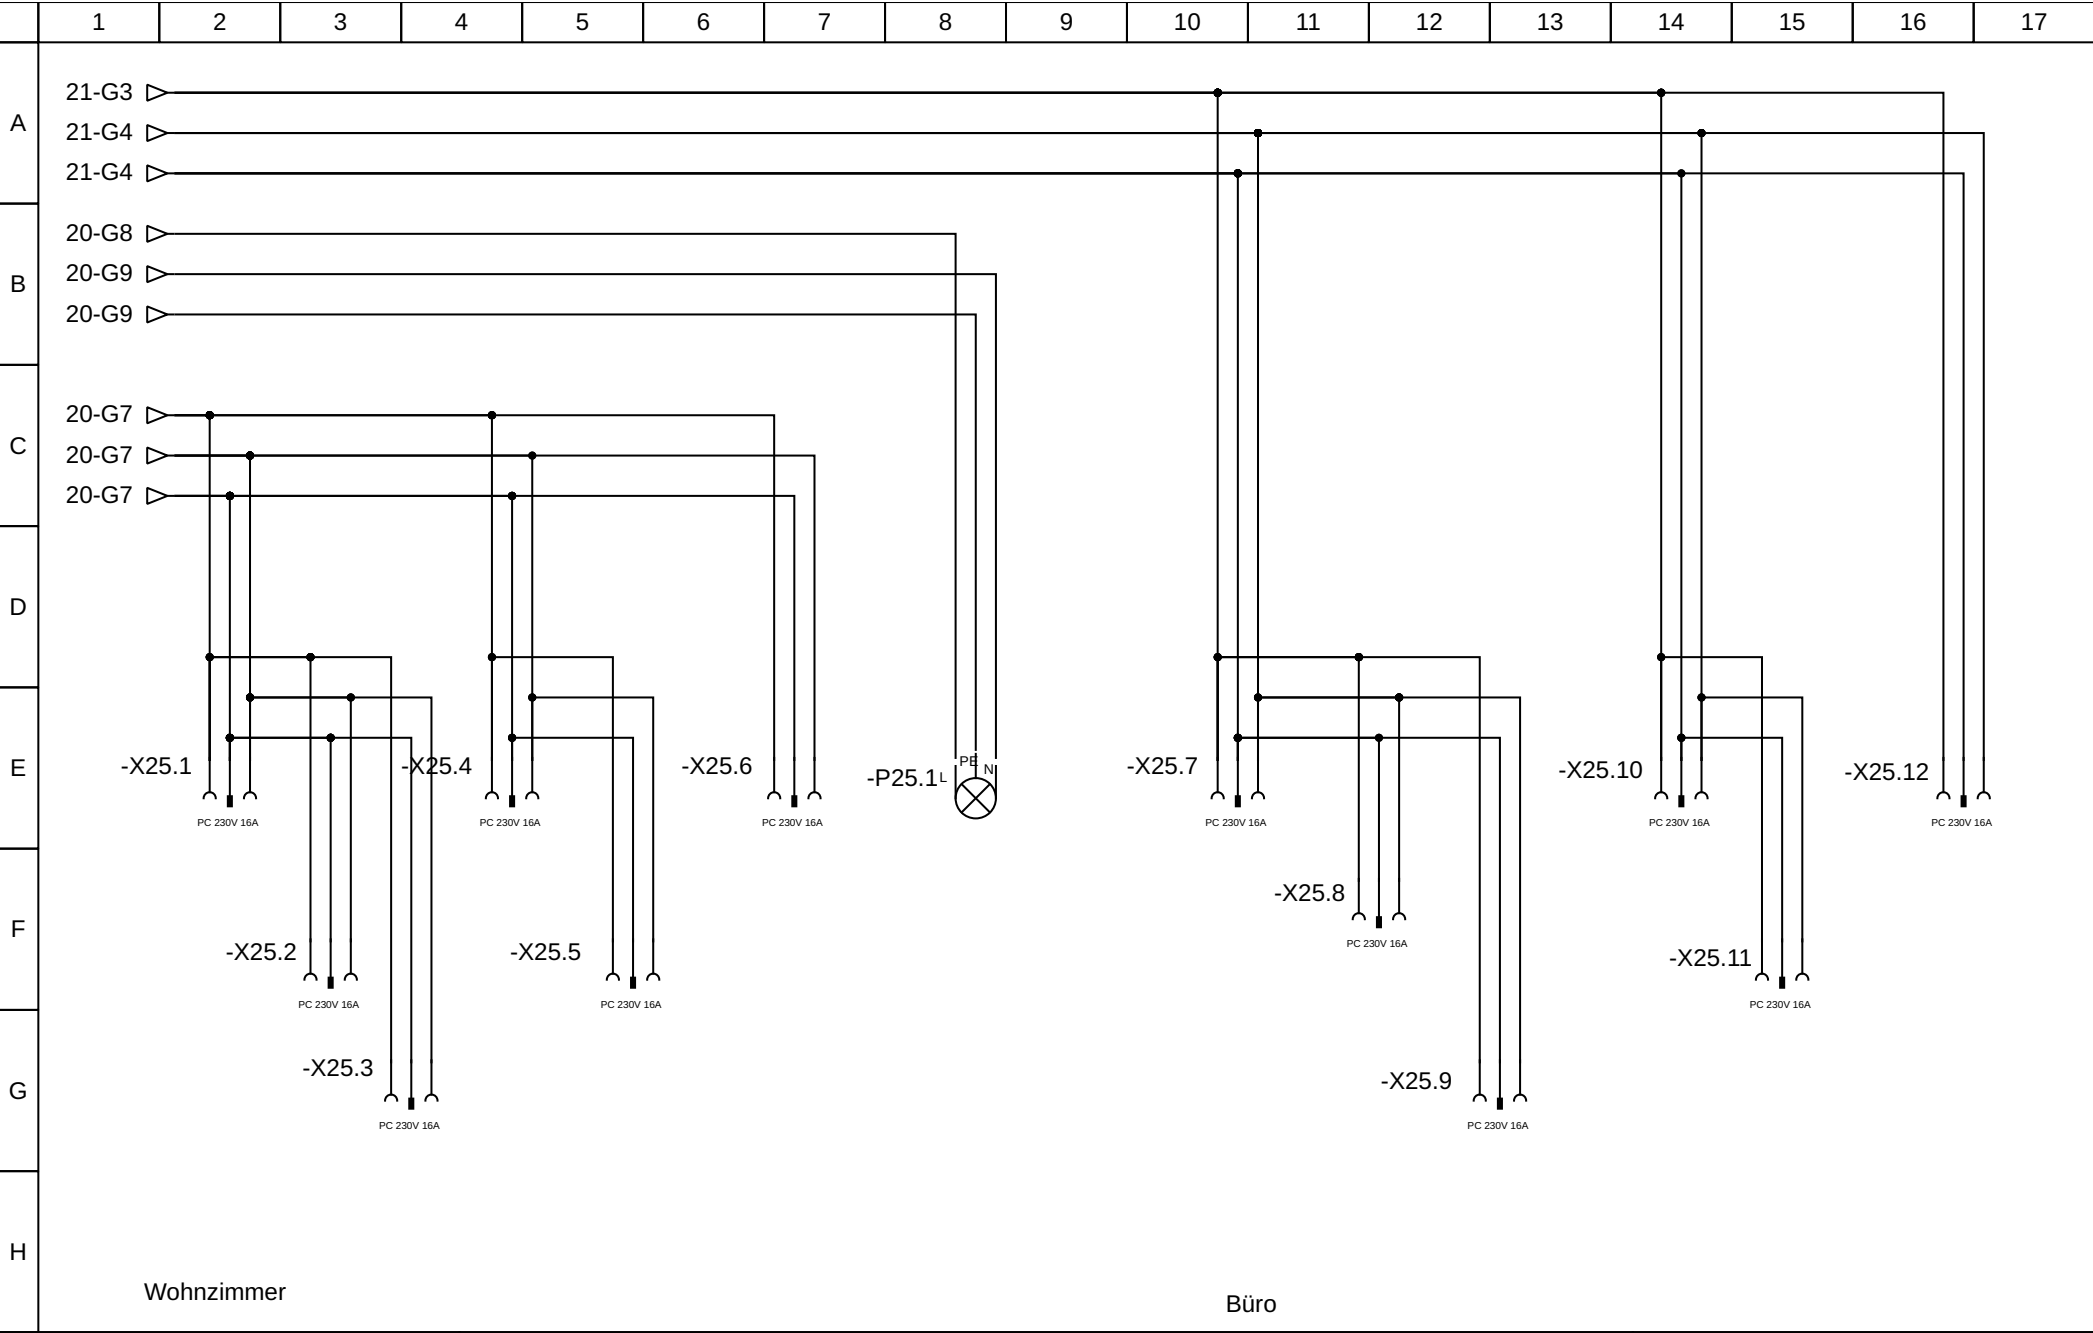

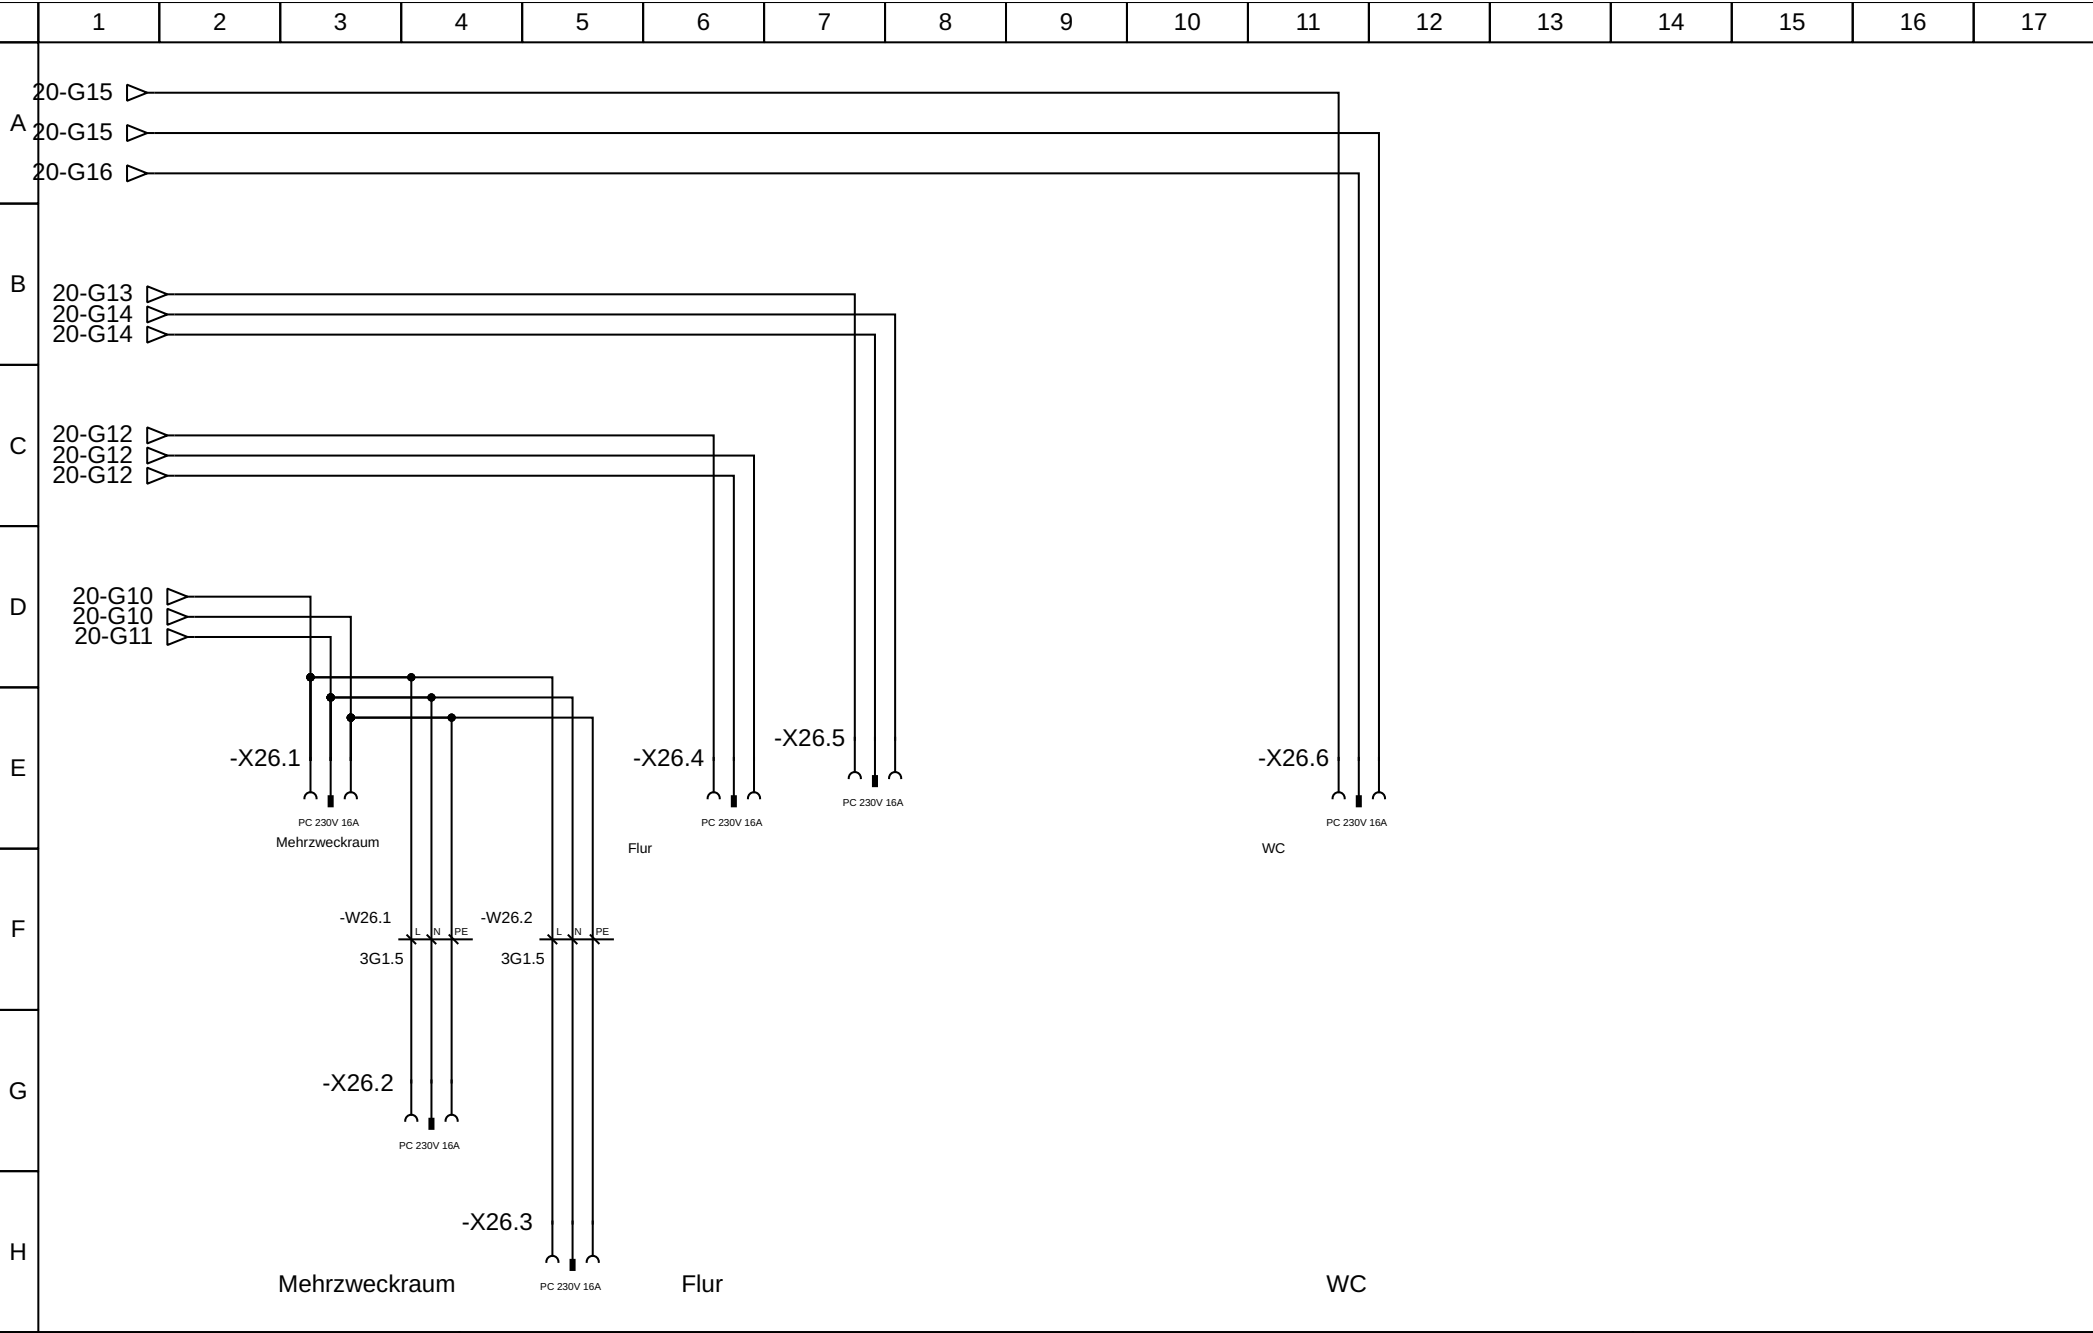

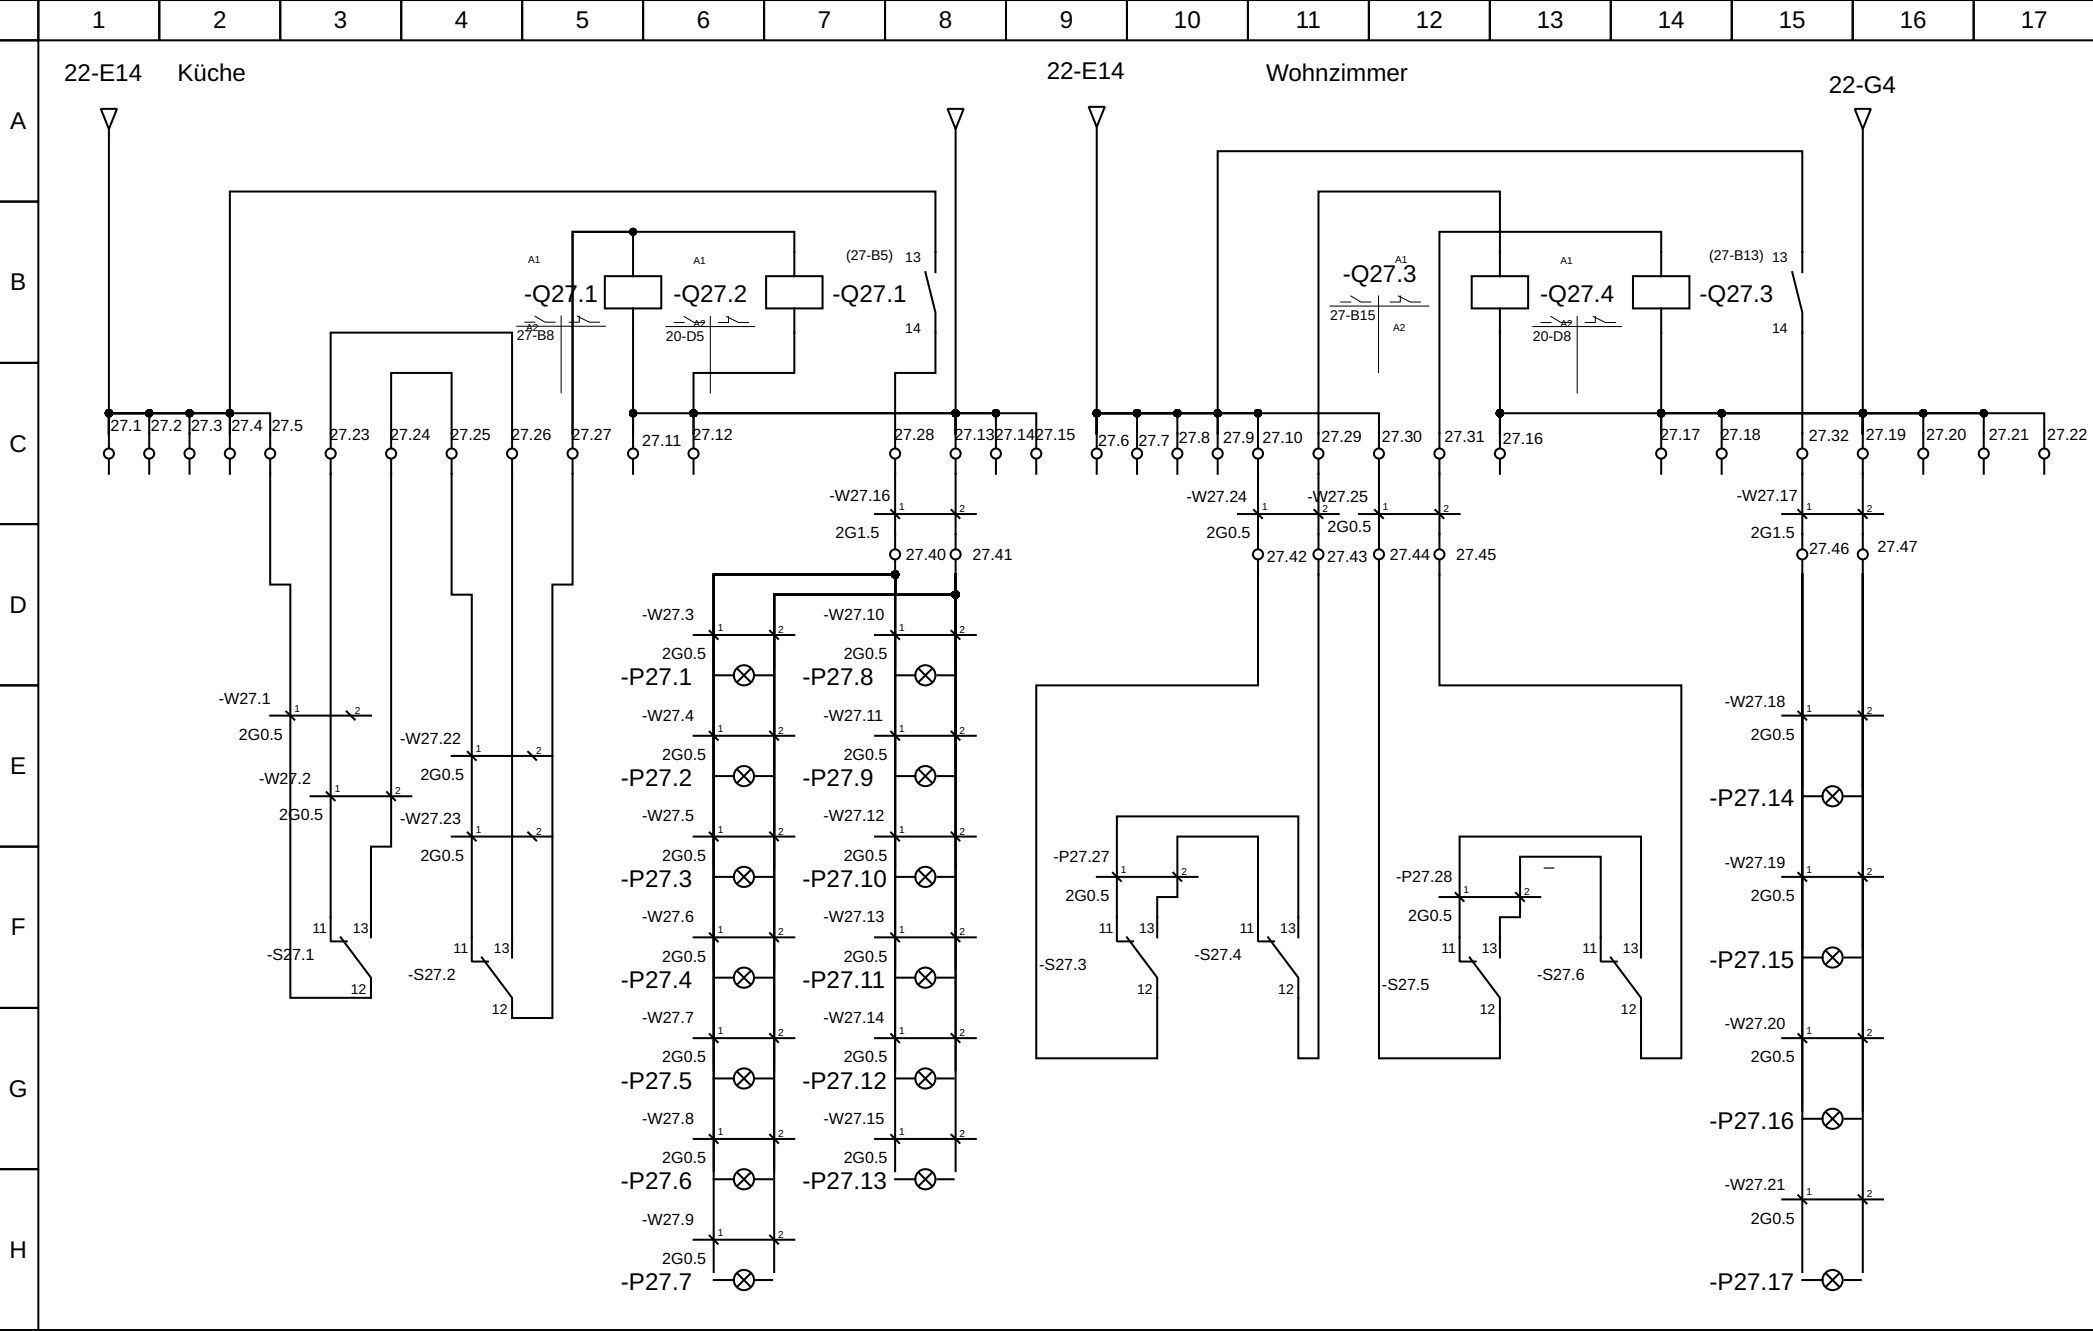


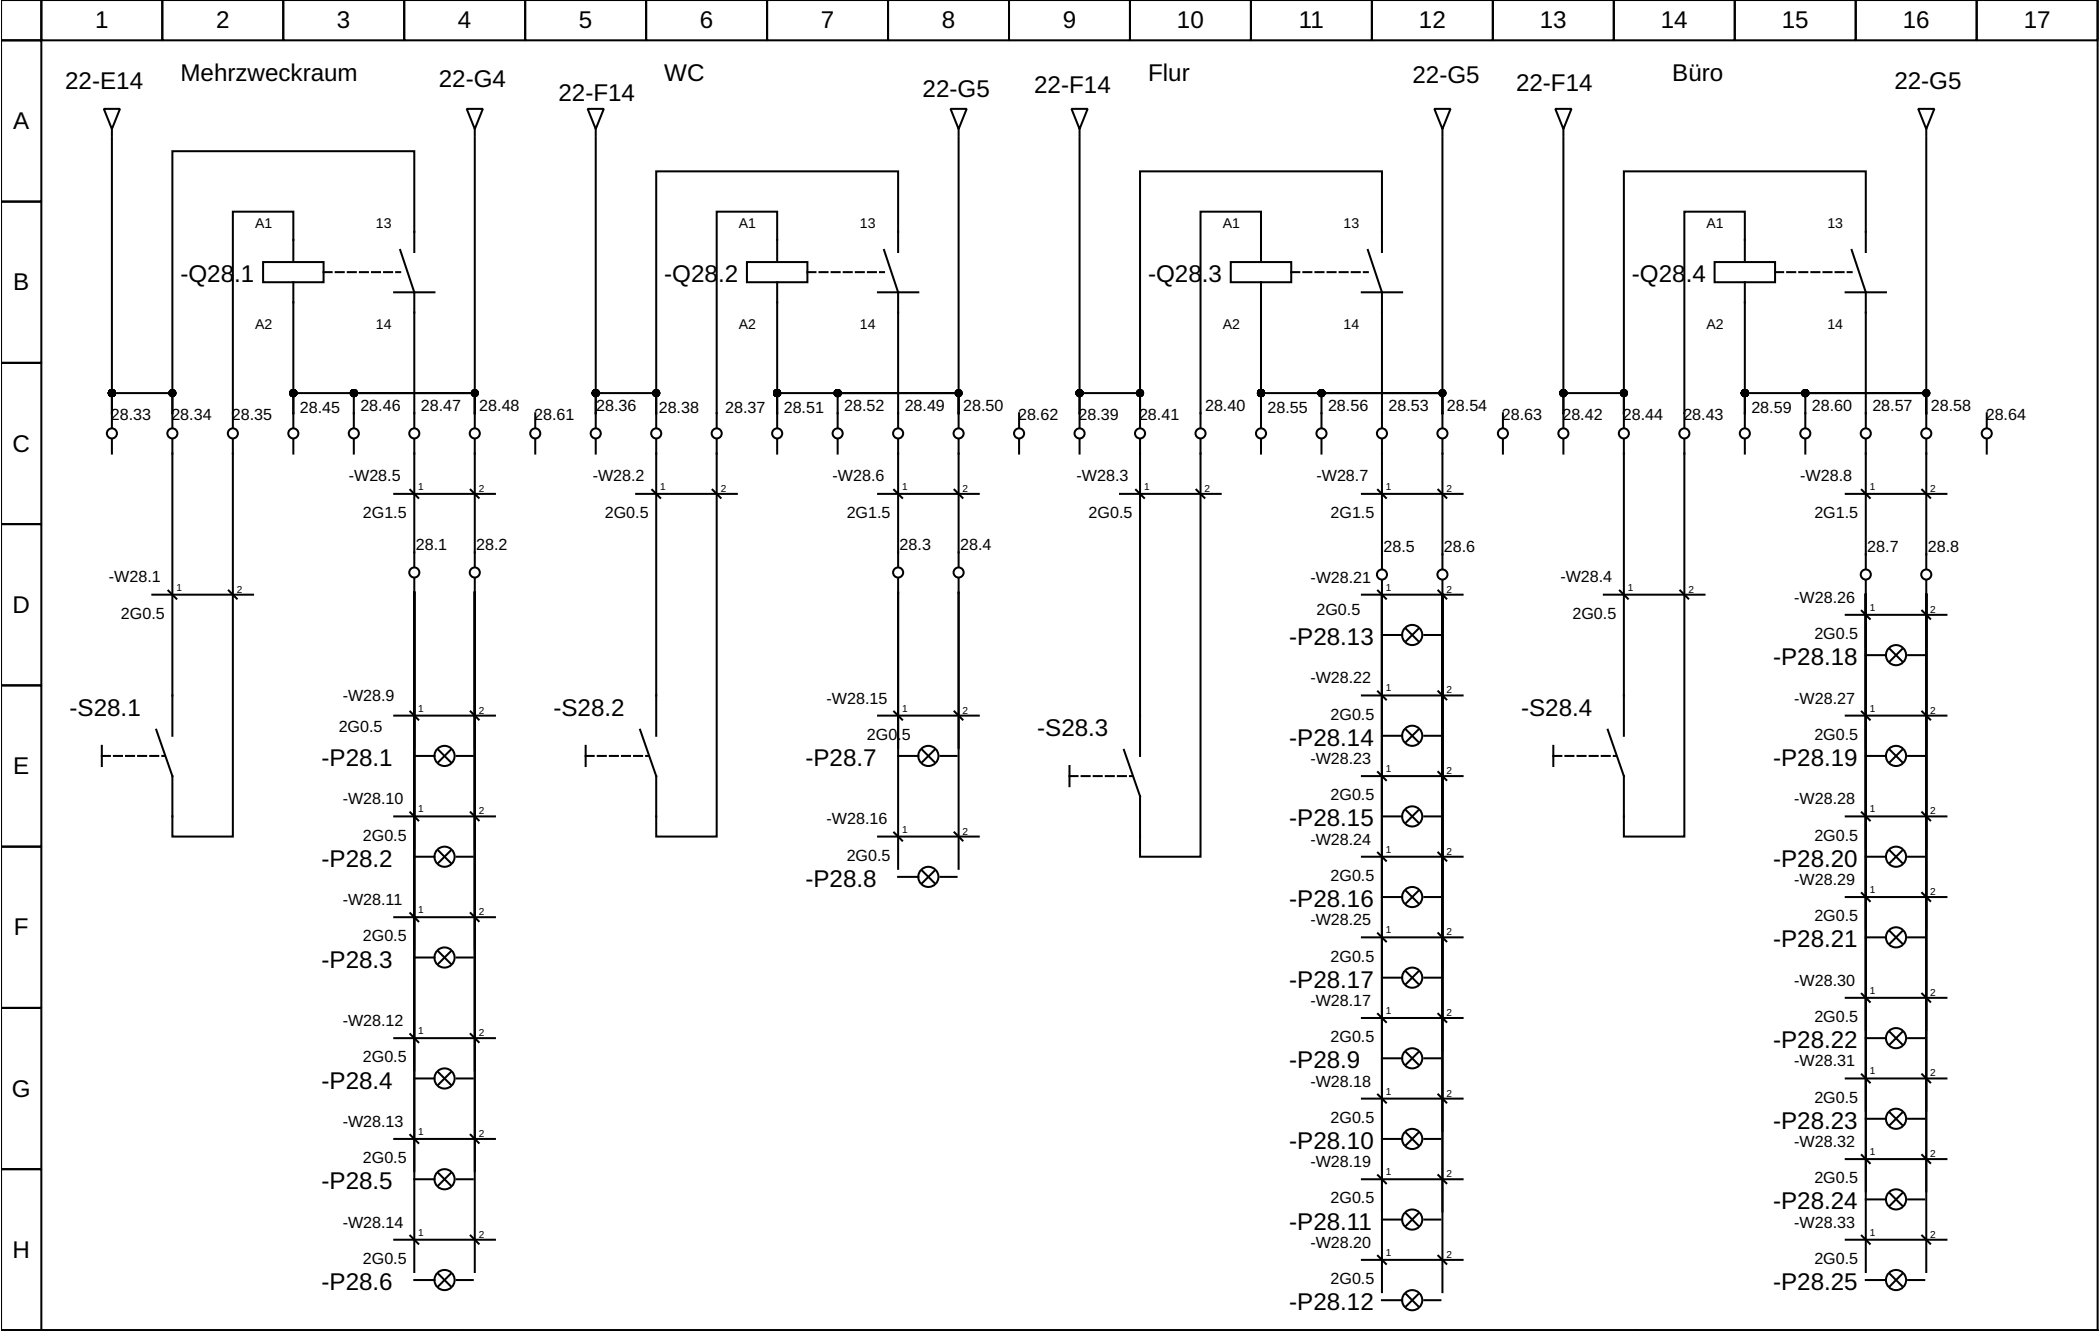


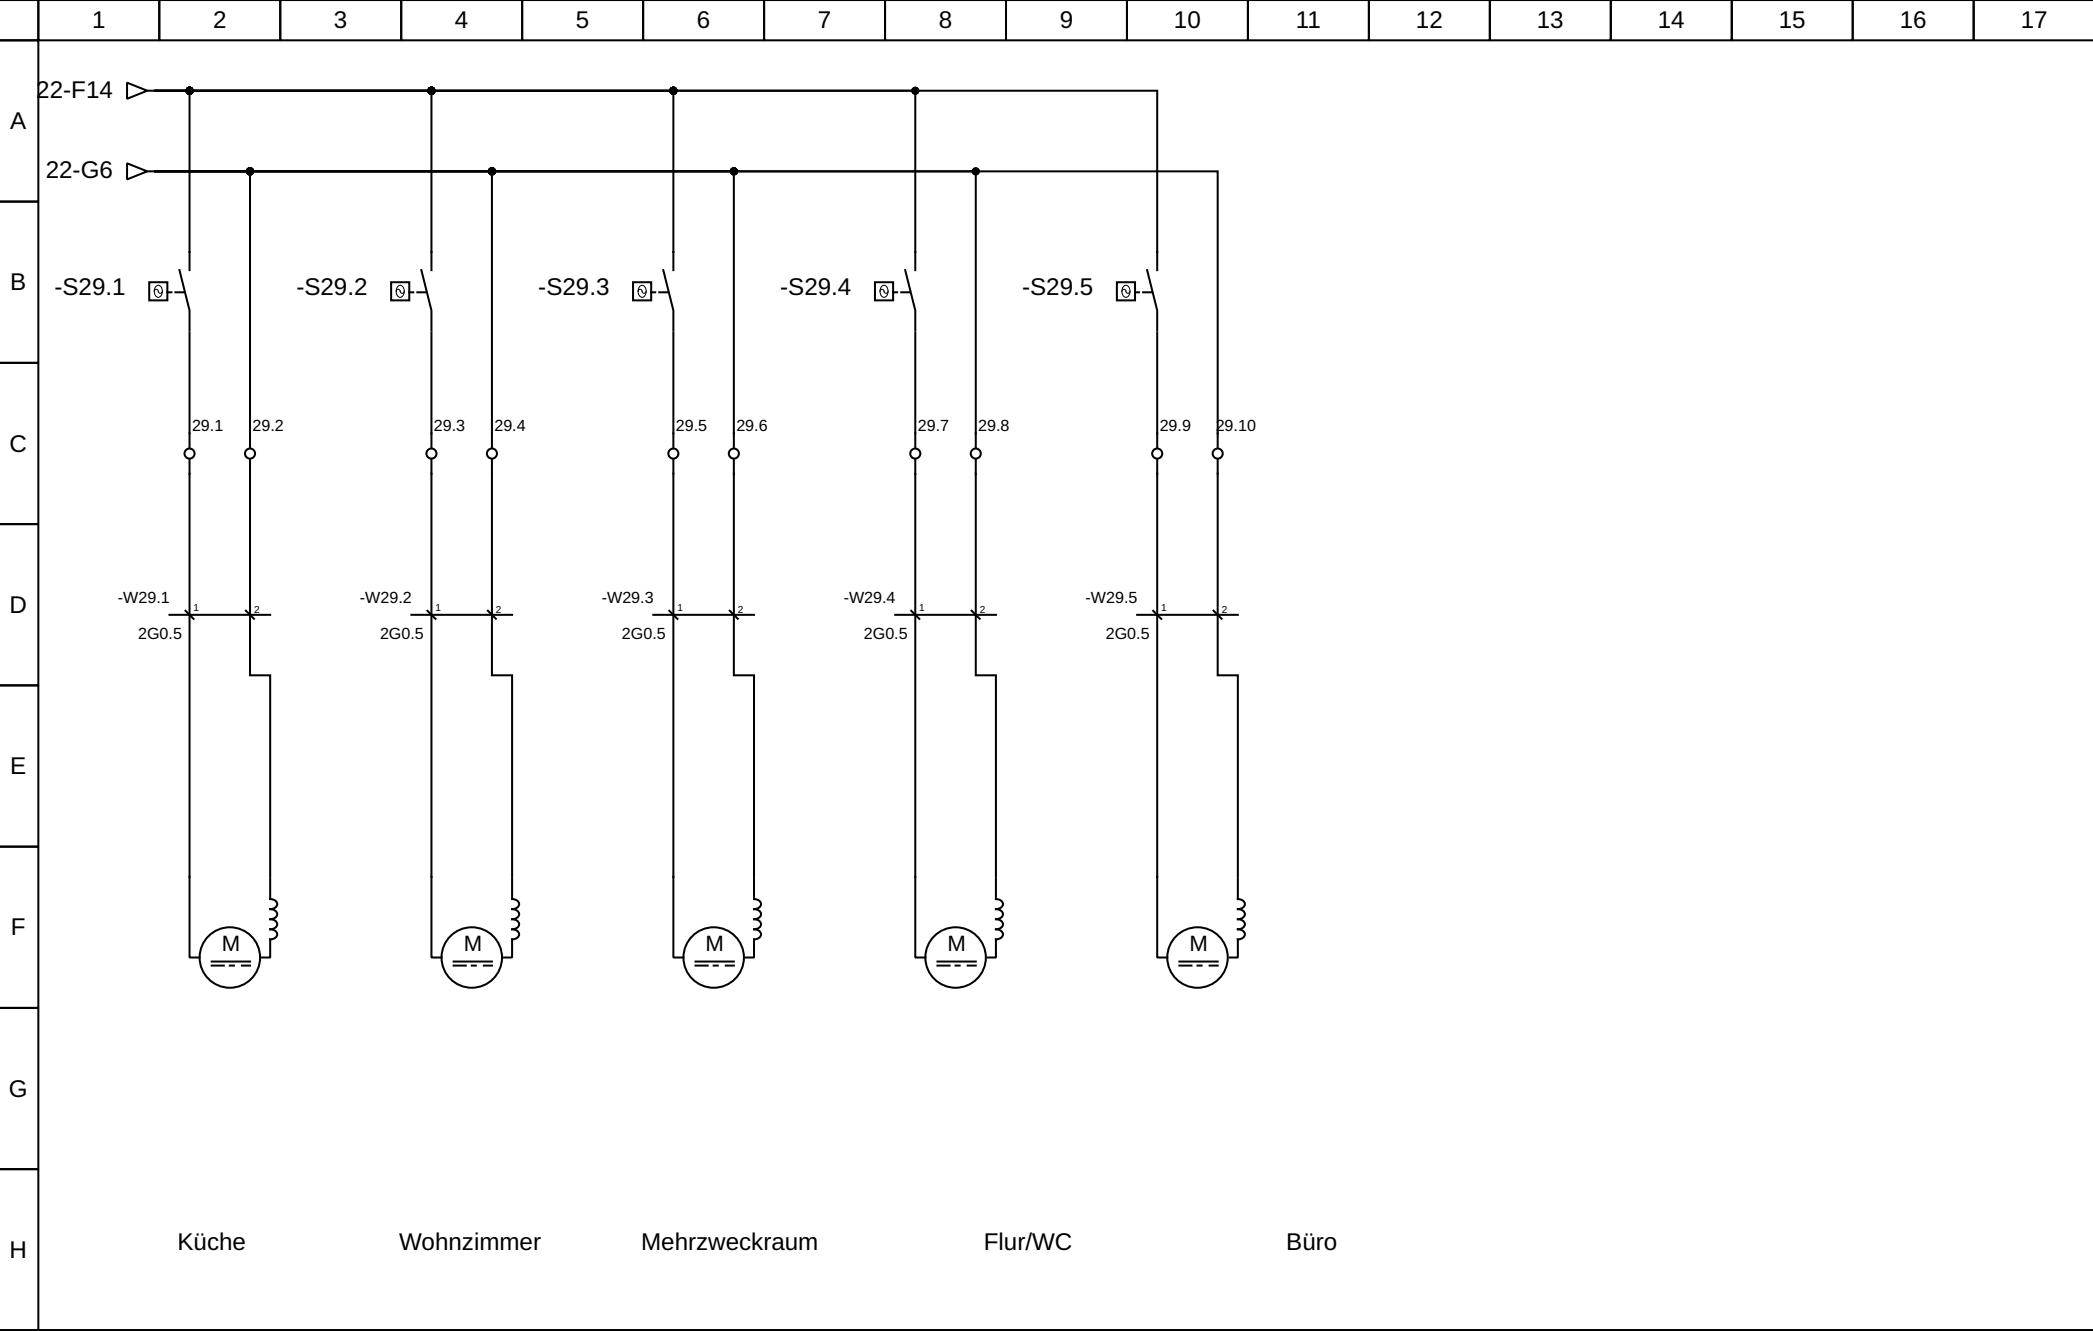



	1	2	3	4	5	6	7	8	9	10	11	12	13	14	15	16	17
A																	
B																	
C																	
D																	
E																	
F																	
G																	
H																	
Autor: Entrich				Daten										Datei:			
Datum:														Seite: 30/38			


	1	2	3	4	5	6	7	8	9	10	11	12	13	14	15	16	17
A																	
B																	
C																	
D	OG Verteile X10 20/38-20.20 20/38-20.21 20/38-20.22 20/38-20.23 20/38-20.24 20/38-20.25 20/38-20.26 20/38-20.27 20/38-20.28 20/38-20.29 21/38-21.30 21/38-21.31 21/38-21.32																
E	OG Verteile X10-N 19/38-19.33 19/38-19.35 19/38-19.34 20/38-20.36 20/38-20.37 20/38-20.38 20/38-20.39 20/38-20.40 20/38-20.41 20/38-20.42 20/38-20.43 20/38-20.44 20/38-20.45 21/38-21.45 21/38-21.46 21/38-21.47																
F	OG Verteile X10-PE 20/38-20.55 20/38-20.56 20/38-20.57 20/38-20.58 20/38-20.59 20/38-20.60 20/38-20.61 20/38-20.62 20/38-20.63 20/38-20.64 21/38-21.65 21/38-21.66 21/38-21.67																
G																	
H																	

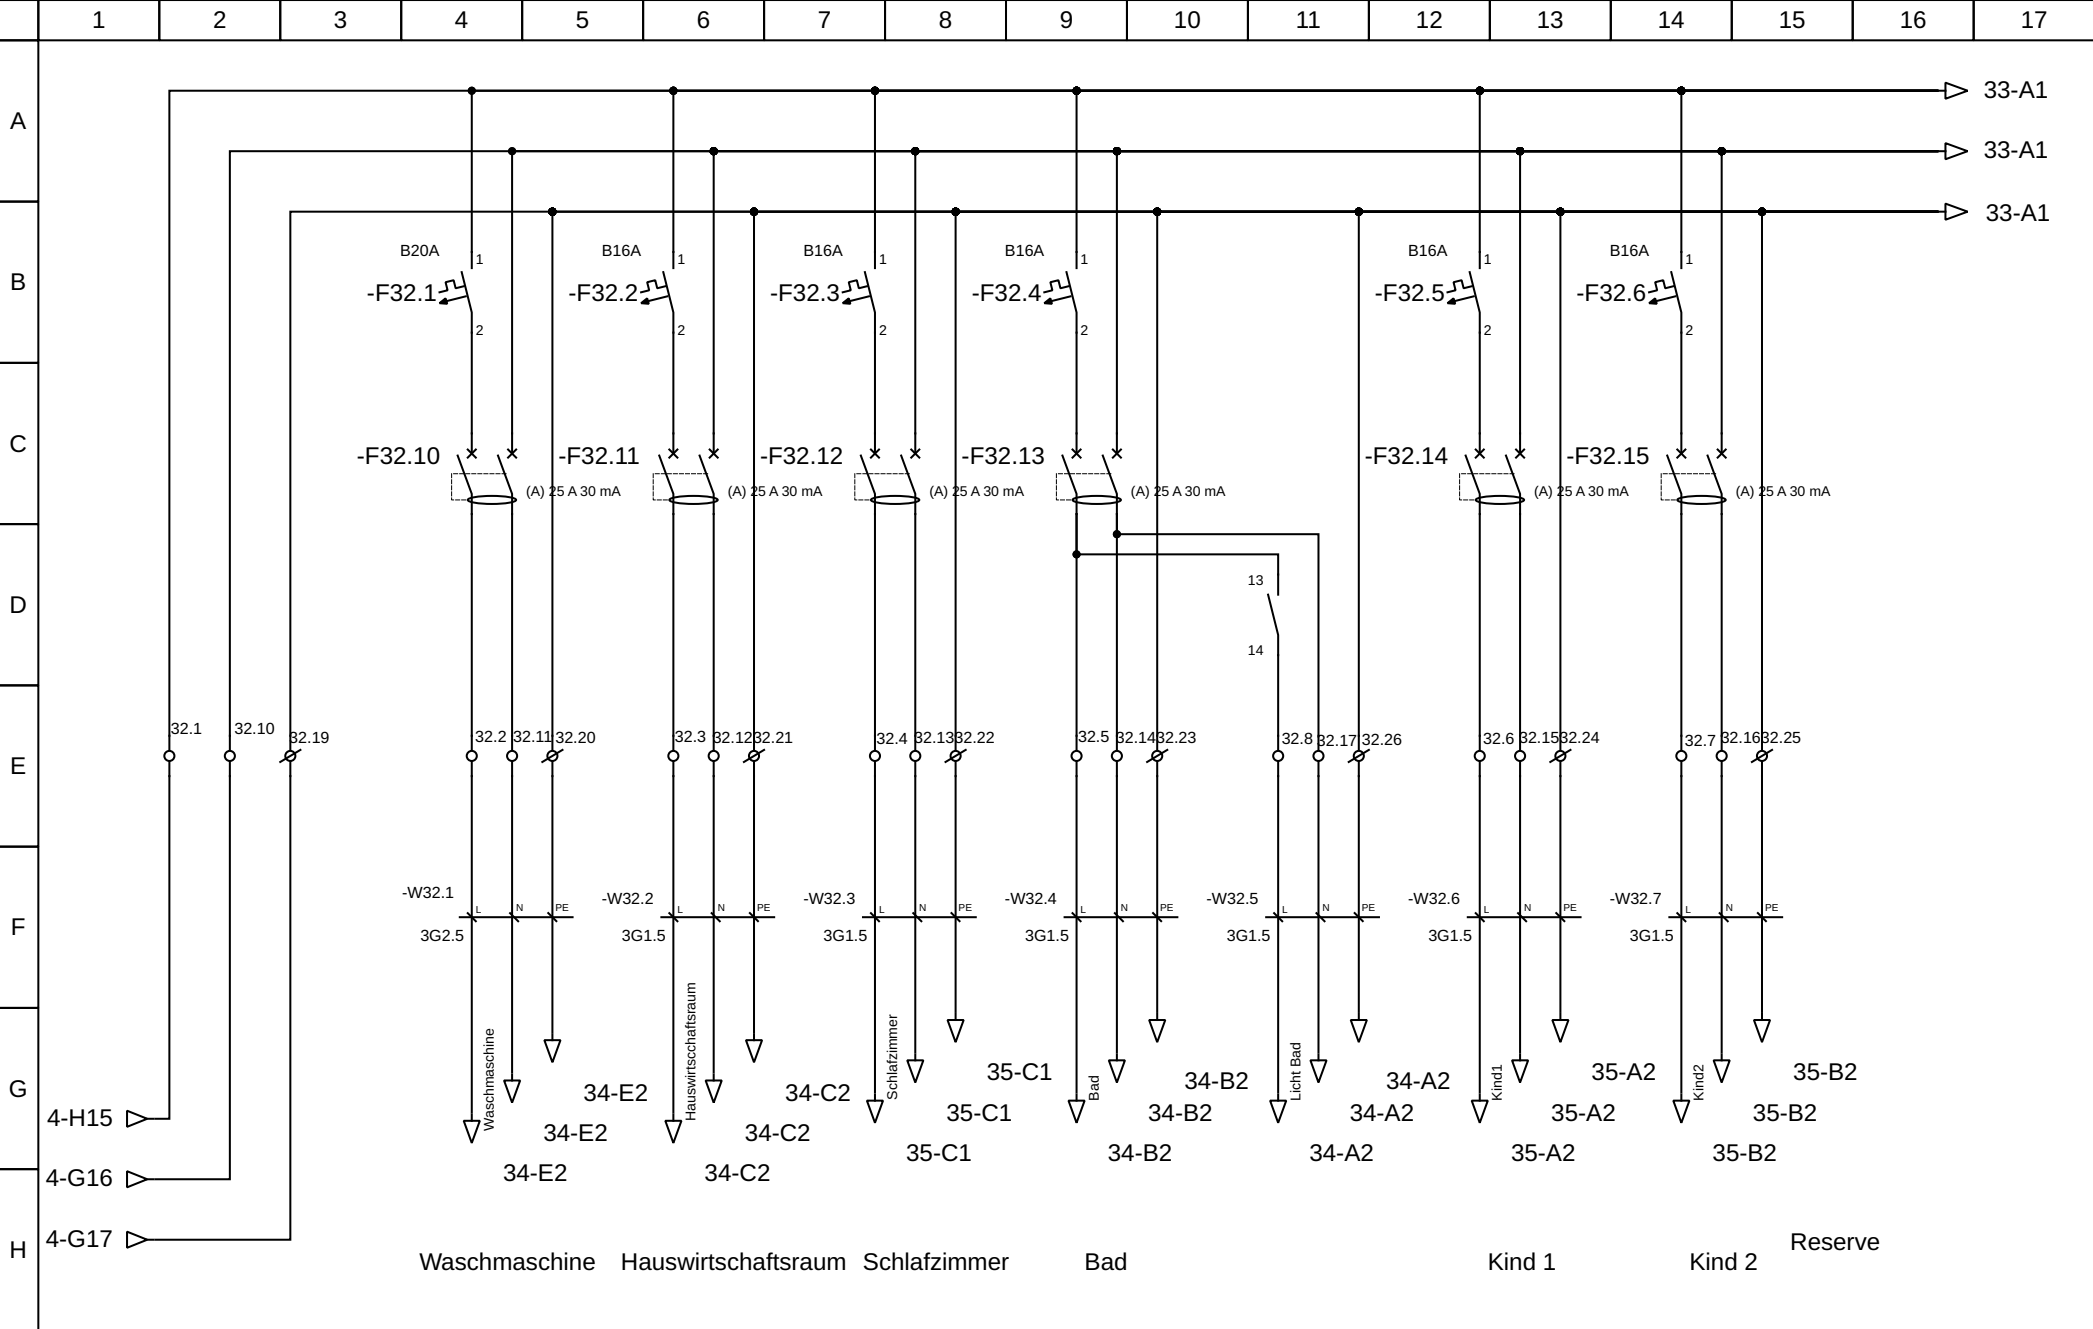


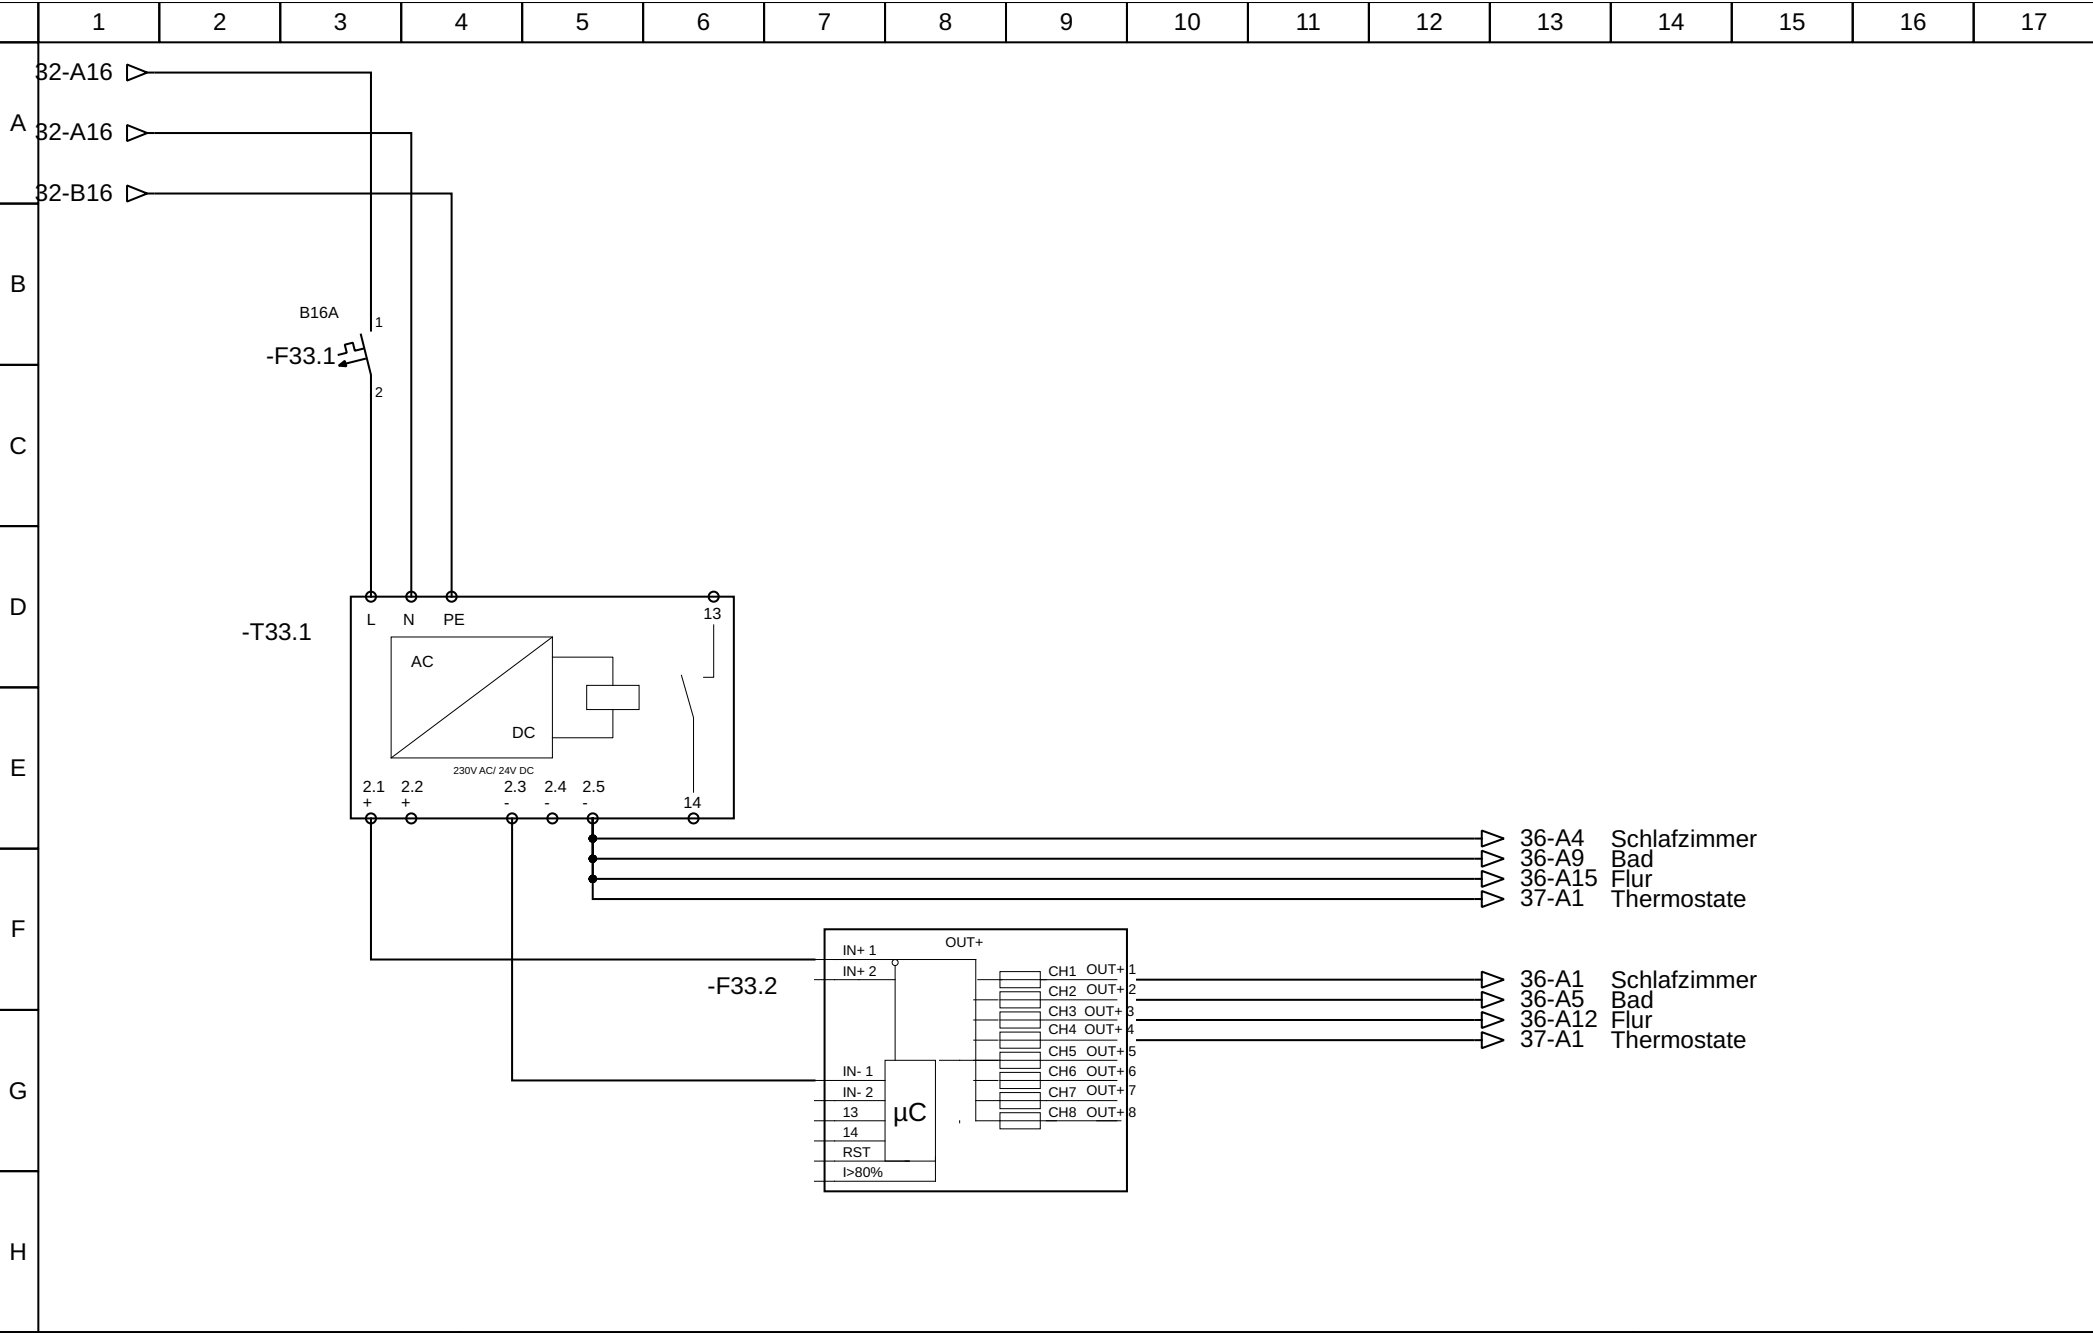

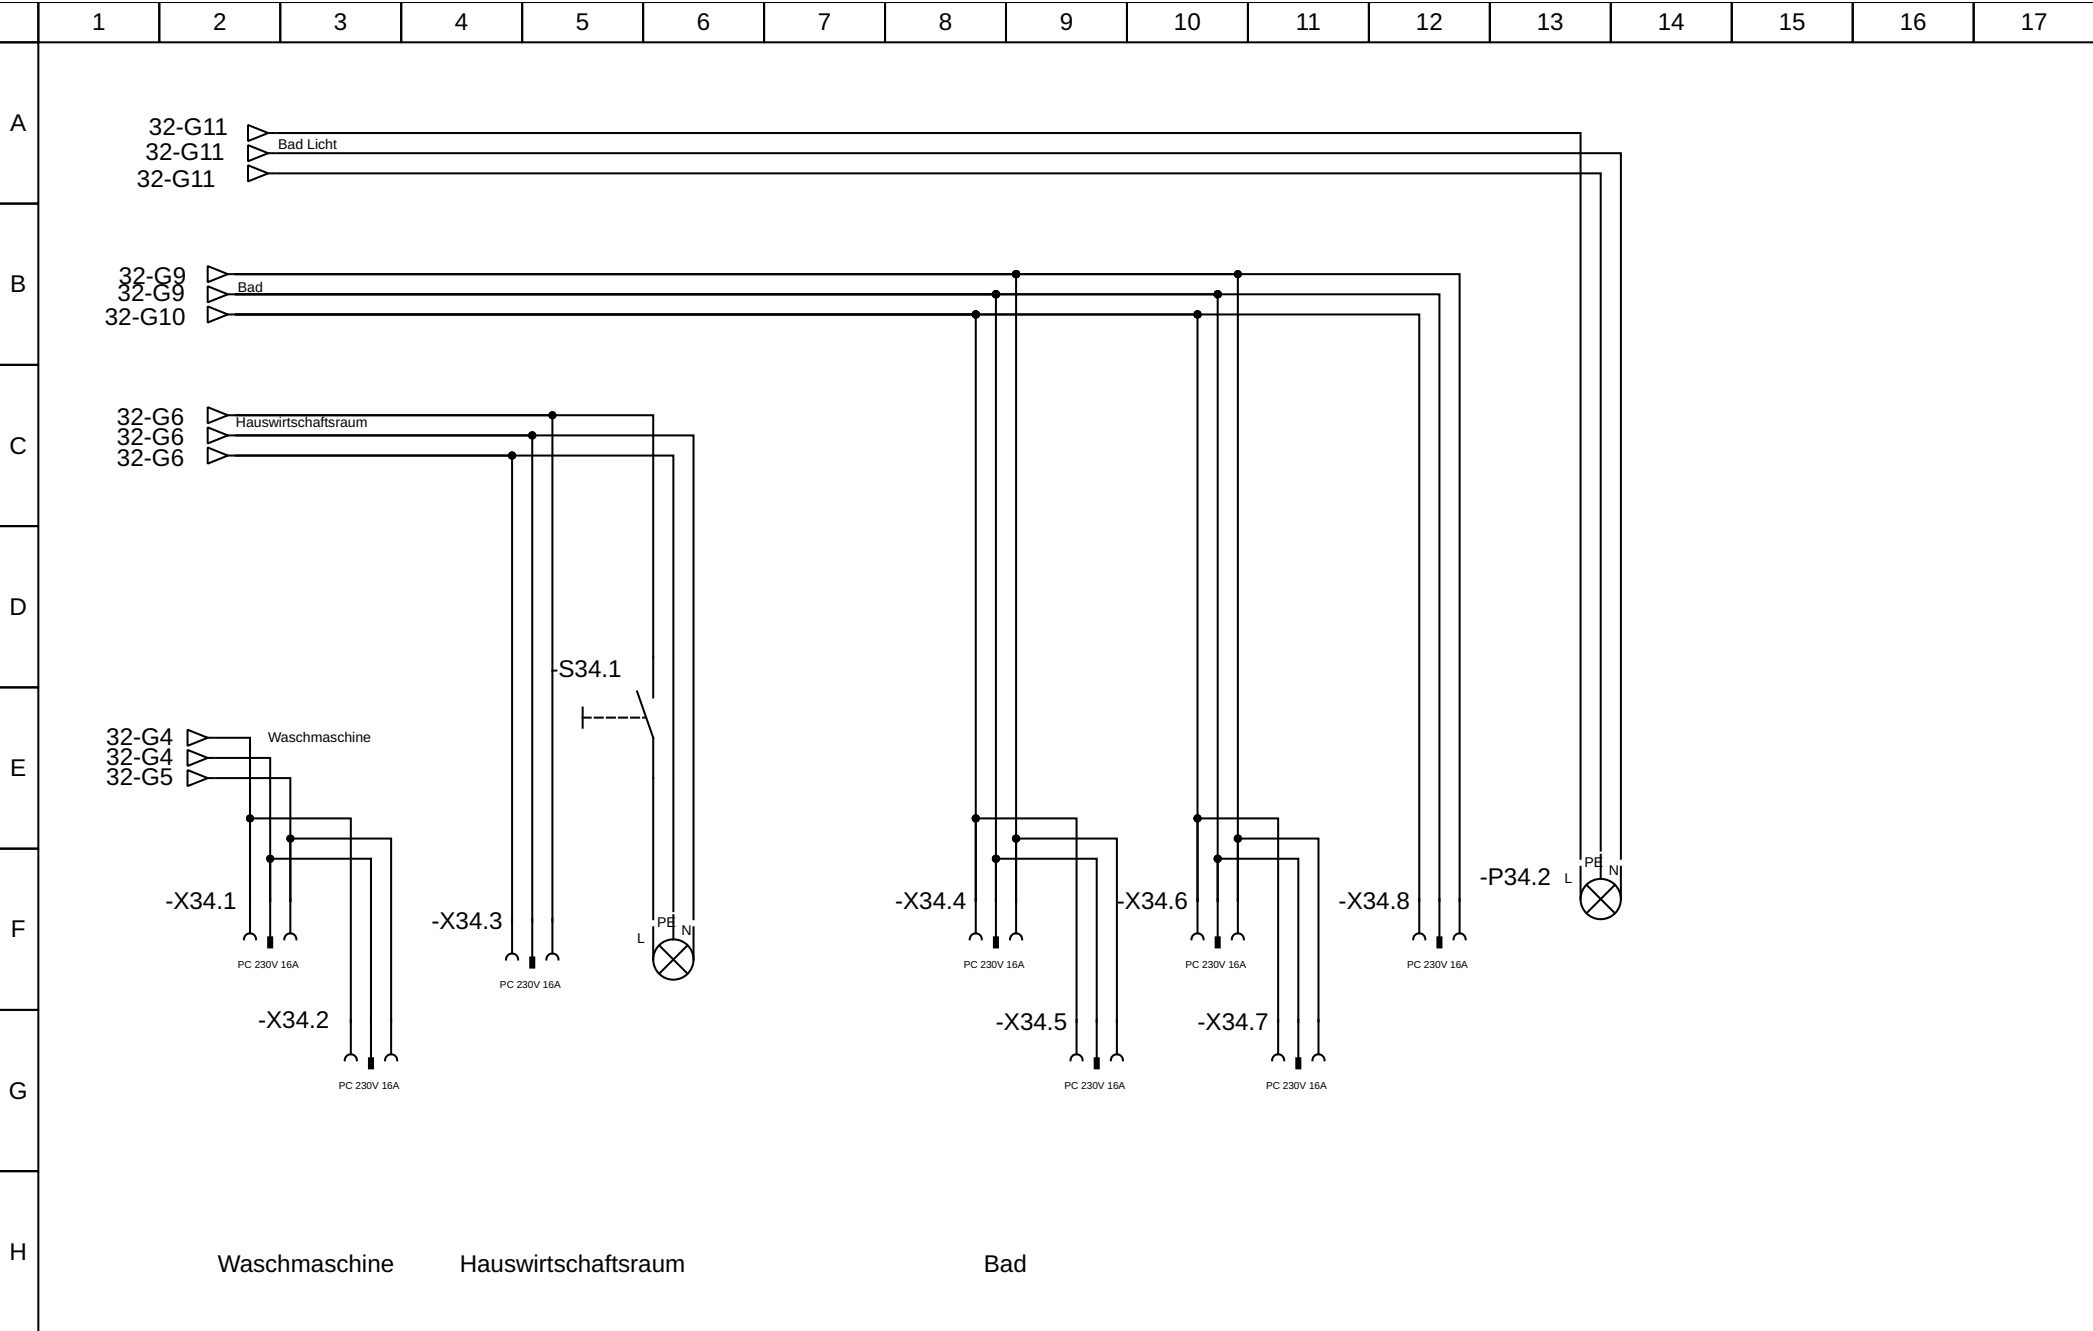

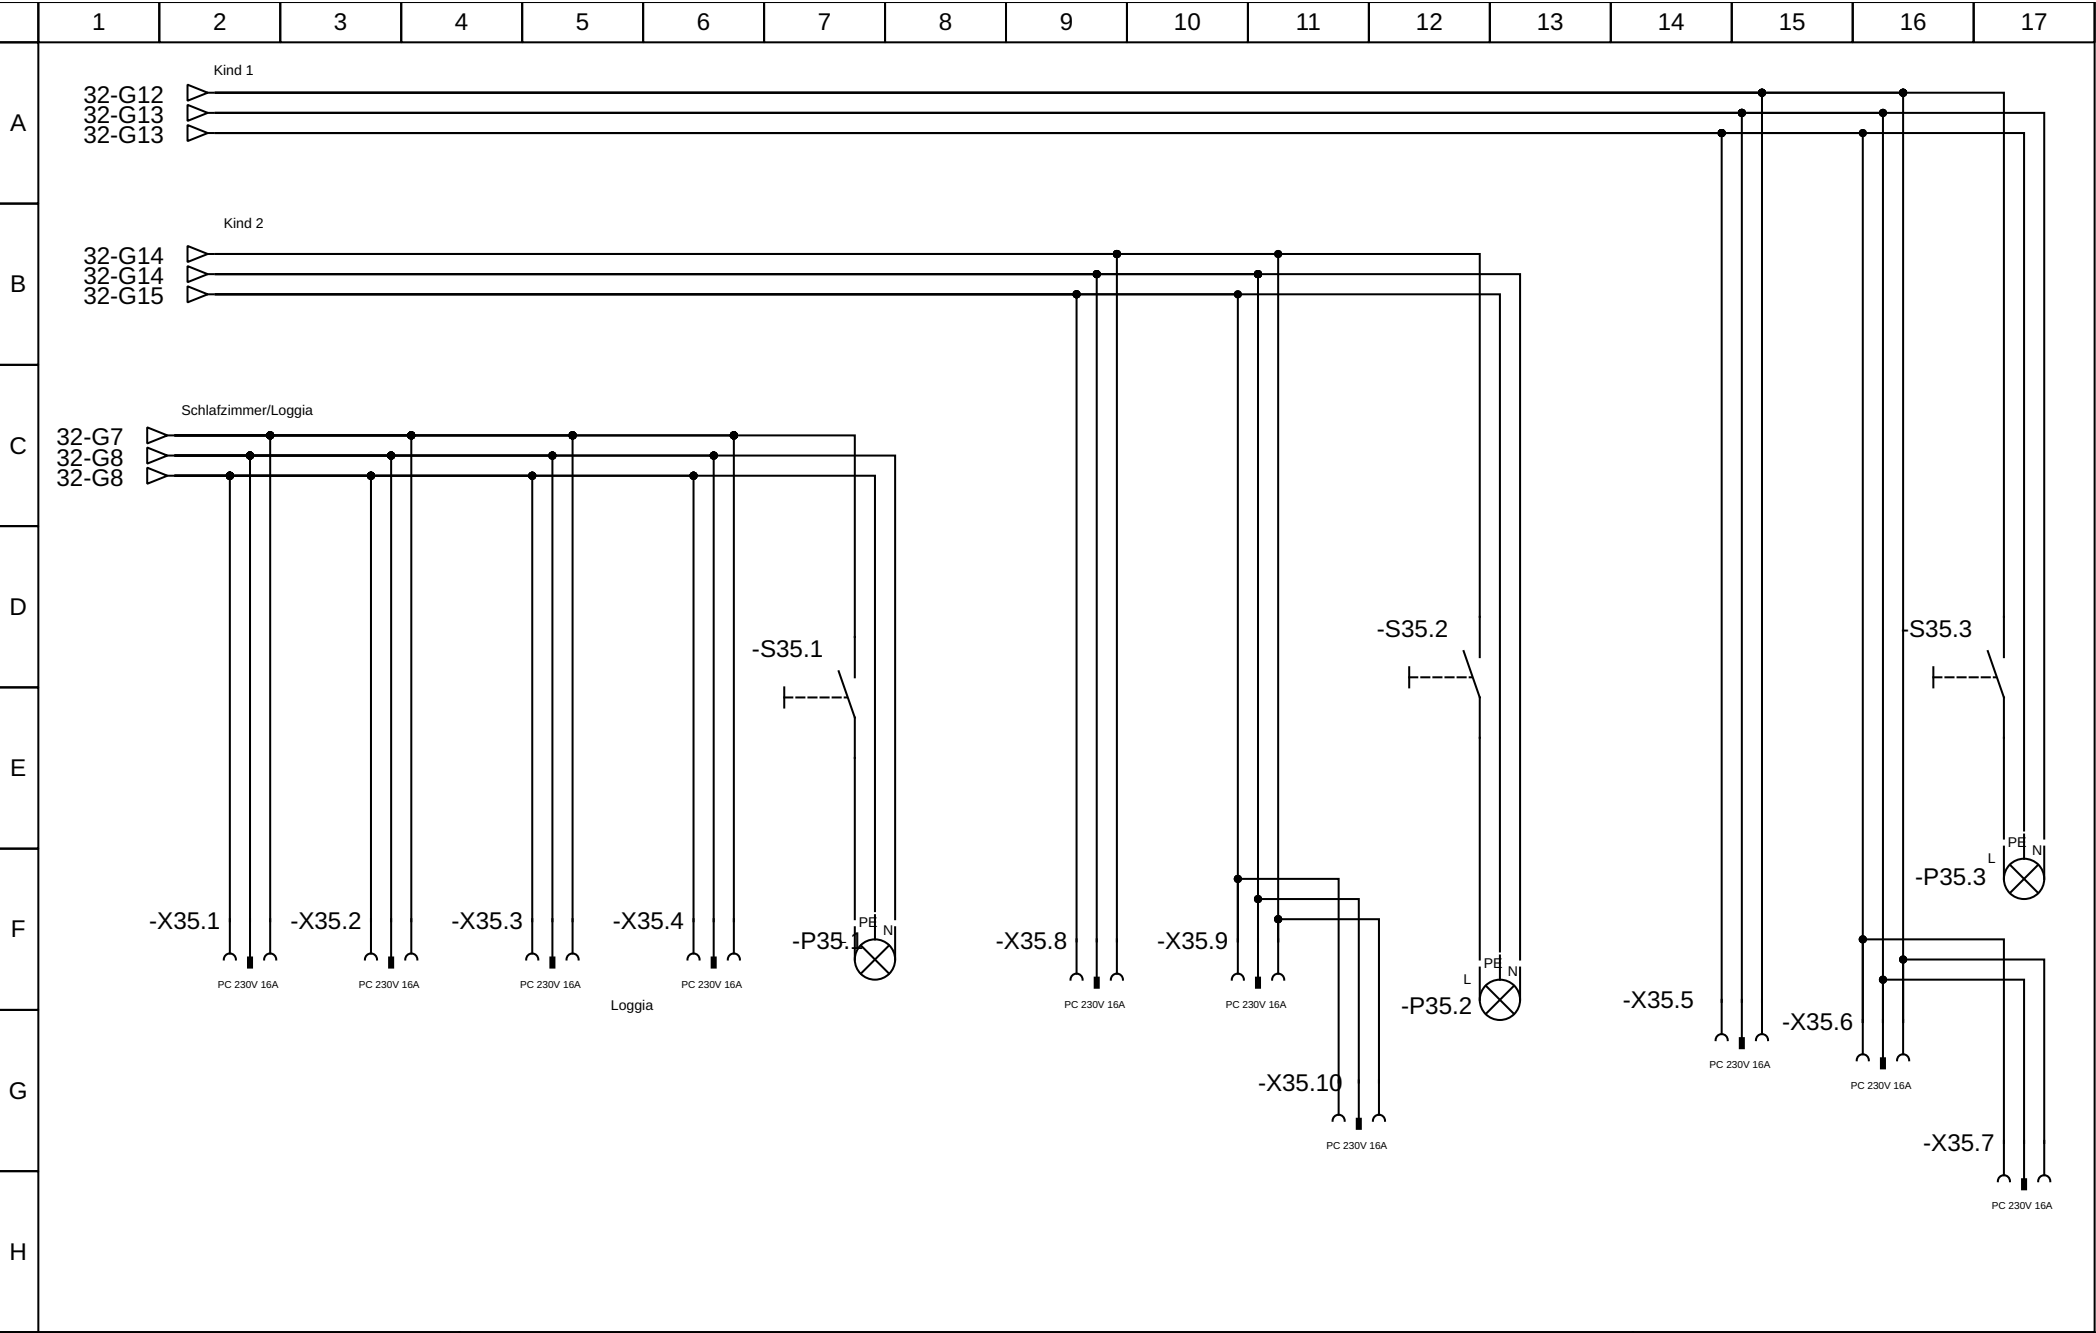

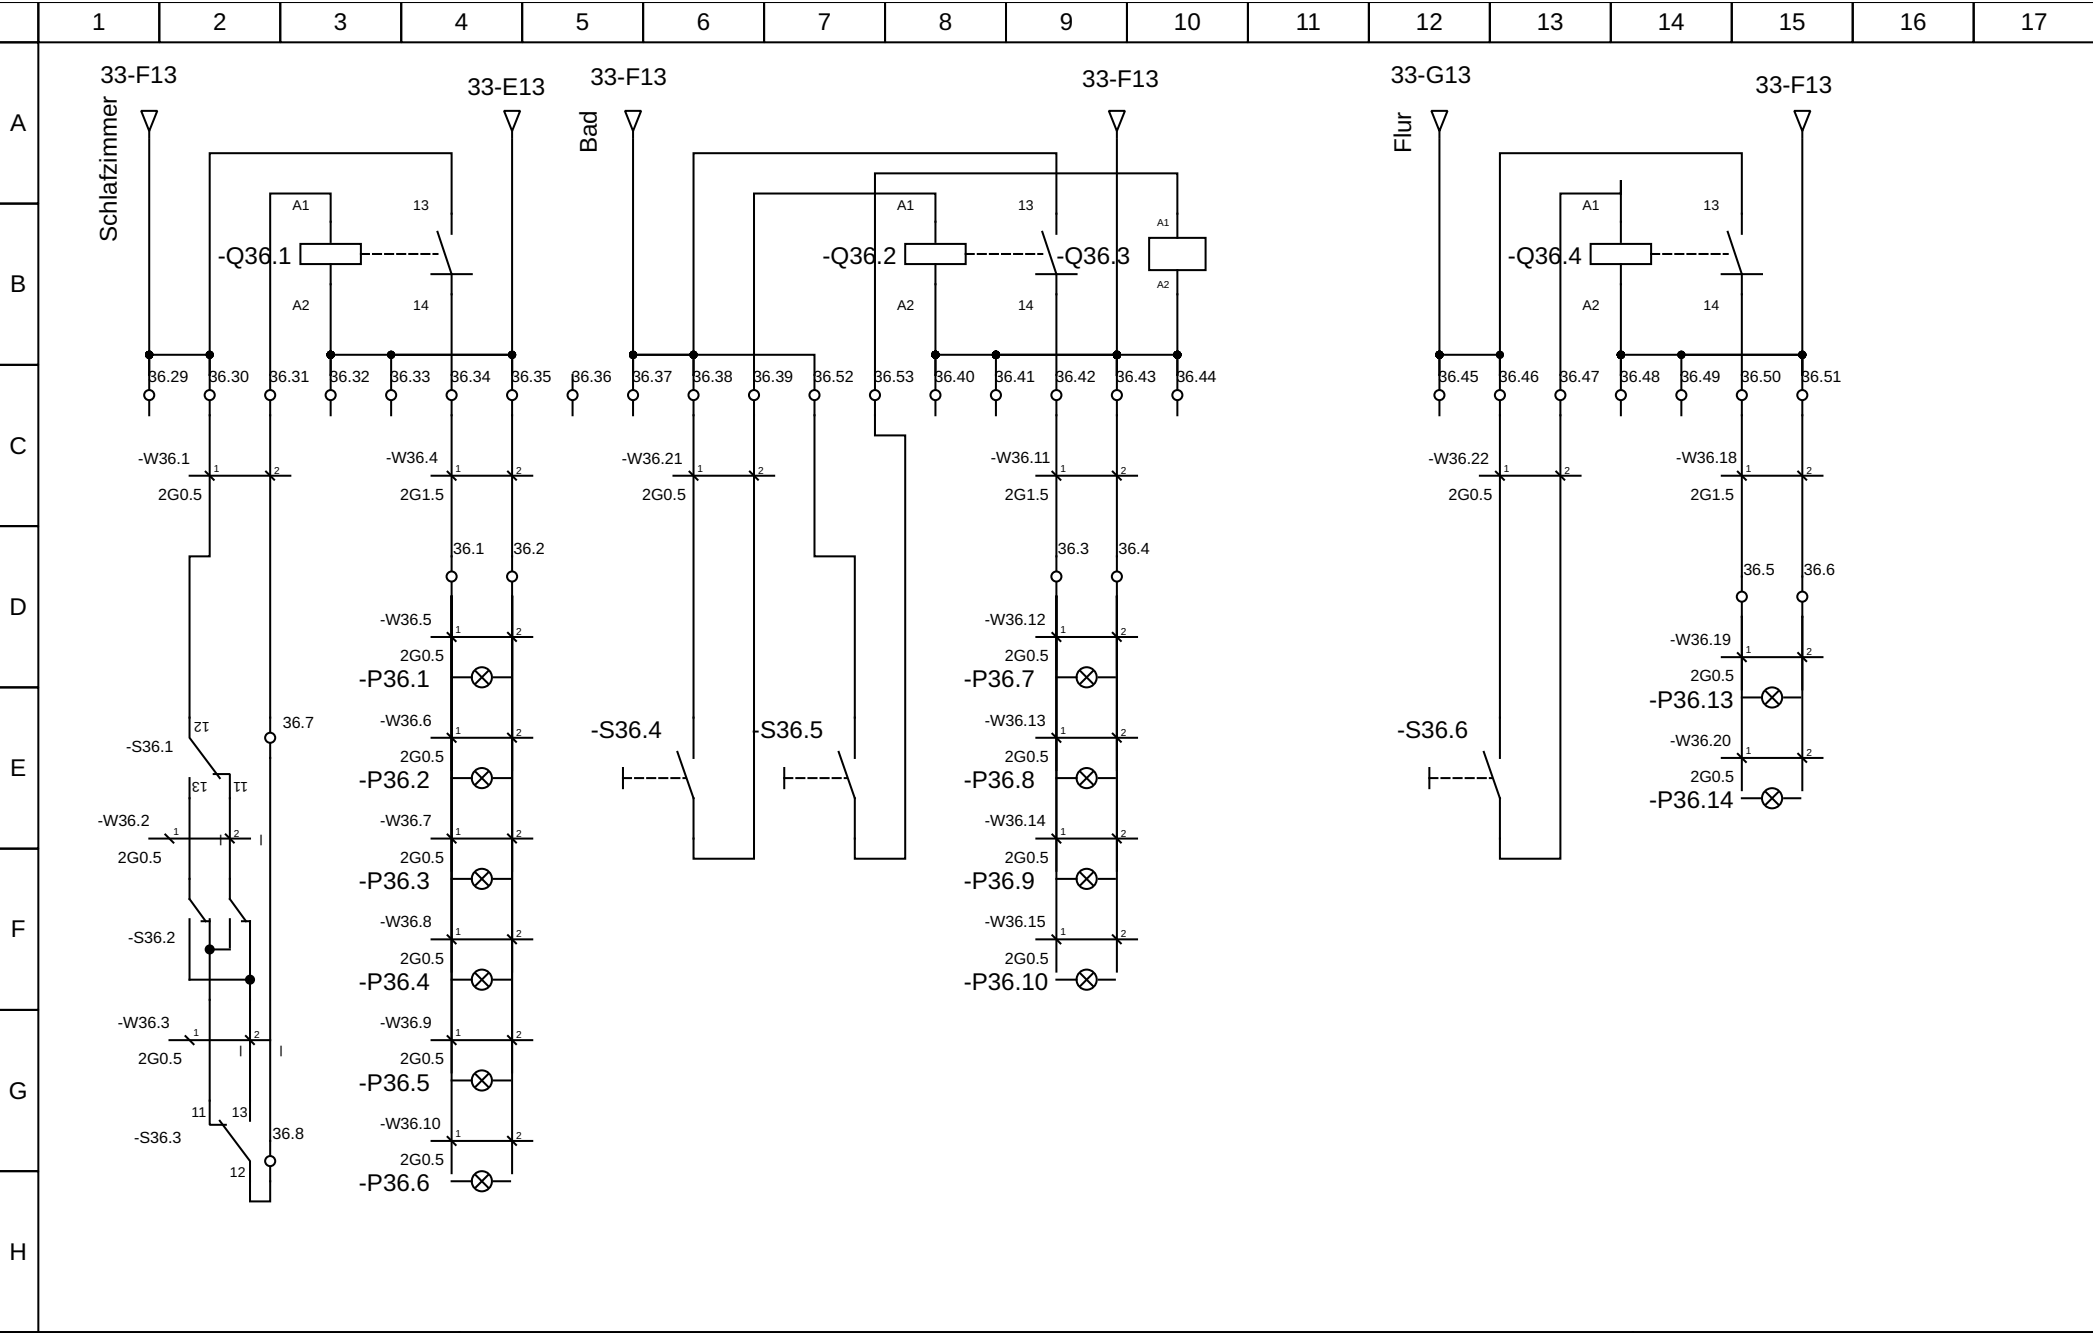

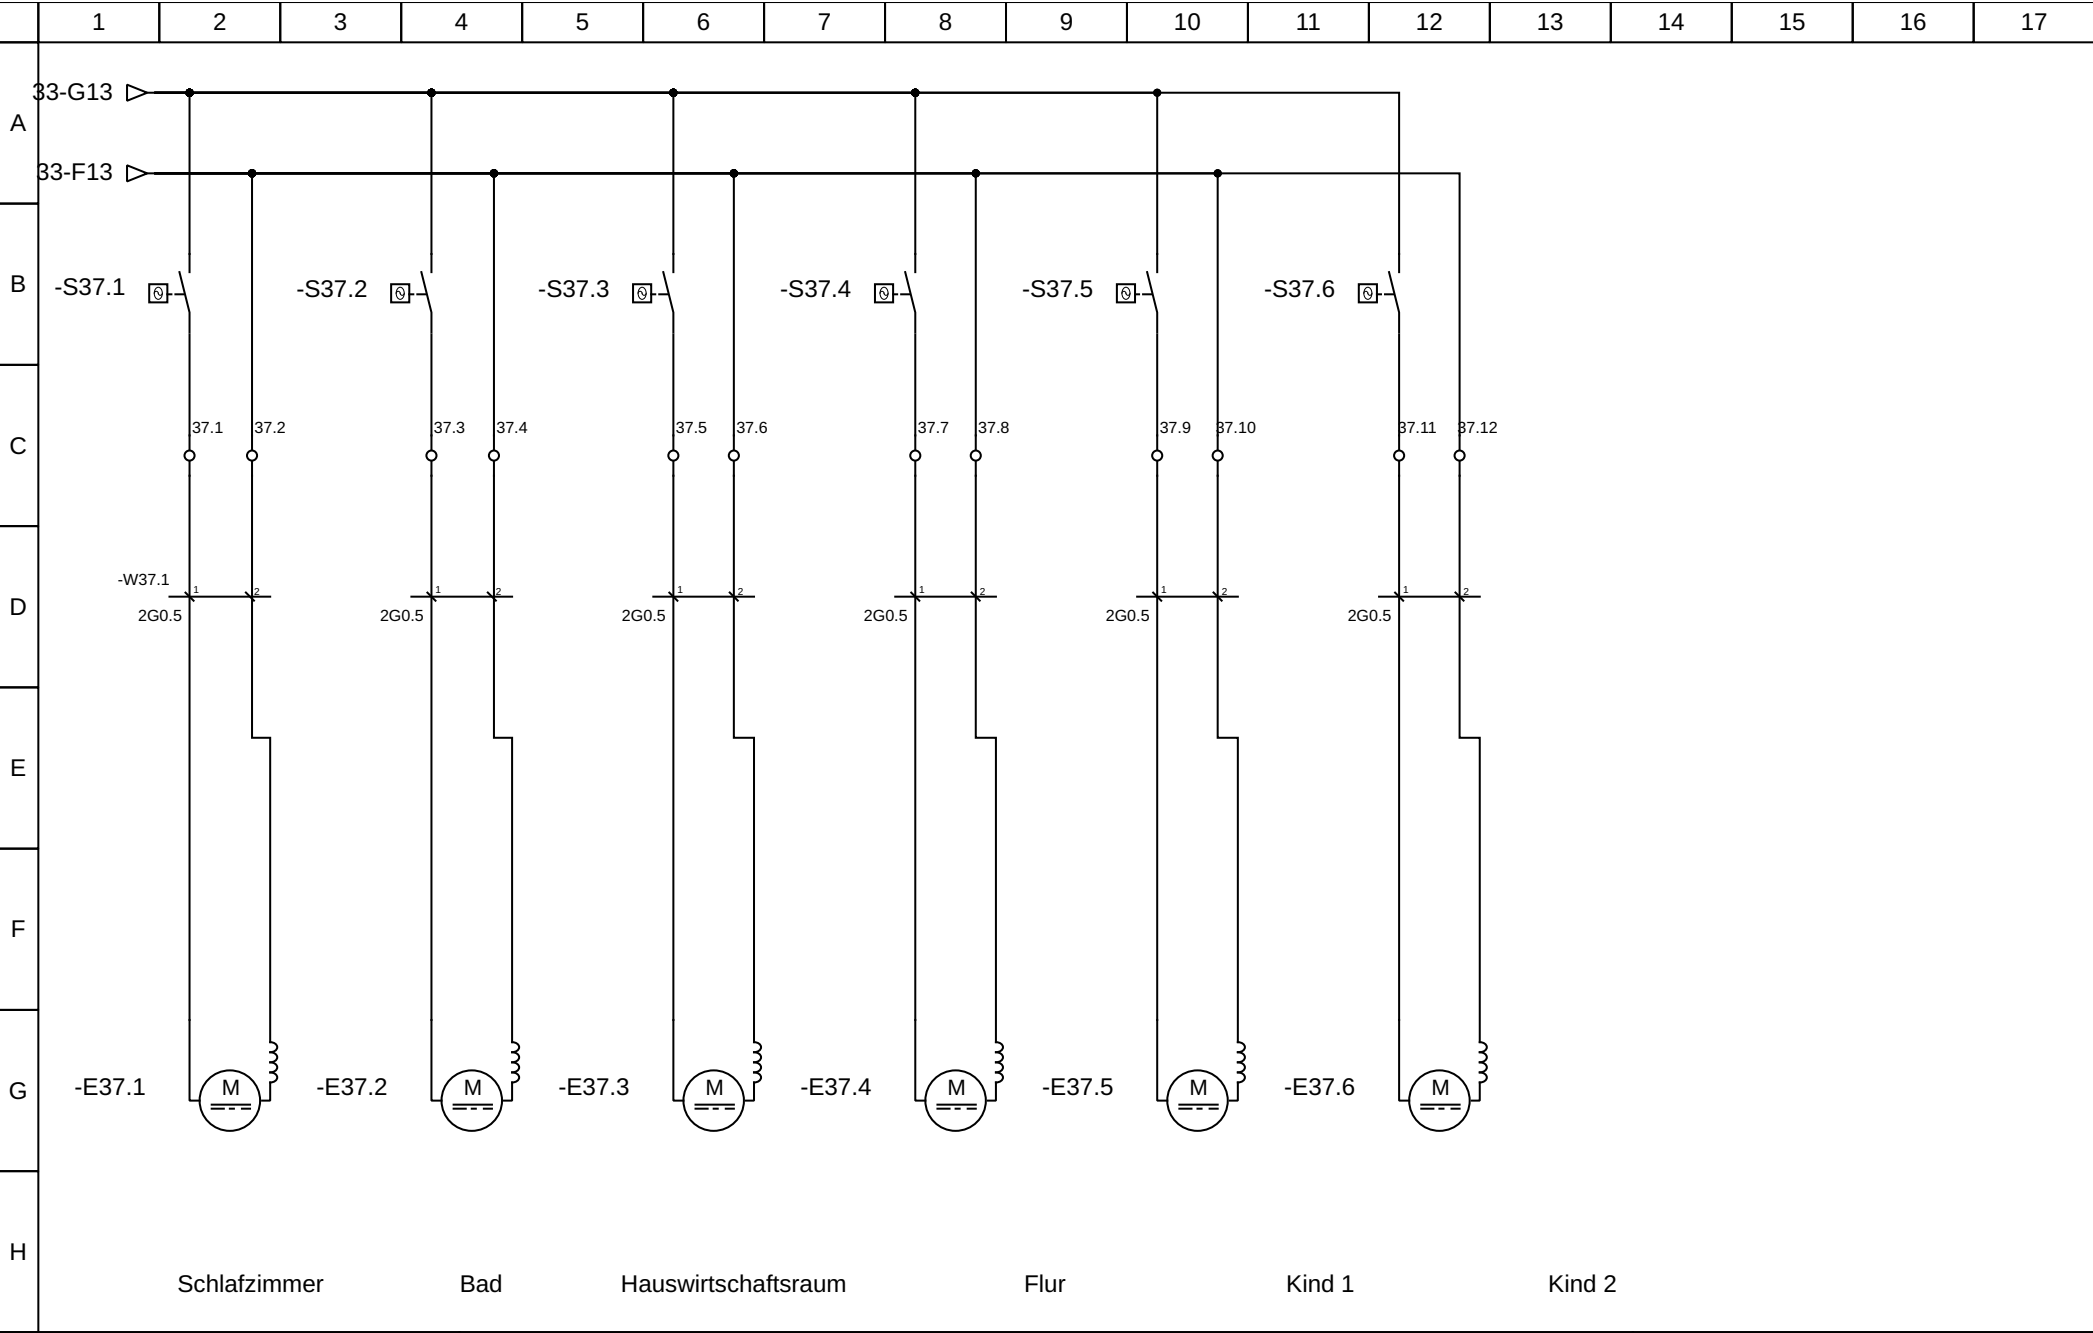

	1	2	3	4	5	6	7	8	9	10	11	12	13	14	15	16	17
A	DG erteile X20 32/38-32.1 32/38-32.2 32/38-32.3 32/38-32.4 32/38-32.5 32/38-32.6 32/38-32.7 32/38-32.8 32/38-32.11 32/38-32.12 32/38-32.13 32/38-32.14 32/38-32.15 32/38-32.16 32/38-32.17 DG erteile X20 24V 36/38-36.31 36/38-36.34 36/38-36.39 36/38-36.42 36/38-36.44 36/38-36.47 36/38-36.50 36/38-36.52 DG erteile X20 - N 32/38-32.10 DG erteile X20 - PE 32/38-32.19 32/38-32.20 32/38-32.21 32/38-32.22 32/38-32.23 32/38-32.24 32/38-32.25 32/38-32.26 DG erteile X20 24V + 36/38-36.29 36/38-36.30 36/38-36.36 36/38-36.37 36/38-36.45 36/38-36.46 36/38-36.38 DG erteile X20 24V - 36/38-36.32 36/38-36.33 36/38-36.35 36/38-36.40 36/38-36.41 36/38-36.43 36/38-36.48 36/38-36.49 36/38-36.51																
B																	
C																	
D																	
E																	
F																	
G																	
H																	